АРХИТЕКТУРНОЕ БЮРО А510

ЖК RIGA HOLIDAY

АЛЬФА-60 (D6)
ДИЗАЙН-ПРОЕКТ

ИЮНЬ 2025

АРХИТЕКТУРНОЕ БЮРО А510
INFO@A510.ru
+7 (495) 532-70-54
www.A510.space | www.A510.ru

СОСТАВ ПРОЕКТА

1	Титульный лист	19	Мастер-спальня 1	37	Схема управления электроприборами
2	Состав проекта	20	Мастер-спальня 2	38	Ведомость верхней и нижней разводки электроприборов
3	Визуализация Кухня|Гостиная 1	21	Мастер-спальня 3	39	План раскладок по стенам
4	Визуализация Кухня|Гостиная 2	22	Мастер-спальня 4	40	Кухня|Гостиная раскладки С З
5	Визуализация Кухня|Гостиная 3	23	Общая планировка	41	Кухня|Гостиная раскладки Ю В
6	Визуализация Кухня|Гостиная 4	24	Обмерный план	42	С|У С З В Ю
7	Визуализация Кухня|Гостиная 5	25	План демонтажа	43	Холл С З В Ю
8	Визуализация Кухня|Гостиная 6	26	План монтажа	44	Мастер спальня С З
9	Холл 1	27	План заполнения проемов	45	Мастер спальня Ю В
10	Холл 2	28	Ведомость дверей	46	Детская спальня С З
11	Холл 3	29	План покрытий пола	47	Детская спальня Ю В
12	Холл 4	30	План финишных покрытий стен		
13	Спальня детская 1	31	План потолков		
14	Спальня детская 2	32	Ведомость основных отделочных материалов		
15	Спальня детская 3	33	План монтажа оборудования		
16	Спальня детская 4	34	Принципиальная схема отопления, кондиционирования		
17	С|У 1	35	Нижняя разводка электроприборов		
18	С|У 2	36	Верхняя разводка электроприборов		

Примечания:
- Комплект чертежей подготовлен на основании рабочей документации предоставленной заказчиком, фактические замеры не проводились
- За отметку +0.000 принят уровень "чистого" пола
- Высотные отметки даны от уровня "чистого" пола
- Финальное утверждения цветов покраски проводится по выкрасам на объекте
- Замеры мебели производятся поставщиком продукции после выполнения чистовой отделки
- Замеры дверных проемов производятся поставщиком продукции после выполнения черновой отделки
- Размеры указаны для справки и при необходимости корректируются по месту, при существенных расхождениях фактических замеров и рабочего проекта
обратиться к разработчику дизайн-проекта для внесения корректив (выполняется в рамках авторского надзора)

Изм.	Кол.уч	Лист	Док.	Подпись	Дата	АЛЬФА-60	Стадия	Лист	Листов
Рук.Маст.		Каличкин А.Д.					Р	2	47
ГАП		Пономарев А.А.							
Архитектор		Муратов Р.Р.				Состав проекта	А510		

АРХИТЕКТУРНОЕ БЮРО А510
INFO@A510.ru
+7 (495) 532-70-54
www.A510.space | www.A510.ru



Изм.	Кол.уч	Лист	Док.	Подпись	Дата	АЛЬФА-60	Стадия	Лист	Листов
Рук.Маст.		Каличкин А.Д.					Р	3	47
ГАП		Пономарев А.А.							
Архитектор		Муратов Р.Р.				Визуализация Кухня|Гостиная 1	A510		

АРХИТЕКТУРНОЕ БЮРО А510
INFO@A510.ru
+7 (495) 532-70-54
www.A510.space | www.A510.ru



Изм.	Кол.уч	Лист	Док.	Подпись	Дата	АЛЬФА-60	Стадия	Лист	Листов
Рук.Маст.		Каличкин А.Д.					Р	5	47
ГАП		Пономарев А.А.							
Архитектор		Муратов Р.Р.				Визуализация Кухня|Гостиная 3	A510		

АРХИТЕКТУРНОЕ БЮРО А510
+7 (495) 532-70-54
INFO@A510.ru
www.A510.space | www.A510.ru




Изм.	Кол.уч	Лист	Док.	Подпись	Дата	АЛЬФА-60	Стадия	Лист	Листов
Рук.Маст.		Каличкин А.Д.					Р	13	47
ГАП		Пономарев А.А.							
Архитектор		Муратов Р.Р.				Спальня детская 1	A510		

АРХИТЕКТУРНОЕ БЮРО А510
+7 (495) 532-70-54
INFO@A510.ru
www.A510.space | www.A510.ru




Изм.	Кол.уч	Лист	Док.	Подпись	Дата	АЛЬФА-60	Стадия	Лист	Листов
Рук.Маст.		Каличкин А.Д.					Р	19	47
ГАП		Пономарев А.А.							
Архитектор		Муратов Р.Р.				Мастер-спальня 1			

А510

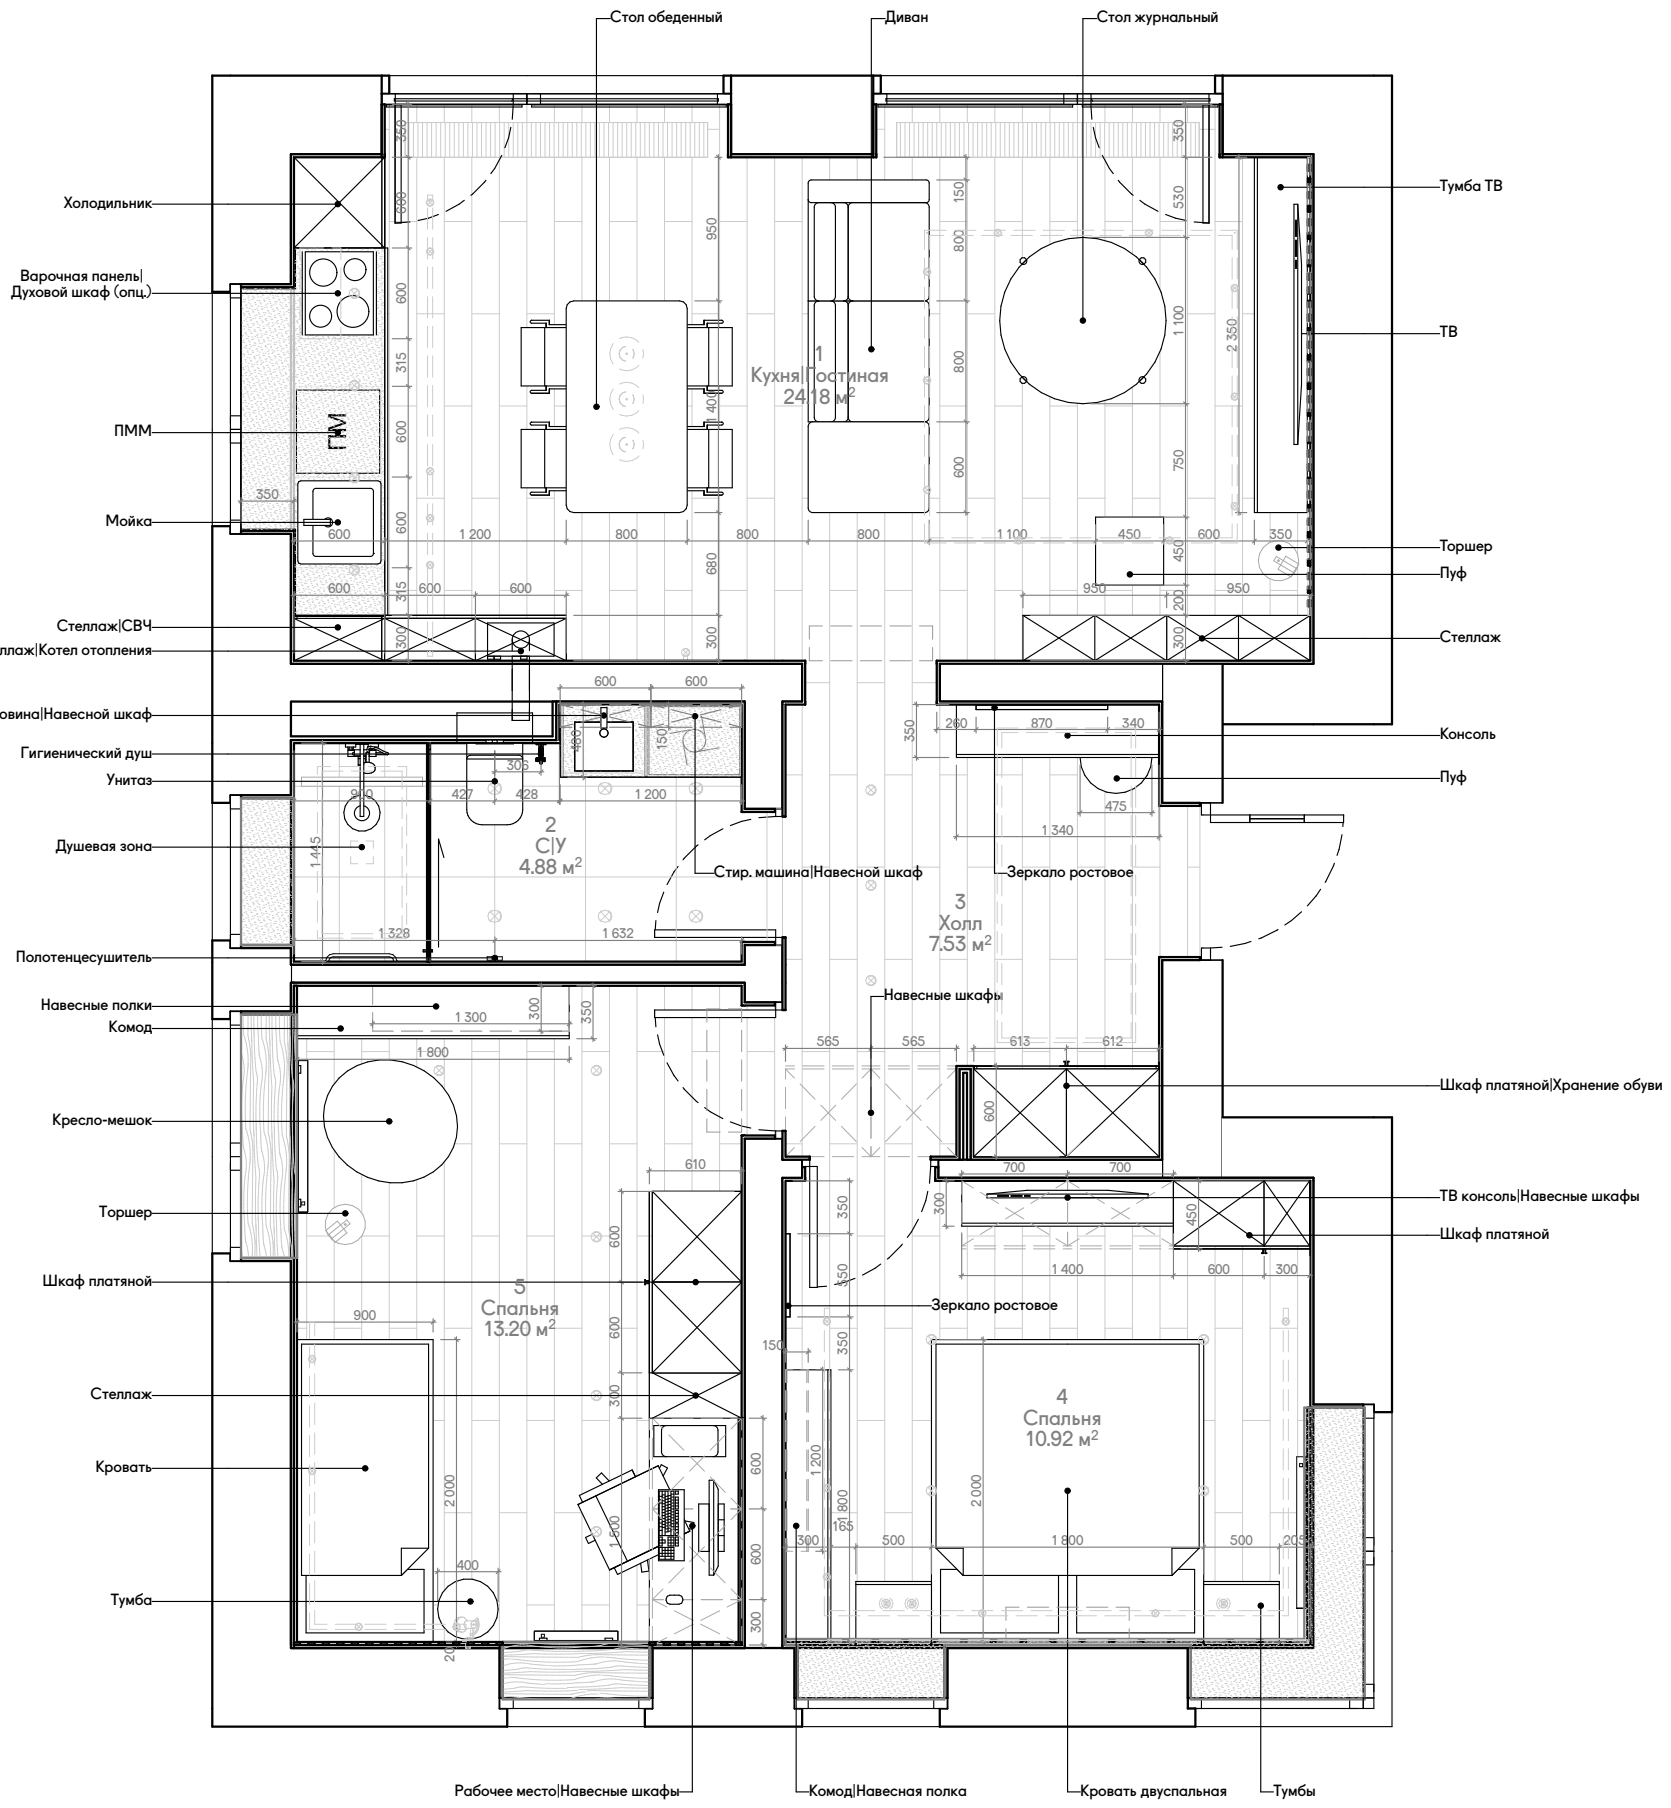


Изм.	Кол.уч	Лист	Док.	Подпись	Дата	АЛЬФА-60	Стадия	Лист	Листов
Рук.Маст.		Каличкин А.Д.					Р	23	47
ГАП		Пономарев А.А.							
Архитектор		Муратов Р.Р.				Общая планировка			

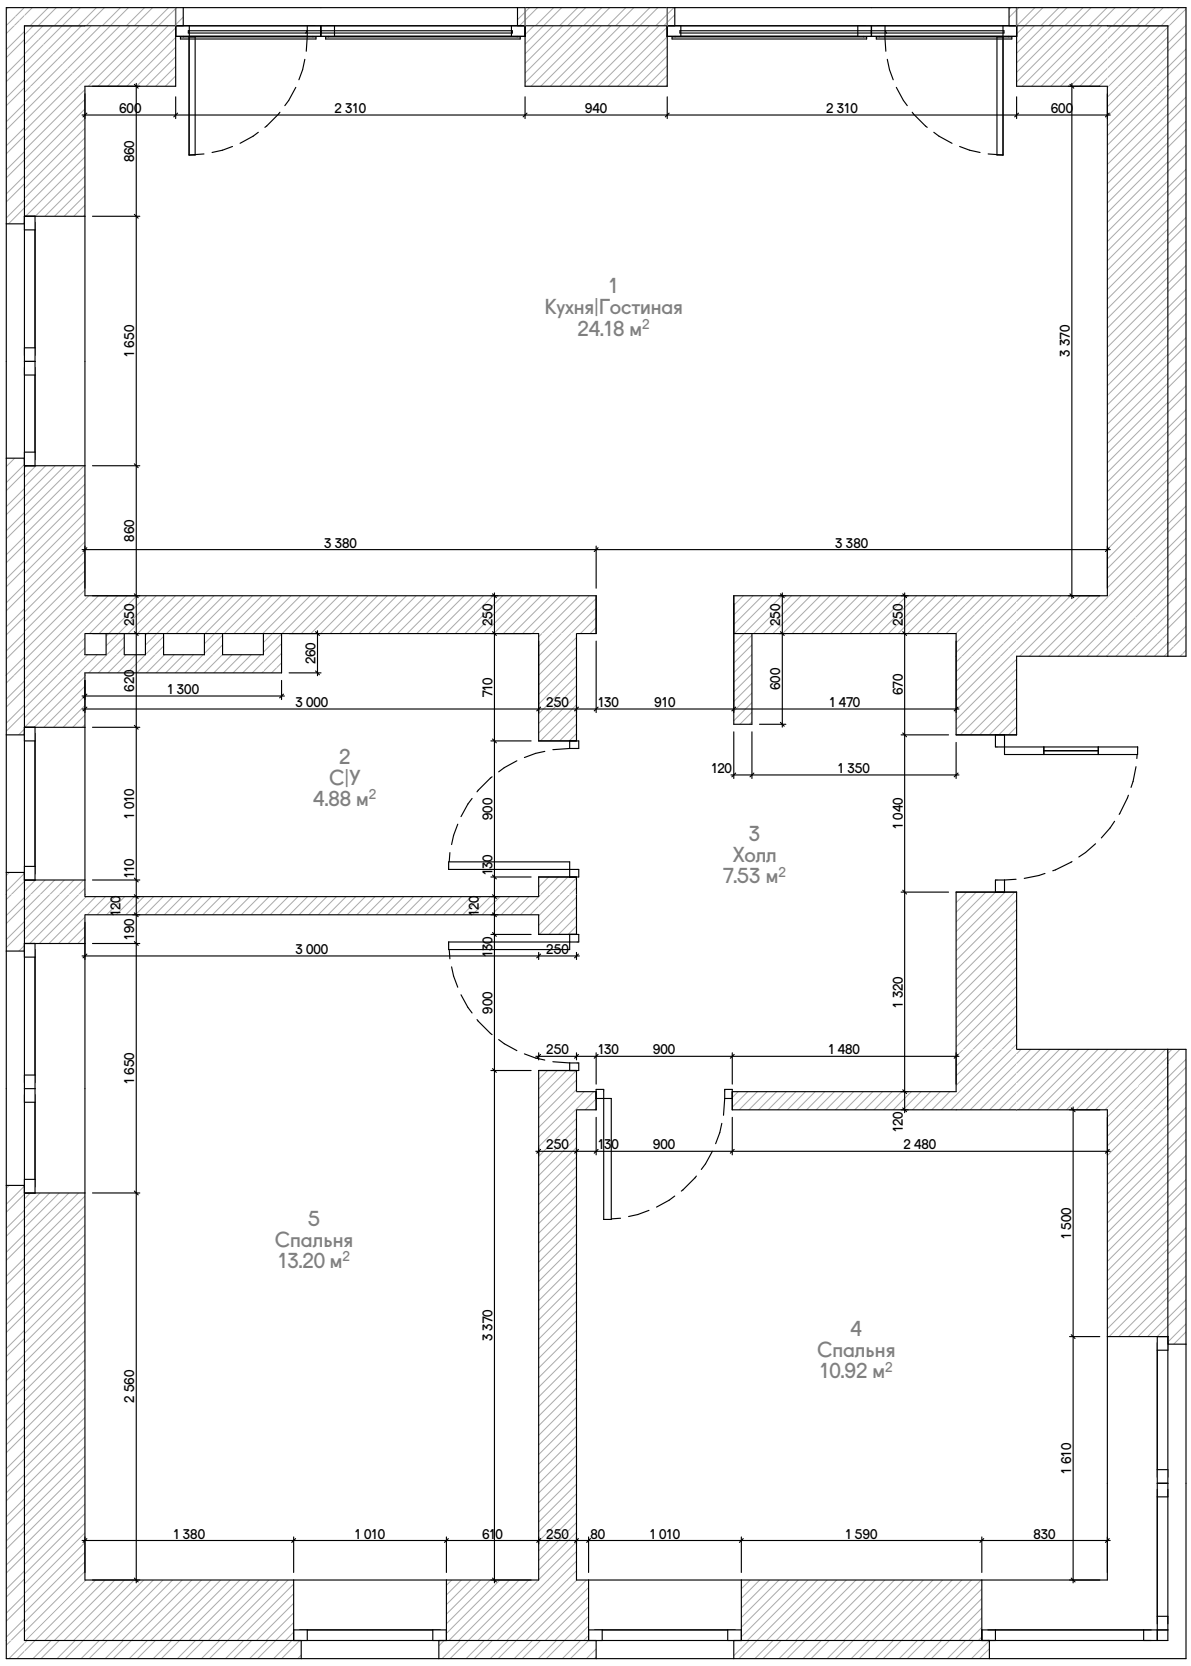


*Размеры указаны на основании рабочей документации, перед началом работ выполнить обмеры фактической геометрии

Изм.	Кол.уч	Лист	Док.	Подпись	Дата	АЛЬФА-60	Стадия	Лист	Листов
Рук.Маст.		Каличкин А.Д.					Р	24	47
ГАП		Пономарев А.А.							
Архитектор		Муратов Р.Р.				Обмерный план			

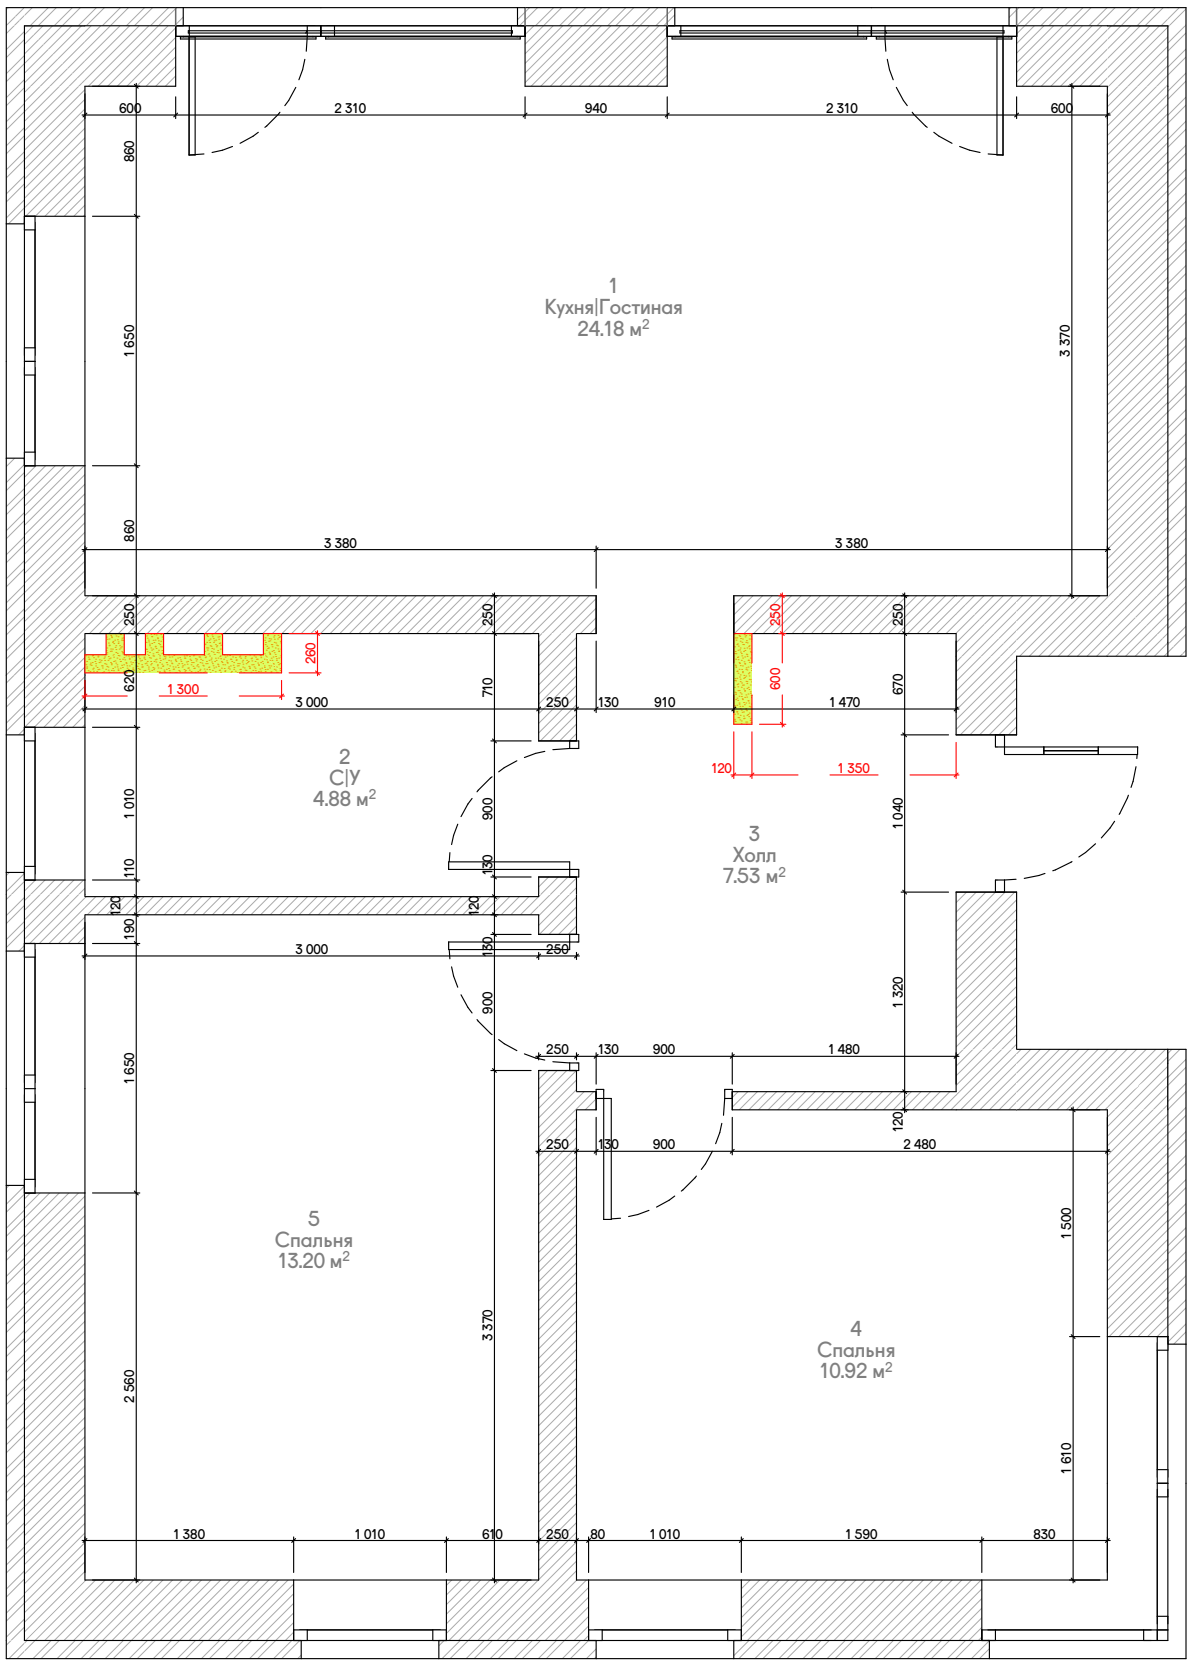

*Размеры указаны на основании рабочей документации, перед началом работ выполнить обмеры фактической геометрии


Изм.	Кол.уч	Лист	Док.	Подпись	Дата	АЛЬФА-60	Стадия	Лист	Листов
Рук.Маст.		Каличкин А.Д.					Р	25	47
ГАП		Пономарев А.А.							
Архитектор		Муратов Р.Р.				План демонтажа			

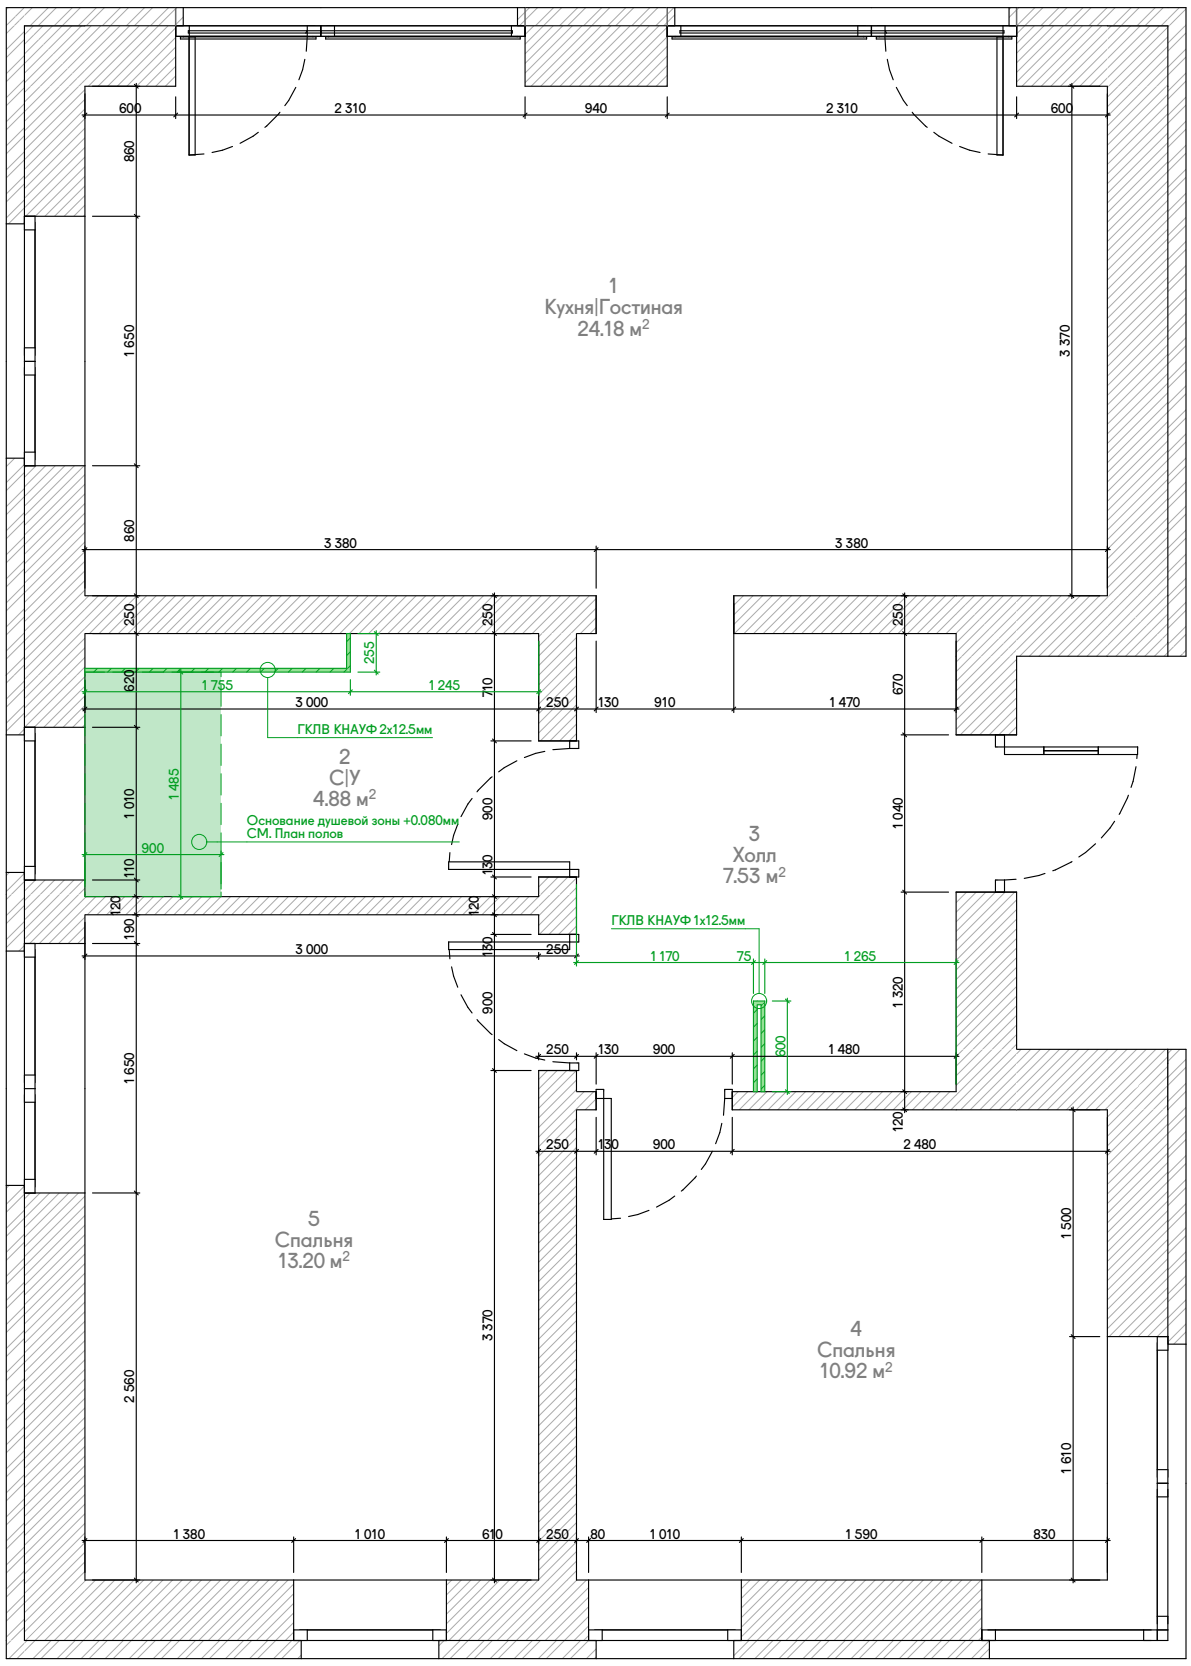

Монтаж стен	
Наименование	Площадь [м2]
ГКЛВ Кнауф 12.5	13.15

*Размеры указаны на основании рабочей документации, перед началом работ выполнить обмеры фактической геометрии


Изм.	Кол.уч	Лист	Док.	Подпись	Дата	АЛЬФА-60	Стадия	Лист	Листов
Рук.Маст.		Каличкин А.Д.					Р	26	47
ГАП		Пономарев А.А.							
Архитектор		Муратов Р.Р.				План монтажа			

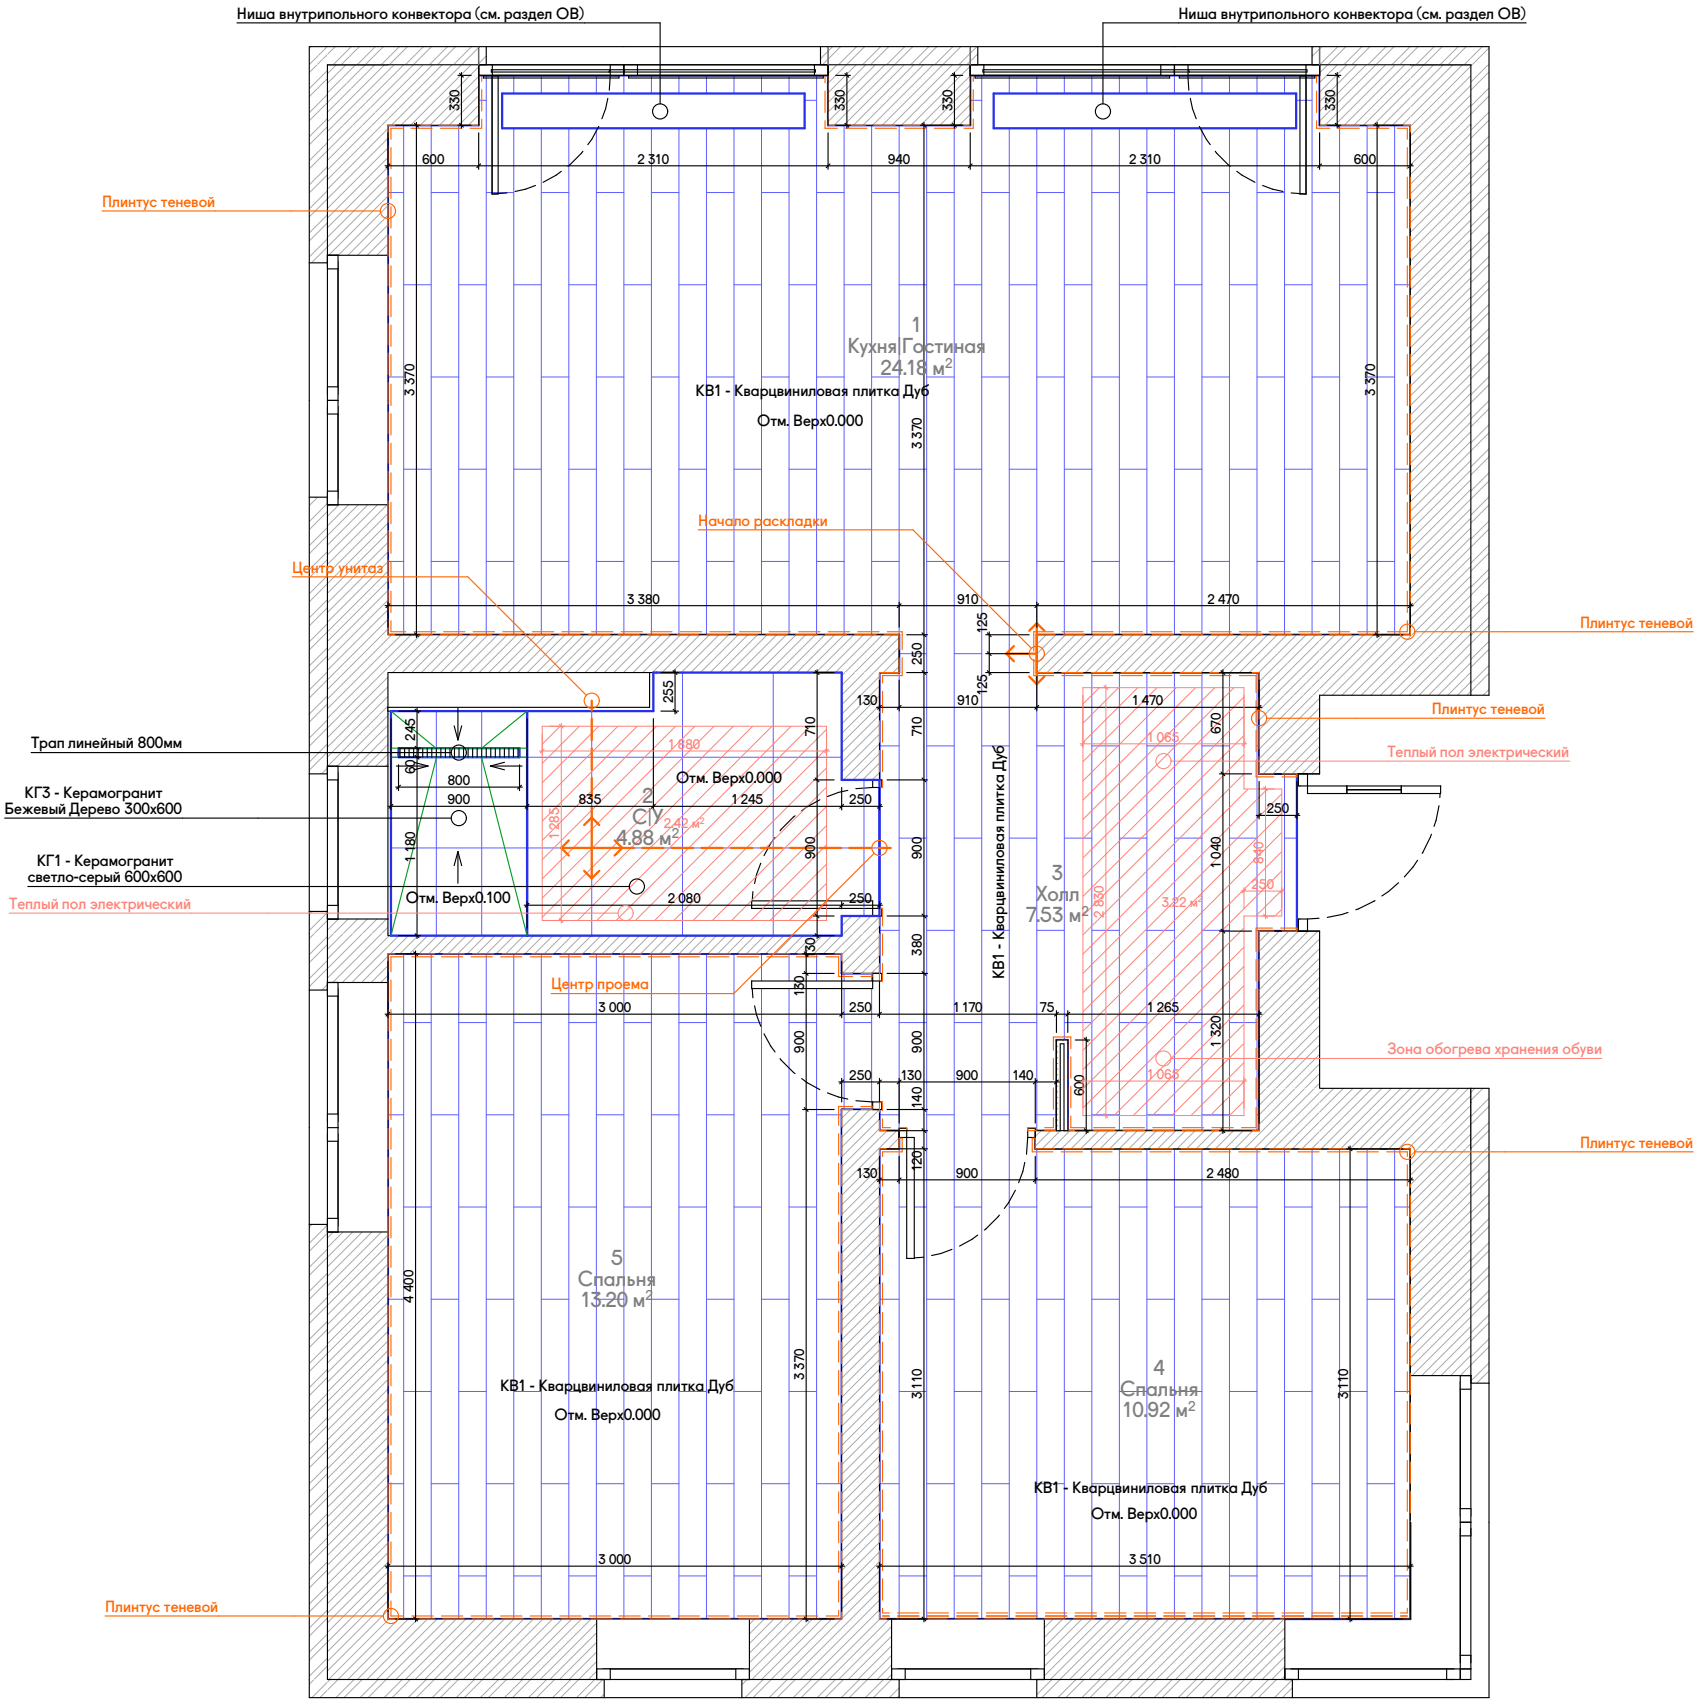

Финишные покрытия пола	
Наименование	Учитываемая Площадь [м2]
КВ1" - Кварцвиниловая плитка Дуб	53.30
КГ1" - Керамогранит светло-серый 600х600	3.50
КГ3" - Керамогранит Бежевый Дерево 300х600	1.26

Плинтус напольный	
Наименование	Длина (мм)
Плинтус теневой напольный	55 369.1

Изм.	Кол.уч	Лист	Док.	Подпись	Дата	АЛЬФА-60	Стадия	Лист	Листов
Рук.Маст.		Каличкин А.Д.					Р	29	47
ГАП		Пономарев А.А.							
Архитектор		Муратов Р.Р.				План покрытий пола			

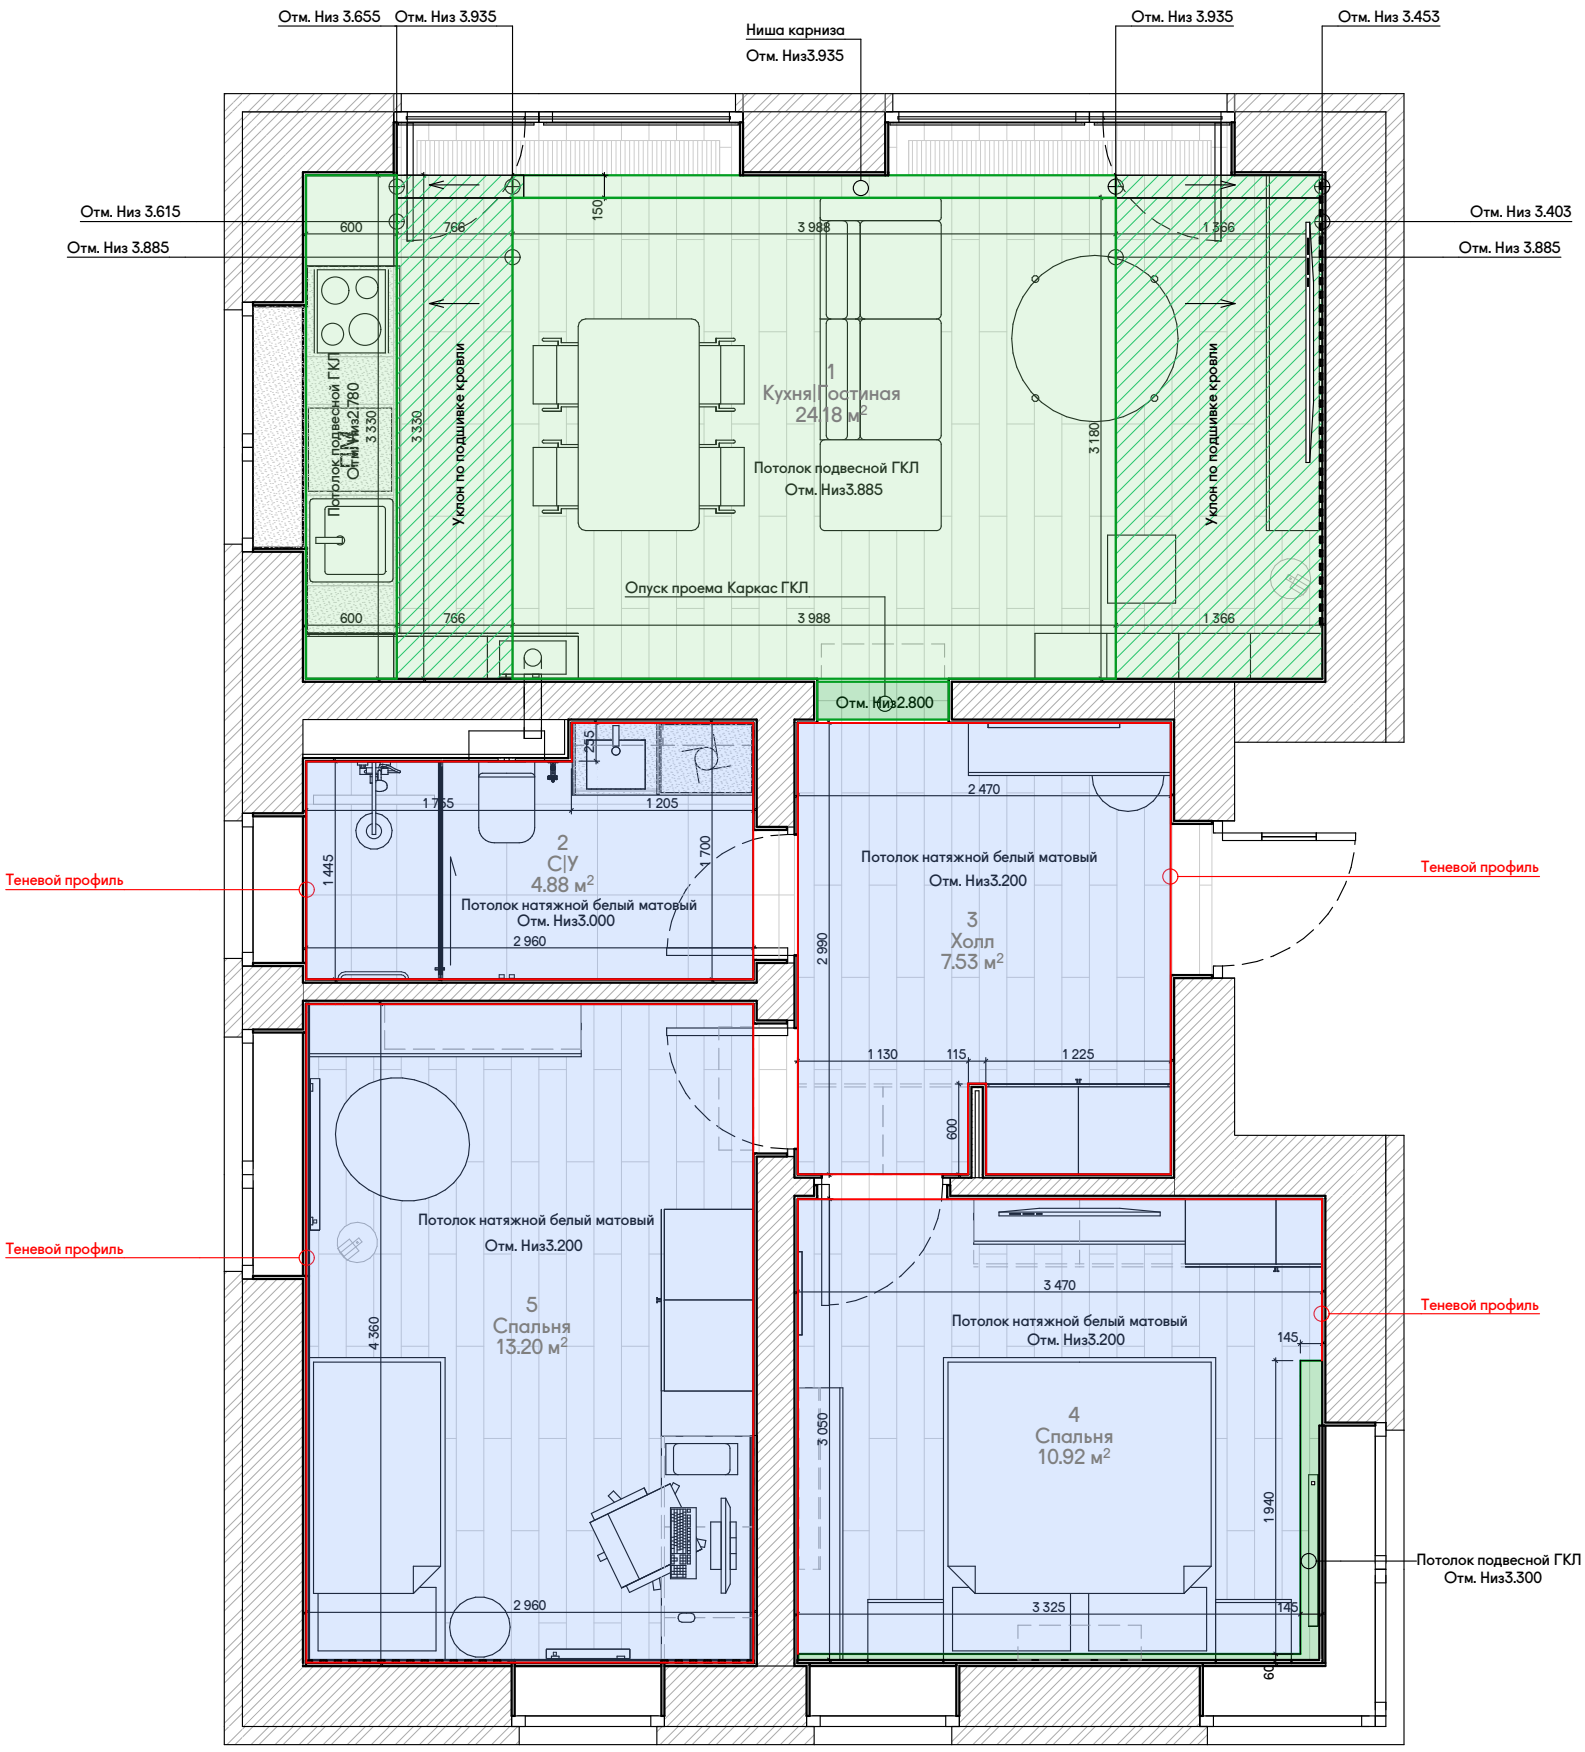

Потолки	
Наименование	Учитываемая Площадь [м2]
КР1* - Краска Белая Матовая	32.87
НП1* - Натяжной потолок Белый Матовый	34.03

Подготовка потолок	
Наименование	Площадь [м2]
ГКЛВ Кнауф 12.5	18.79

*Размеры даны для справки, утвердить отметки потолков после обмеров фактической геометрии

Профиль потолочный	
Наименование	Длина (мм)
Профиль теневой потолочный	43 489.2

Изм.	Кол.уч	Лист	Док.	Подпись	Дата	АЛЬФА-60	Стадия	Лист	Листов
Рук.Маст.		Каличкин А.Д.					Р	31	47
ГАП		Пономарев А.А.							
Архитектор		Муратов Р.Р.				План потолков			


Подготовка поверхностей|материалы		
Наименование	Примечание	Площадь [м2]
Выравнивание стен под покраску (ГКЛ/Штукатурка)	Выбор выравнивания стен на усмотрение подрядчика	172.09
ГКЛВ Кнауф 12.5	или аналог	32.04
Керамогранит		27.89
Панели ЛДСП	или аналог	11.01

Основные отделочные материалы			
Наименование в проекте	Внешний вид	Наименование подбор	Учитываемая Площадь [м2]
КВ1* - Кварцвиниловая плитка Дуб		ABA плитка Atrium Дуб Артисан класс 33 с фаской толщина 5 мм 182х1220мм	53.30
КГ1* - Керамогранит светло-серый 600х600		Kerama Marazzi Про Дабл DD601520R бежевый светлый обрезной 600х600х9мм	17.21
КГ2*- Керамогранит Бежевый Дерево Узор 300х600		Kerama Marazzi Про Дабл OS\C317\11236R Декор чипсет бежевый матовый обрезной 30х60х0,9	11.17
КГ3* - Керамогранит Бежевый Дерево 300х600		Kerama Marazzi Про Дабл 11236R бежевый матовый обрезной 300х600х9мм	2.87
КР1* - Краска Белая Матовая		Tikkurila Euro Smart 2 Белый или аналог	205.08
КР2* - Краска Антрацит Матовая		Tikkurila Euro Smart 2 Y499 или аналог	11.53
ЛП1* - ЛДСП Панель Дуб светлый		Egger H3165 ST12 Дуб Виченца светлый	11.26
НП1* - Натяжной потолок Белый Матовый		Белый матовый	34.03

Плинтус напольный подбор			
Наименование в проекте	Внешний вид	Наименование подбор	Длина (мм)
Плинтус теневой напольный		Плинтус с теневым зазором (комплектный с дверями) Tenevoy.ru	55 369.1


Профиль потолочный подбор			
Наименование в проекте	Внешний вид	Наименование подбор	Длина (мм)
Профиль теневой потолочный		EUROKRAAB теневой профиль для натяжных потолков	43 489.2

Изм.	Кол.уч	Лист	Док.	Подпись	Дата	АЛЬФА-60	Стадия	Лист	Листов
Рук.Маст.		Каличкин А.Д.					Р	32	47
ГАП		Пономарев А.А.							
Архитектор		Муратов Р.Р.				Ведомость основных отделочных материалов			

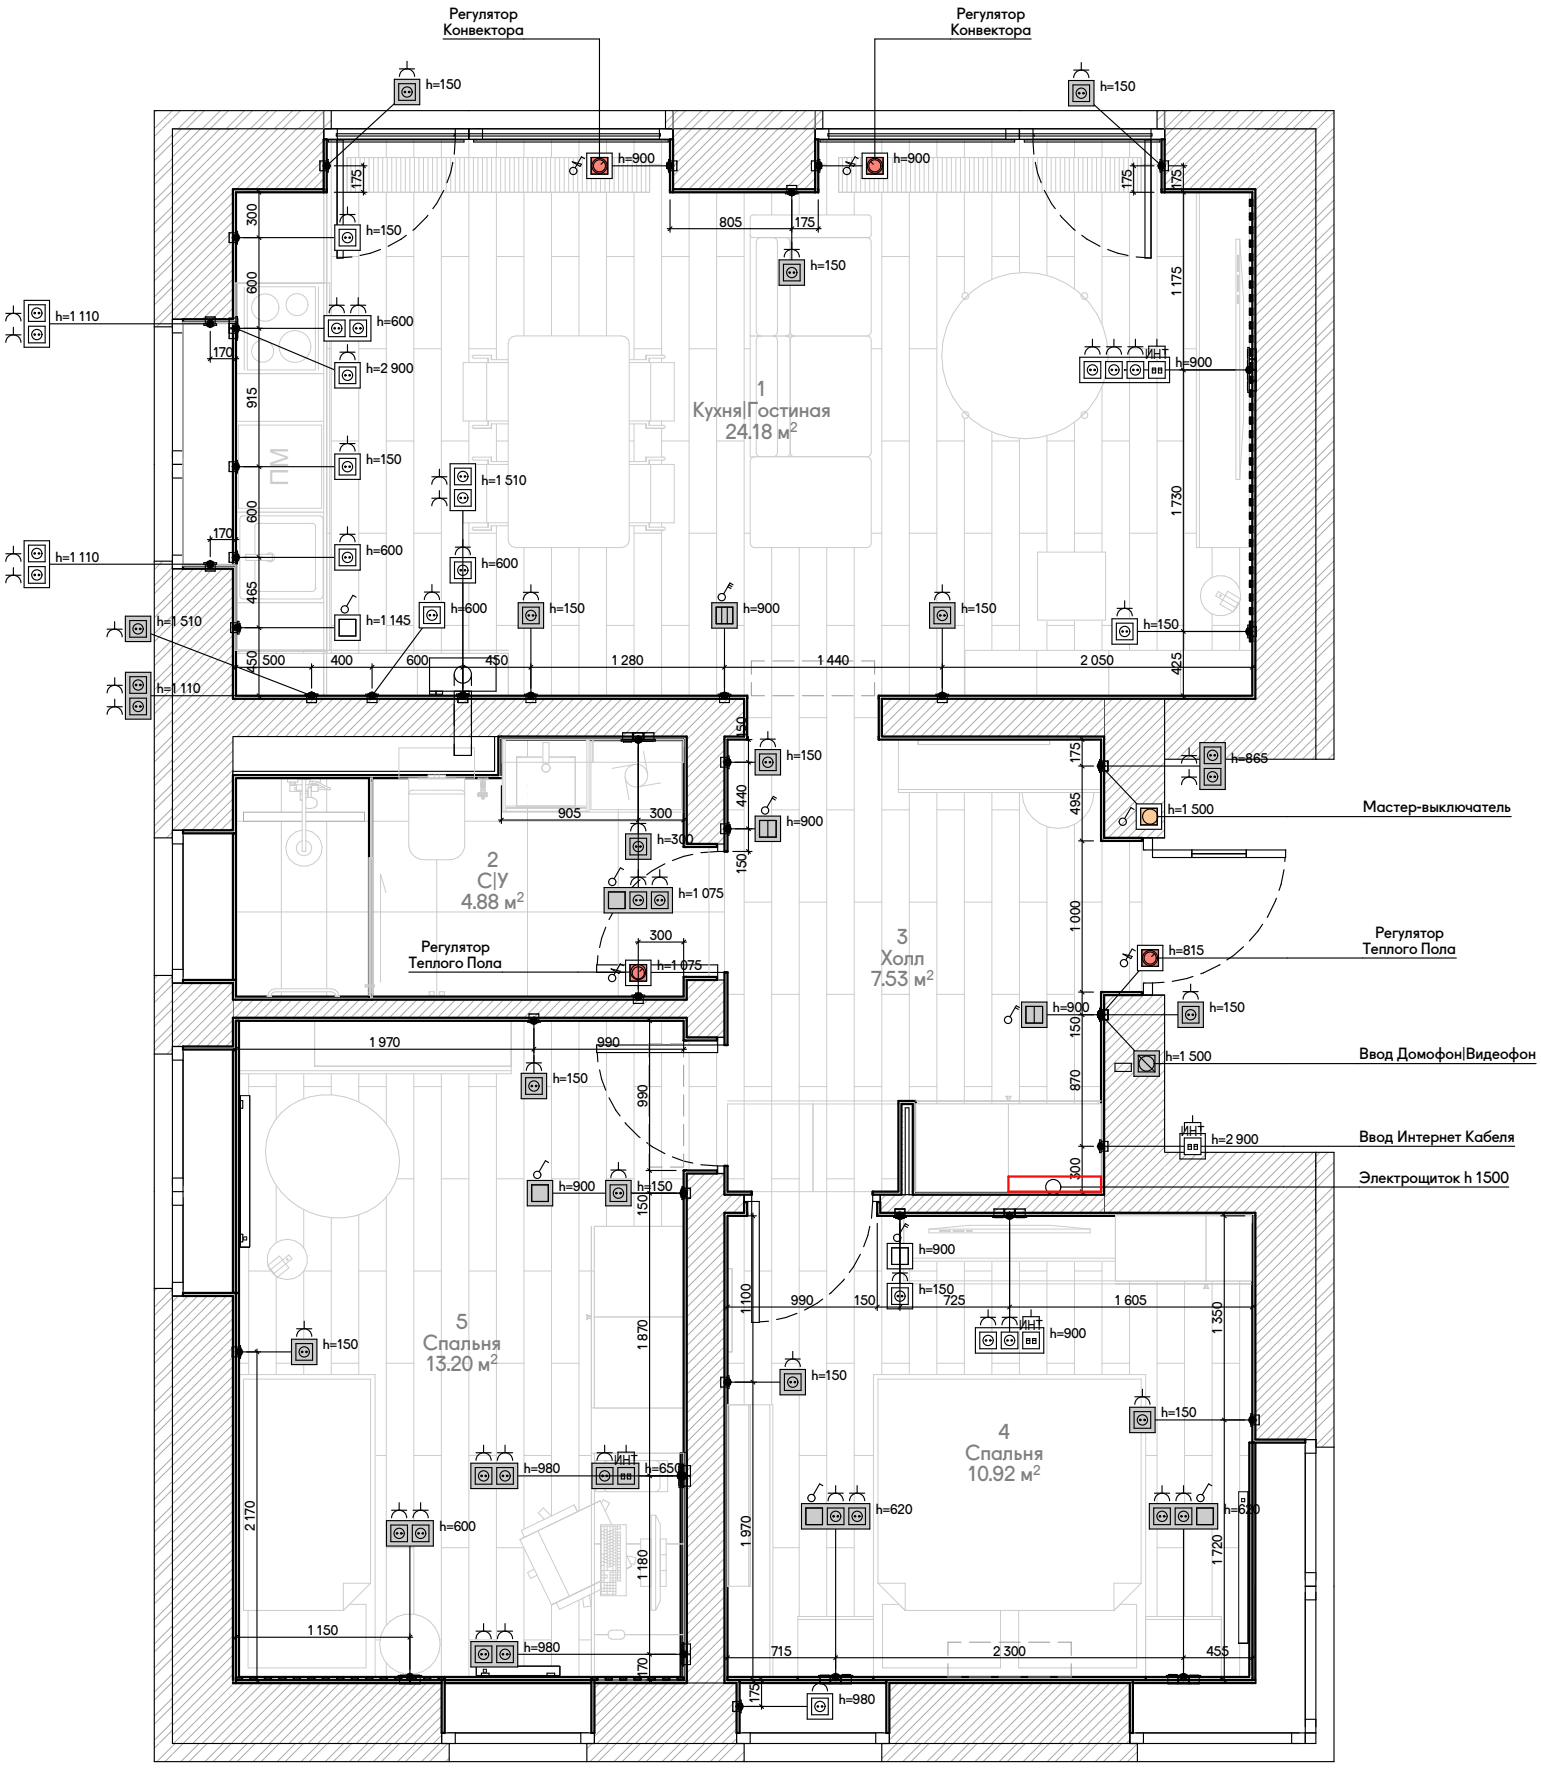


*Выводы питания и наружные выключатели данным проектом не разрабатываются
*Схематичное изображение выключателей и рамок на плане показано лицевой стороной по отношению к смотрящему

Изм.	Кол.уч	Лист	Док.	Подпись	Дата	АЛЬФА-60	Стадия	Лист	Листов
Рук.Маст.		Каличкин А.Д.					Р	35	47
ГАП		Пономарев А.А.							
Архитектор		Муратов Р.Р.				Нижняя разводка электроприборов	А510		

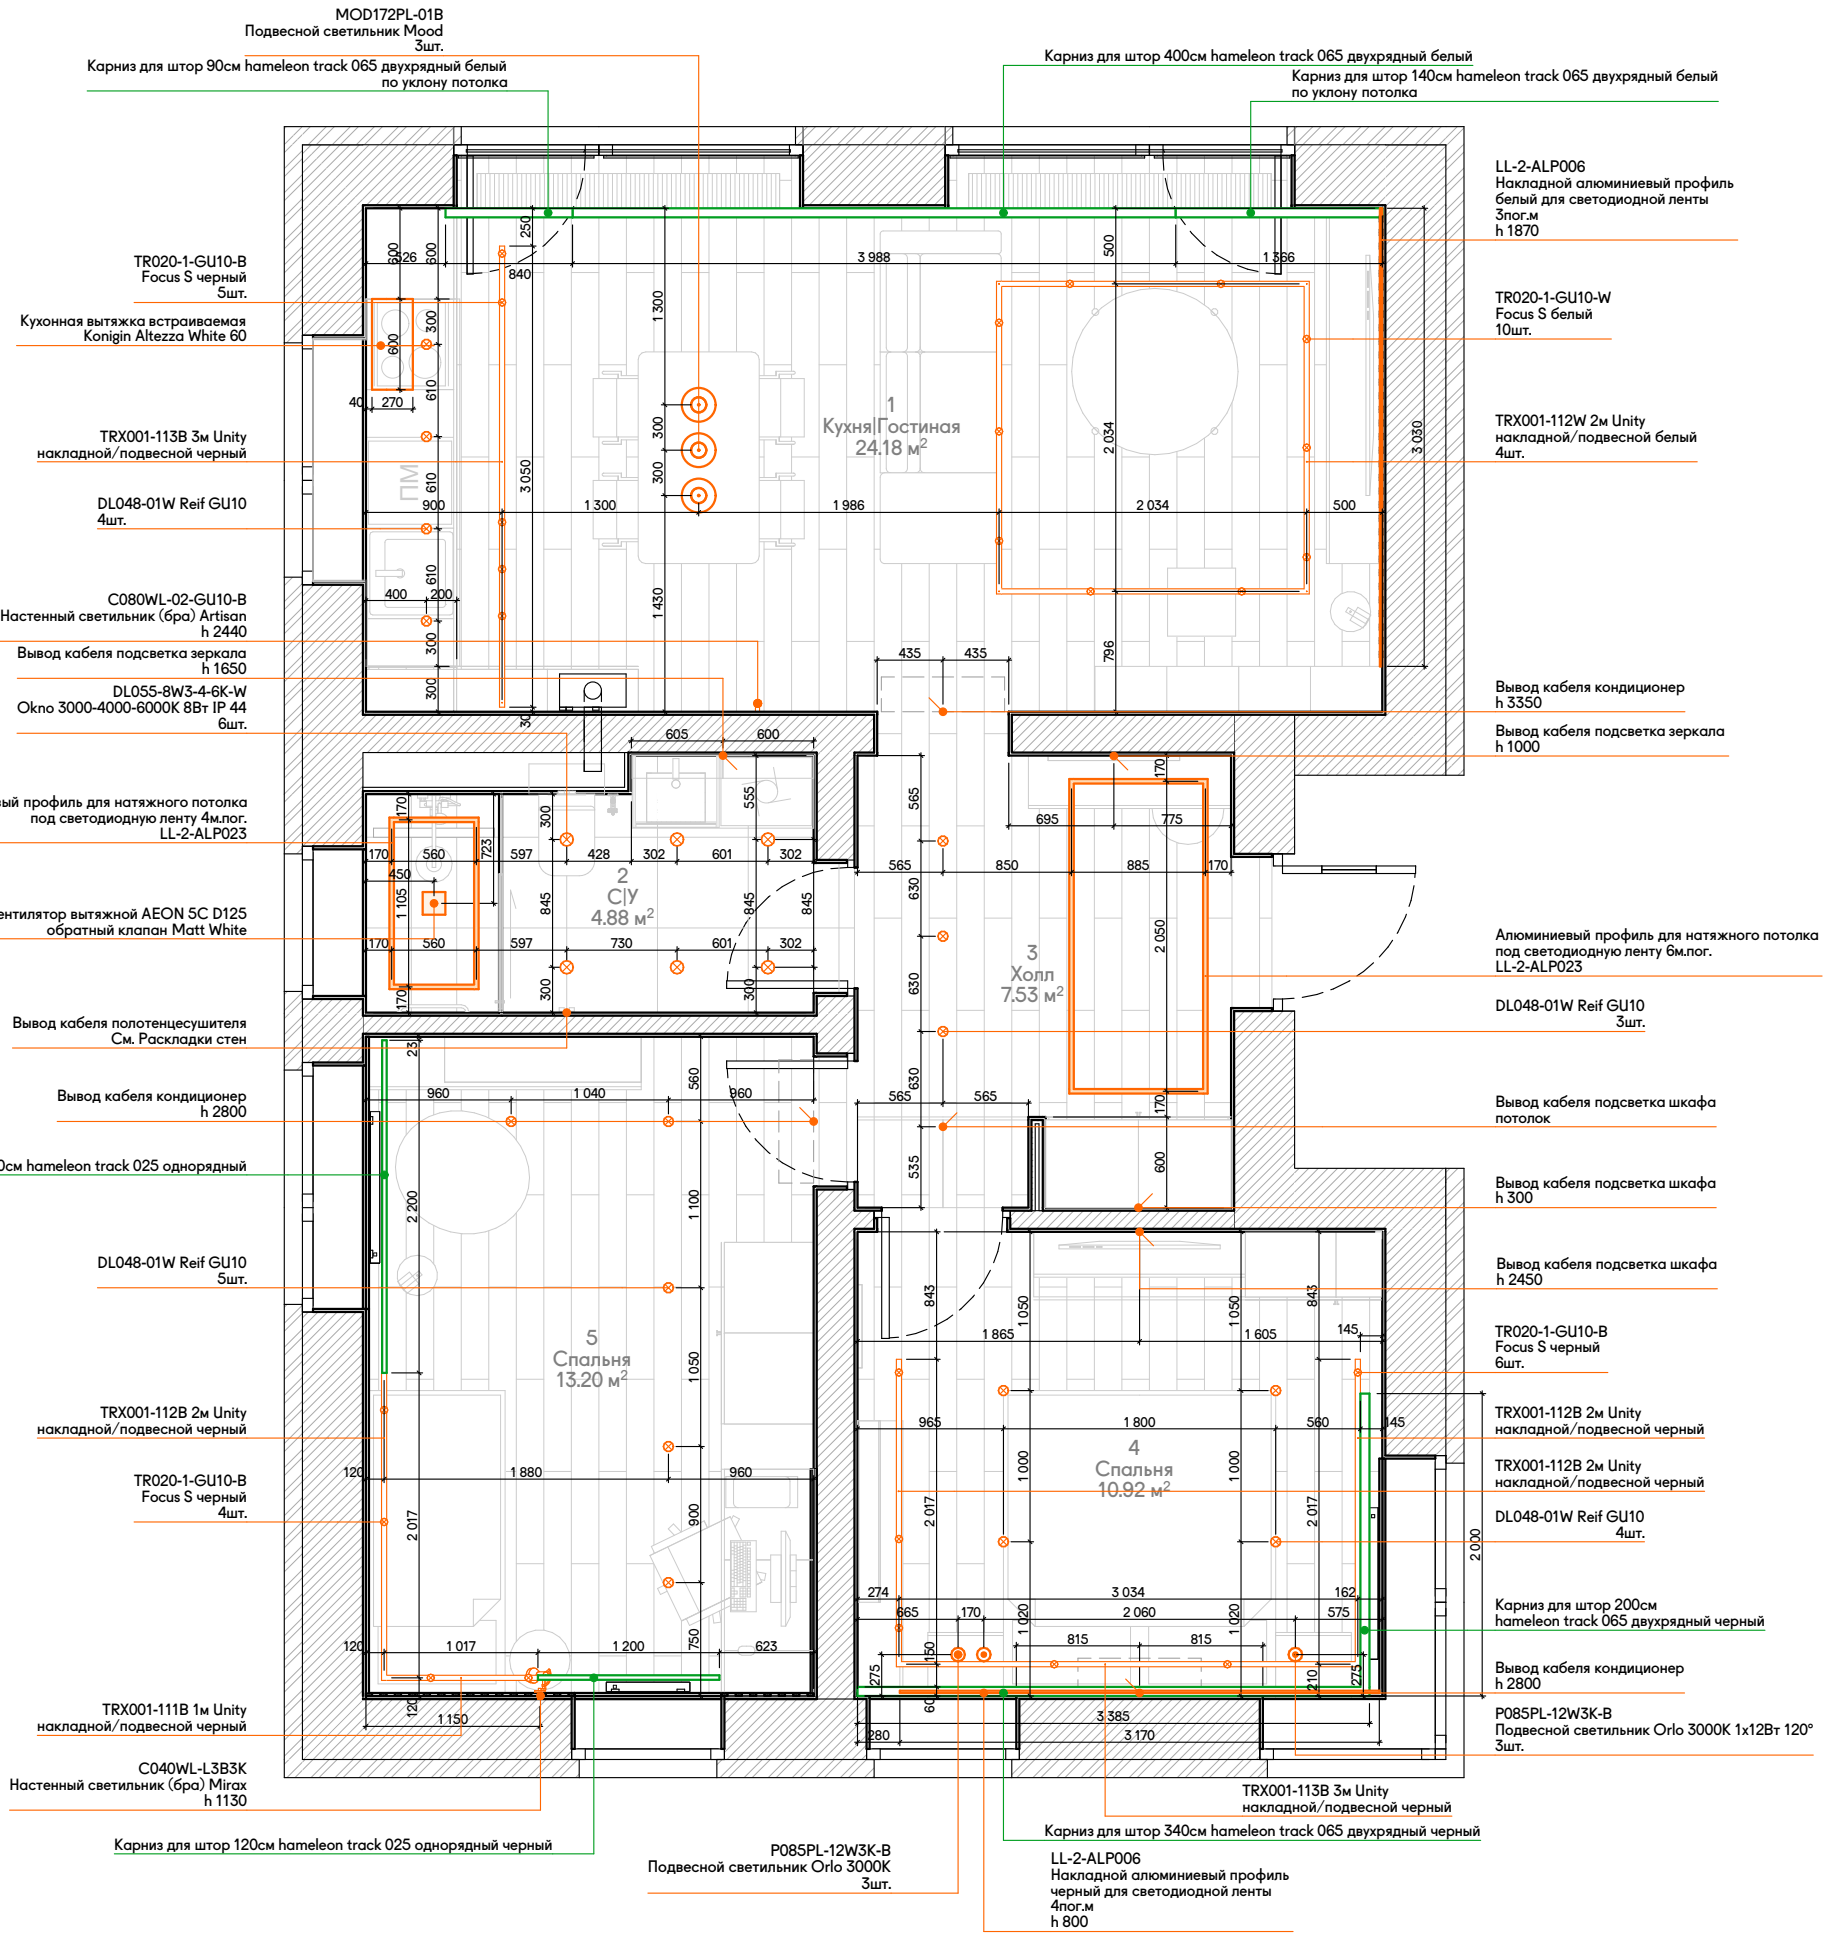


Изм.	Кол.уч	Лист	Док.	Подпись	Дата	АЛЬФА-60	Стадия	Лист	Листов
Рук.Маст.		Каличкин А.Д.					Р	36	47
ГАП		Пономарев А.А.							
Архитектор		Муратов Р.Р.				Верхняя разводка электроприборов			

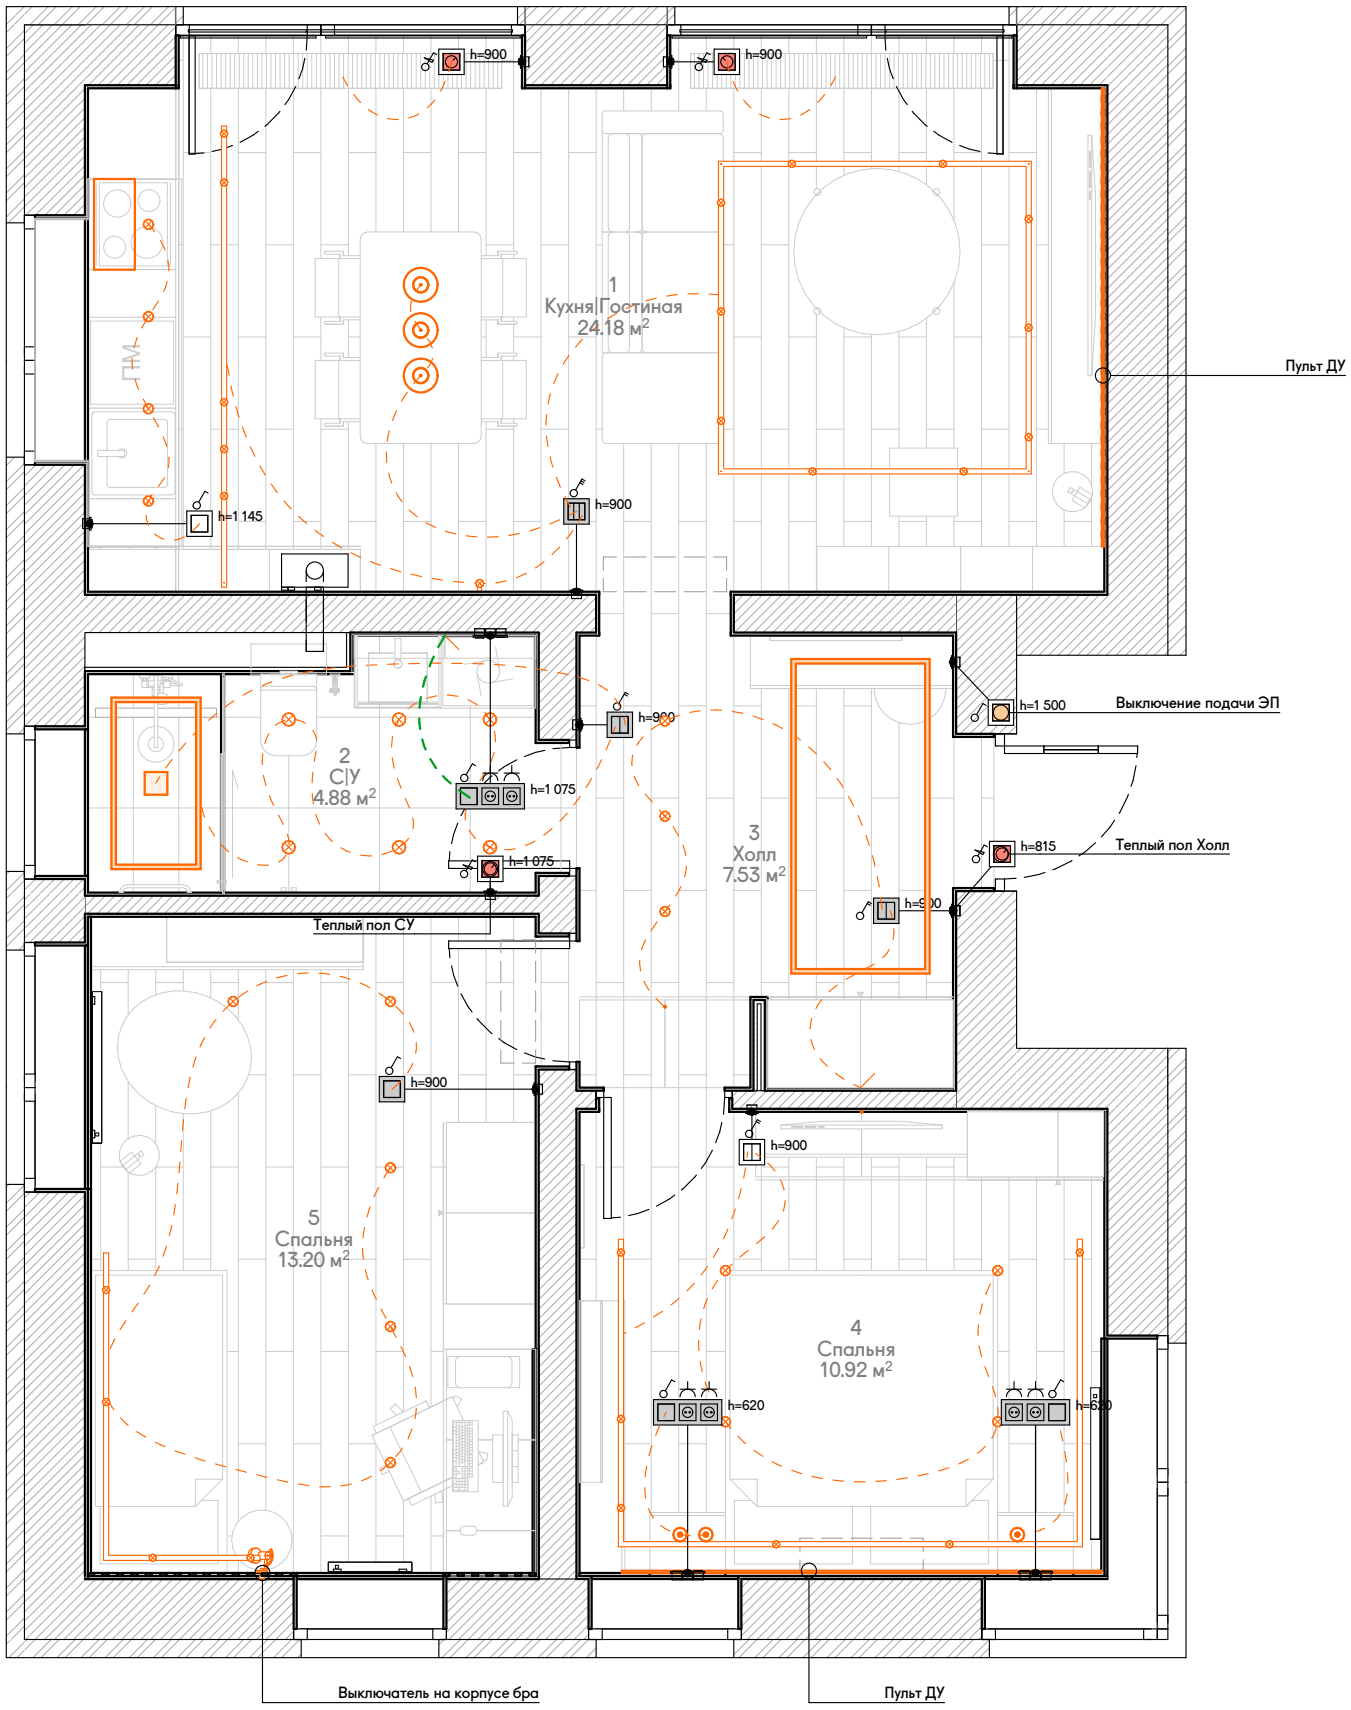


*Схематичное изображение выключателей и рамок на плане показано лицевой стороной по отношению к смотрящему

Изм.	Кол.уч	Лист	Док.	Подпись	Дата	АЛЬФА-60	Стадия	Лист	Листов
Рук.Маст.		Каличкин А.Д.					Р	37	47
ГАП		Пономарев А.А.							
Архитектор		Муратов Р.Р.				Схема управления электроприборами	A510		

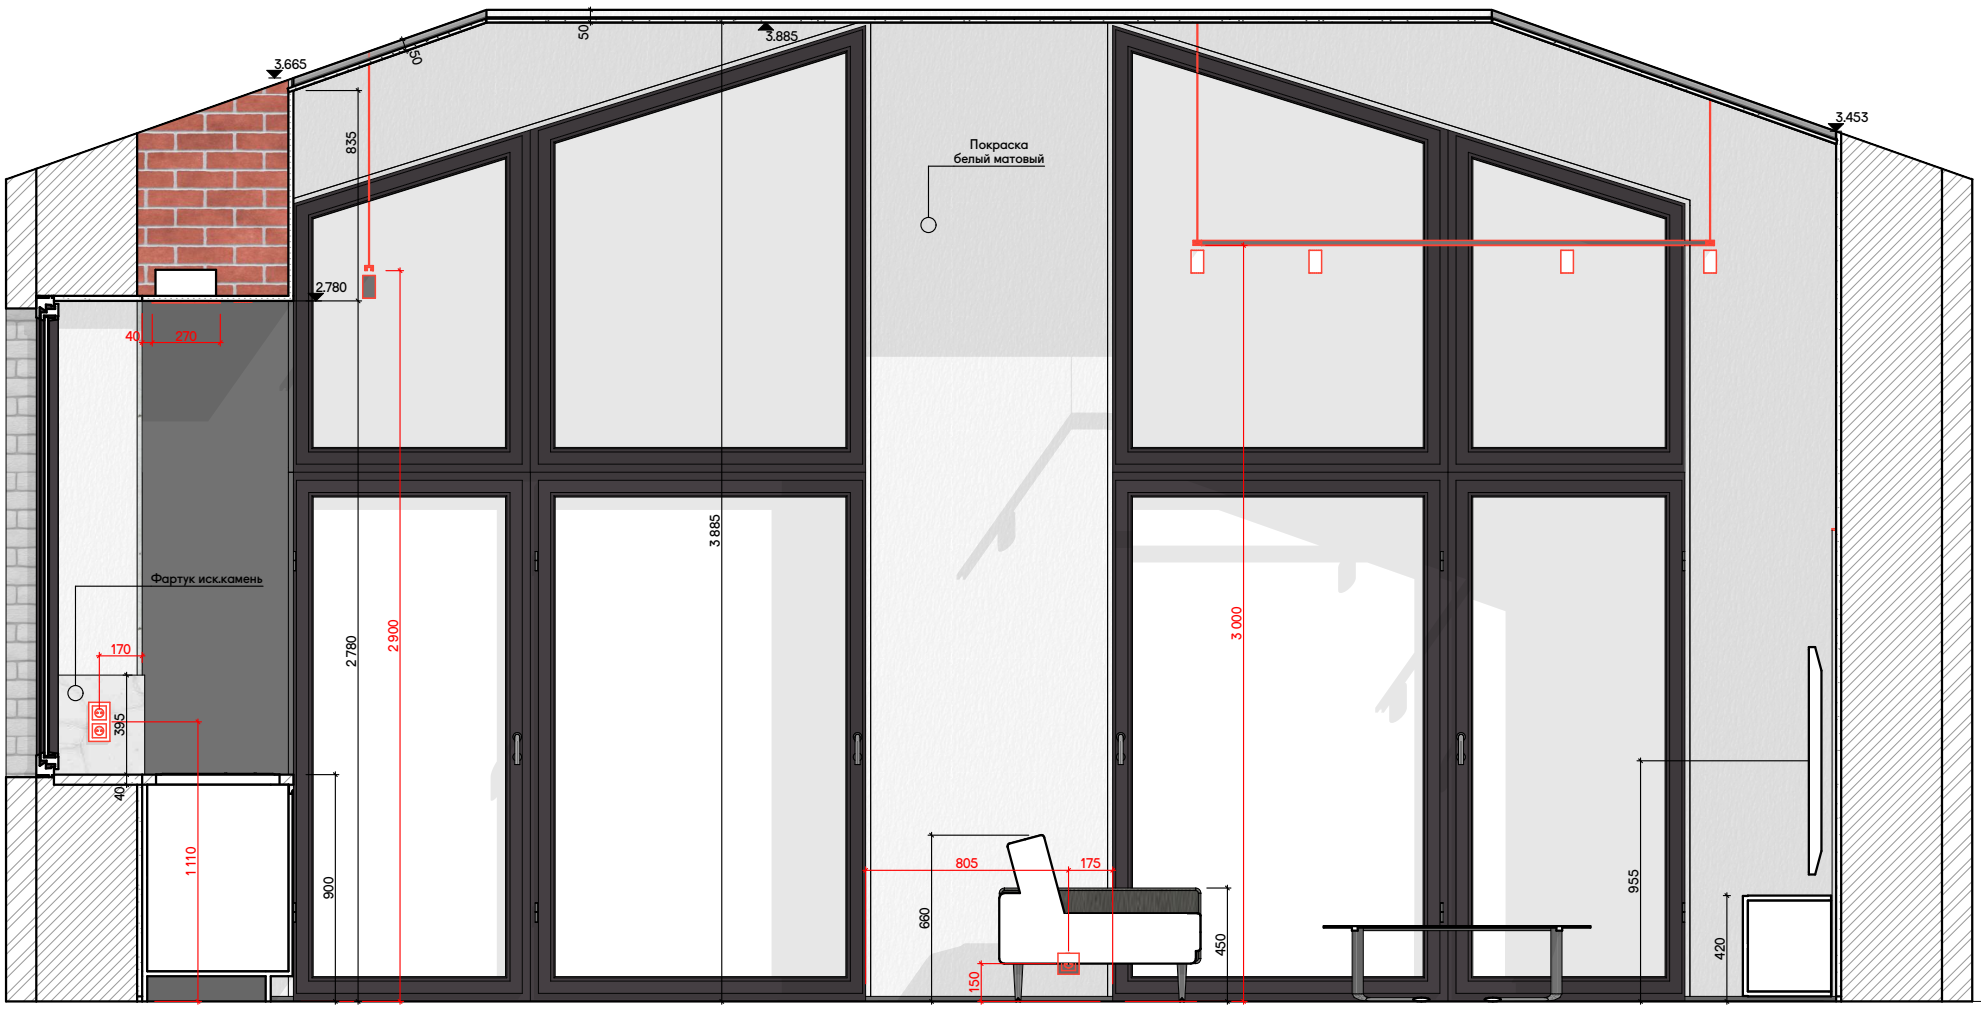


1 Кухня|Гостиная С 1:30

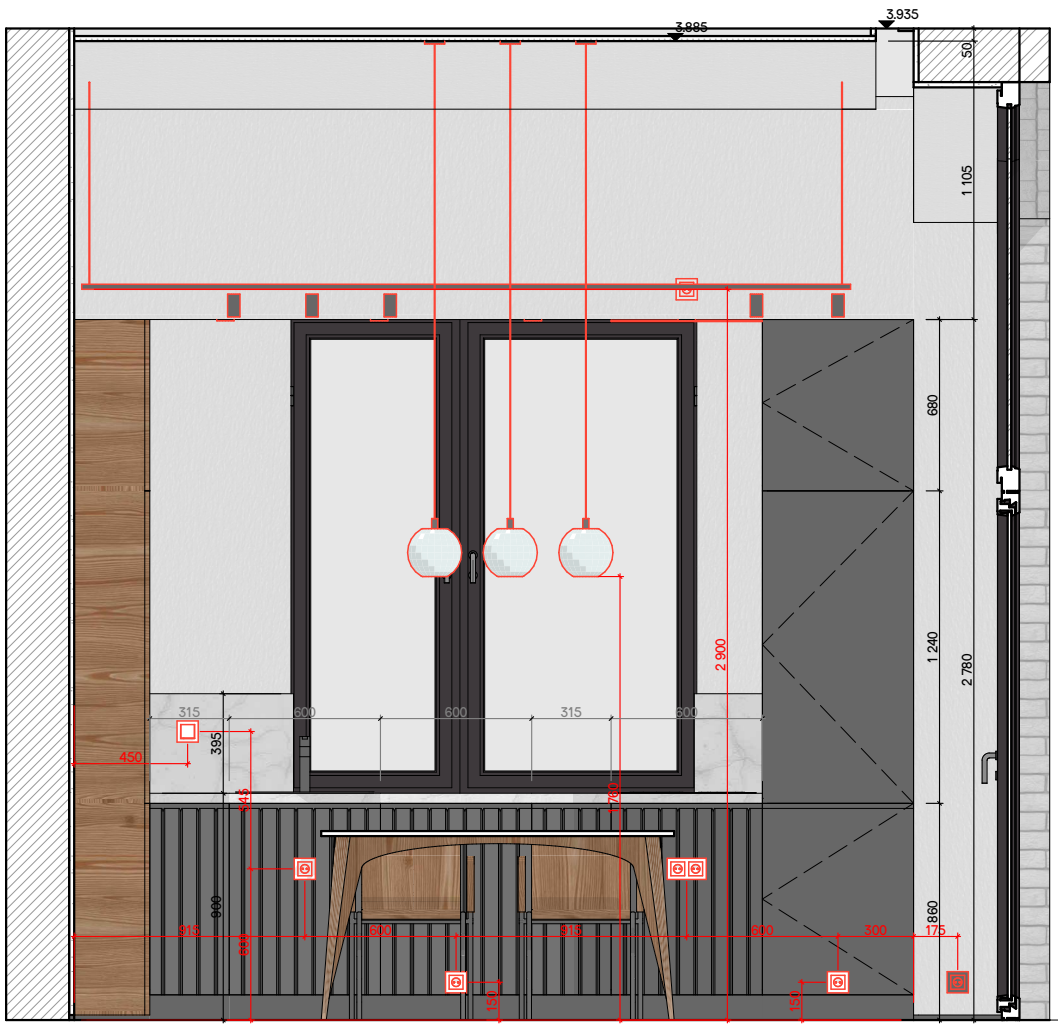


1 Кухня|Гостиная З 1:30


Изм.	Кол.уч	Лист	Док.	Подпись	Дата	АЛЬФА-60	Стадия	Лист	Листов
Рук.Маст.		Каличкин А.Д.					Р	40	47
ГАП		Пономарев А.А.							
Архитектор		Муратов Р.Р.				Кухня|Гостиная раскладки С З			

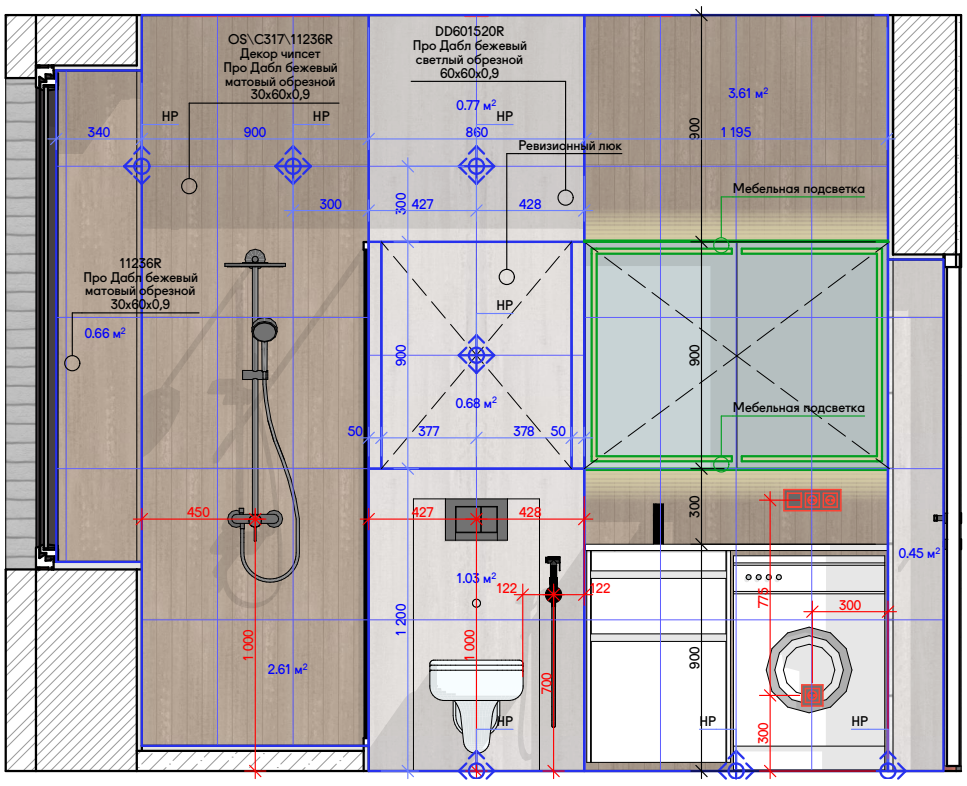


2 С|У С 1:30

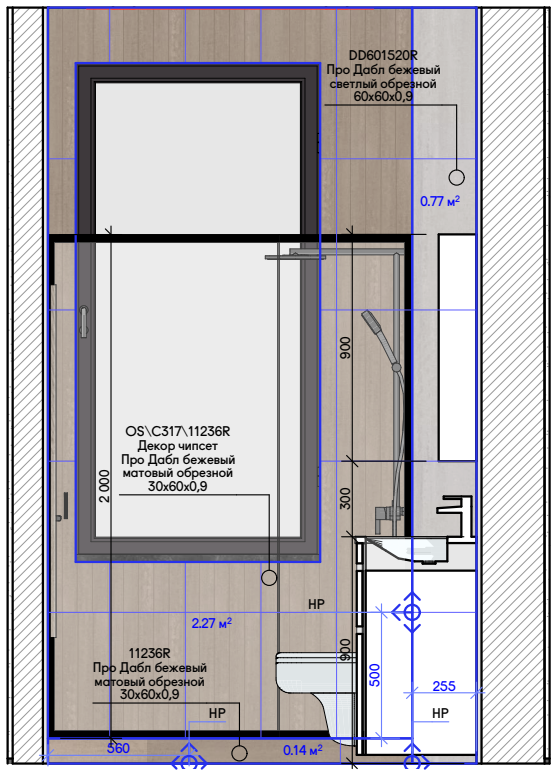

2 С|У З 1:30

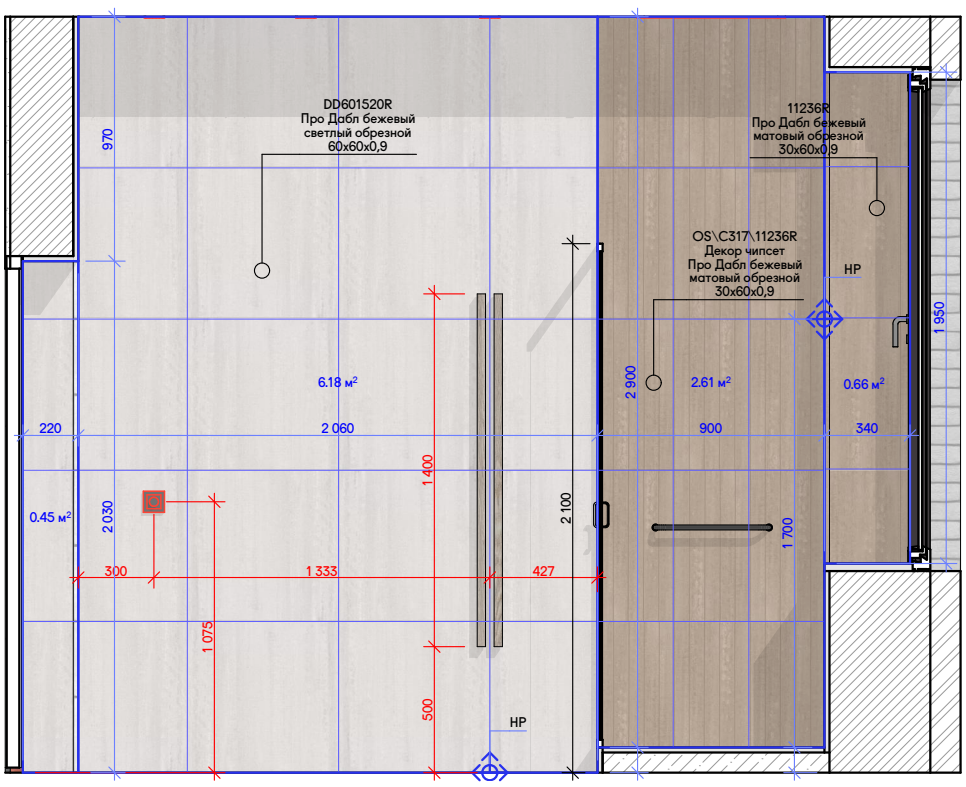

2 С|У Ю 1:30

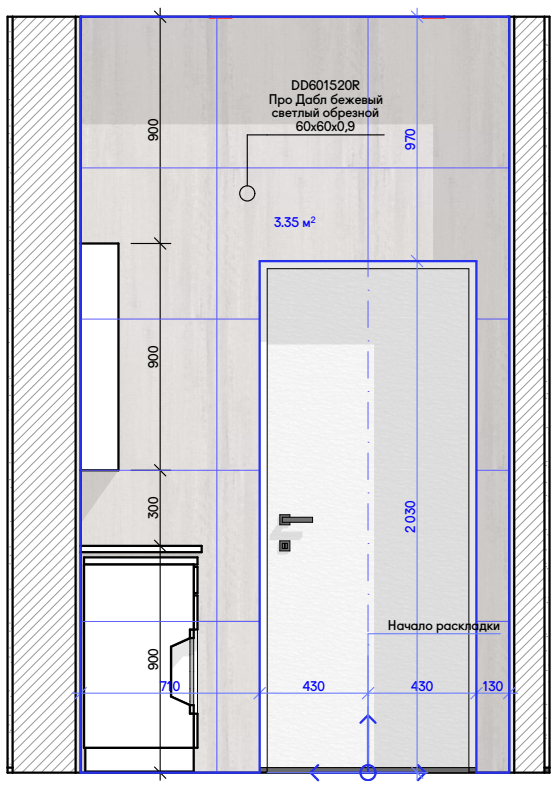

2 С|У В 1:30

Изм.	Кол.уч	Лист	Док.	Подпись	Дата	АЛЬФА-60	Стадия	Лист	Листов
Рук.Маст.		Каличкин А.Д.					Р	42	47
ГАП		Пономарев А.А.							
Архитектор		Муратов Р.Р.				С\У С З В Ю			