АРХИТЕКТУРНОЕ БЮРО А510

ЖК RIGA HOLIDAY

ОРИОН 180 (D7)
ДИЗАЙН-ПРОЕКТ

ИЮЛЬ 2025

АРХИТЕКТУРНОЕ БЮРО А510
INFO@A510.ru
+7 (495) 532-70-54
www.A510.space | www.A510.ru

СОСТАВ ПРОЕКТА

1	Титульный лист	31	5СУ 1	61	11Спальня 7	91	План монтажа 2	121	Холл С 3
2	Состав проекта	32	5СУ 2	62	12СУ 1	92	План заполнения проемов	122	Холл Ю В
3	Гостиная 1	33	5СУ 3	63	12СУ 2	93	План заполнения проемов 2	123	Кабинет С 3
4	Гостиная 2	34	5СУ 4	64	12СУ 3	94	Ведомость дверей	124	Кабинет Ю В
5	Гостиная 3	35	Котельная 1	65	12СУ 4	95	План покрытий пола	125	5СУ
6	Гостиная 4	36	Котельная 2	66	12СУ 5	96	План покрытий пола 2	126	Котельная С 3
7	Гостиная 5	37	Котельная 3	67	13Спальня 1	97	План финишных покрытий стен	127	Котельная Ю В
8	Гостиная 6	38	Холл Второй этаж 1	68	13Спальня 2	98	План финишных покрытий стен 2	128	Холл Второй этаж С 3
9	Гостиная 7	39	Холл Второй этаж 2	69	13Спальня 3	99	План потолков	129	Холл Второй этаж Ю В
10	Гостиная 8	40	Холл Второй этаж 3	70	13Спальня 4	100	План потолков 2	130	Мастер-спальня С 3
11	Гостиная 9	41	Холл Второй этаж 4	71	13Спальня 5	101	Ведомость основных отделочных материалов	131	Мастер-спальня Ю В
12	Гостиная 10	42	Холл Второй этаж 5	72	13Спальня 6	102	План монтажа оборудования	132	9СУ
13	Гостиная 11	43	Холл Второй этаж 6	73	13Спальня 7	103	План монтажа оборудования 2	133	Гардероб
14	Гостиная 12	44	Мастер-спальня 1	74	14Спальня 1	104	Монтажные схемы оборудования	134	11Спальня С 3
15	Гостиная 13	45	Мастер-спальня 2	75	14Спальня 2	105	Принципиальная схема отопления, кондиционирования	135	11Спальня Ю В
16	Прихожая 1	46	Мастер-спальня 3	76	14Спальня 3	106	Принципиальная схема отопления, кондиционирования 2	136	12СУ
17	Прихожая 2	47	Мастер-спальня 4	77	14Спальня 4	107	Нижняя разводка электроприборов	137	13Спальня С 3
18	Прихожая 3	48	Мастер-спальня 5	78	14Спальня 5	108	Нижняя разводка электроприборов 2	138	13Спальня Ю В
19	Прихожая 4	49	9СУ 1	79	14Спальня 6	109	Верхняя разводка электроприборов	139	14Спальня С 3
20	Холл 1	50	9СУ 2	80	14Спальня 7	110	Верхняя разводка электроприборов 2	140	14Спальня Ю В
21	Холл 2	51	9СУ 3	81	15СУ 1	111	Схема управления электроприборами	141	15 СУ
22	Холл 3	52	9СУ 4	82	15СУ 2	112	Схема управления электроприборами 2		
23	Холл 4	53	Гардероб 1	83	15СУ 3	113	Ведомость верхней и нижней разводки электроприборов 1 этажа		
24	Холл 5	54	Гардероб 2	84	15СУ 4	114	Ведомость верхней и нижней разводки электроприборов 2 этажа		
25	Холл 6	55	11Спальня 1	85	Общая планировка	115	План раскладок по стенам		
26	Кабинет 1	56	11Спальня 2	86	Общая планировка 2	116	План раскладок по стенам 2		
27	Кабинет 2	57	11Спальня 3	87	Обмерный план	117	Гостиная С 3		
28	Кабинет 3	58	11Спальня 4	88	Обмерный план 2	118	Гостиная Ю В		
29	Кабинет 4	59	11Спальня 5	89	План демонтажа	119	Прихожая С 3		
30	Кабинет 5	60	11Спальня 6	90	План монтажа	120	Прихожая Ю В		

Примечания:
- Комплект чертежей подготовлен на основании рабочей документации предоставленной заказчиком, фактические замеры не проводились
- За отметку +0.000 принят уровень "чистого" пола
- Высотные отметки даны от уровня "чистого" пола
- Финальное утверждения цветов покраски проводится по выкрасам на объекте
- Замеры мебели производятся поставщиком продукции после выполнения чистовой отделки
- Замеры дверных проемов производятся поставщиком продукции после выполнения черновой отделки
- Размеры указаны для справки и при необходимости корректируются по месту, при существенных расхождениях фактических замеров и рабочего проекта
обратиться к разработчику дизайн-проекта для внесения коррективов (выполняется в рамках авторского надзора)

Изм.	Кол.уч	Лист	Док.	Подпись	Дата	ОРИОН-180	Стадия	Лист	Листов
Рук.Маст.		Каличкин А.Д.					Р	2	141
ГАП		Пономарев А.А.							
Архитектор		Муратов Р.Р.				Состав проекта	A510		

АРХИТЕКТУРНОЕ БЮРО А510
INFO@A510.ru
+7 (495) 532-70-54
www.A510.space | www.A510.ru

Изм.	Кол.уч	Лист	Док.	Подпись	Дата	ОРИОН-180	Стадия	Лист	Листов
Рук.Маст.		Каличкин А.Д.					Р	3	141
ГАП		Пономарев А.А.							
Архитектор		Муратов Р.Р.				Гостиная 1	A510		

АРХИТЕКТУРНОЕ БЮРО А510
INFO@A510.ru
+7 (495) 532-70-54
www.A510.space | www.A510.ru

Изм.	Кол.уч	Лист	Док.	Подпись	Дата	ОРИОН-180	Стадия	Лист	Листов
Рук.Маст.		Каличкин А.Д.					Р	8	141
ГАП		Пономарев А.А.							
Архитектор		Муратов Р.Р.				Гостиная 6	A510		

АРХИТЕКТУРНОЕ БЮРО А510
+7 (495) 532-70-54
INFO@A510.ru
www.A510.space | www.A510.ru

Изм.	Кол.уч	Лист	Док.	Подпись	Дата	ОРИОН-180	Стадия	Лист	Листов
Рук.Маст.		Каличкин А.Д.					Р	16	141
ГАП		Пономарев А.А.							
Архитектор		Муратов Р.Р.				Прихожая 1	A510		

АРХИТЕКТУРНОЕ БЮРО А510
+7 (495) 532-70-54
INFO@A510.ru
www.A510.space | www.A510.ru

Изм.	Кол.уч	Лист	Док.	Подпись	Дата	ОРИОН-180	Стадия	Лист	Листов
Рук.Маст.		Каличкин А.Д.					Р	26	141
ГАП		Пономарев А.А.							
Архитектор		Муратов Р.Р.				Кабинет 1	A510		

АРХИТЕКТУРНОЕ БЮРО А510
INFO@A510.ru
+7 (495) 532-70-54
www.A510.space | www.A510.ru

Изм.	Кол.уч	Лист	Док.	Подпись	Дата	ОРИОН-180	Стадия	Лист	Листов
Рук.Маст.		Каличкин А.Д.					Р	44	141
ГАП		Пономарев А.А.							
Архитектор		Муратов Р.Р.				Мастер-спальня 1	A510		

АРХИТЕКТУРНОЕ БЮРО А510
INFO@A510.ru
+7 (495) 532-70-54
www.A510.space | www.A510.ru

Изм.	Кол.уч	Лист	Док.	Подпись	Дата	ОРИОН-180	Стадия	Лист	Листов
Рук.Маст.		Каличкин А.Д.					Р	54	141
ГАП		Пономарев А.А.							
Архитектор		Муратов Р.Р.				Гардероб 2			

АРХИТЕКТУРНОЕ БЮРО А510
INFO@A510.ru
+7 (495) 532-70-54
www.A510.space | www.A510.ru

Изм.	Кол.уч	Лист	Док.	Подпись	Дата	ОРИОН-180	Стадия	Лист	Листов
Рук.Маст.		Каличкин А.Д.					Р	84	141
ГАП		Пономарев А.А.							
Архитектор		Муратов Р.Р.				15СУ 4	A510		

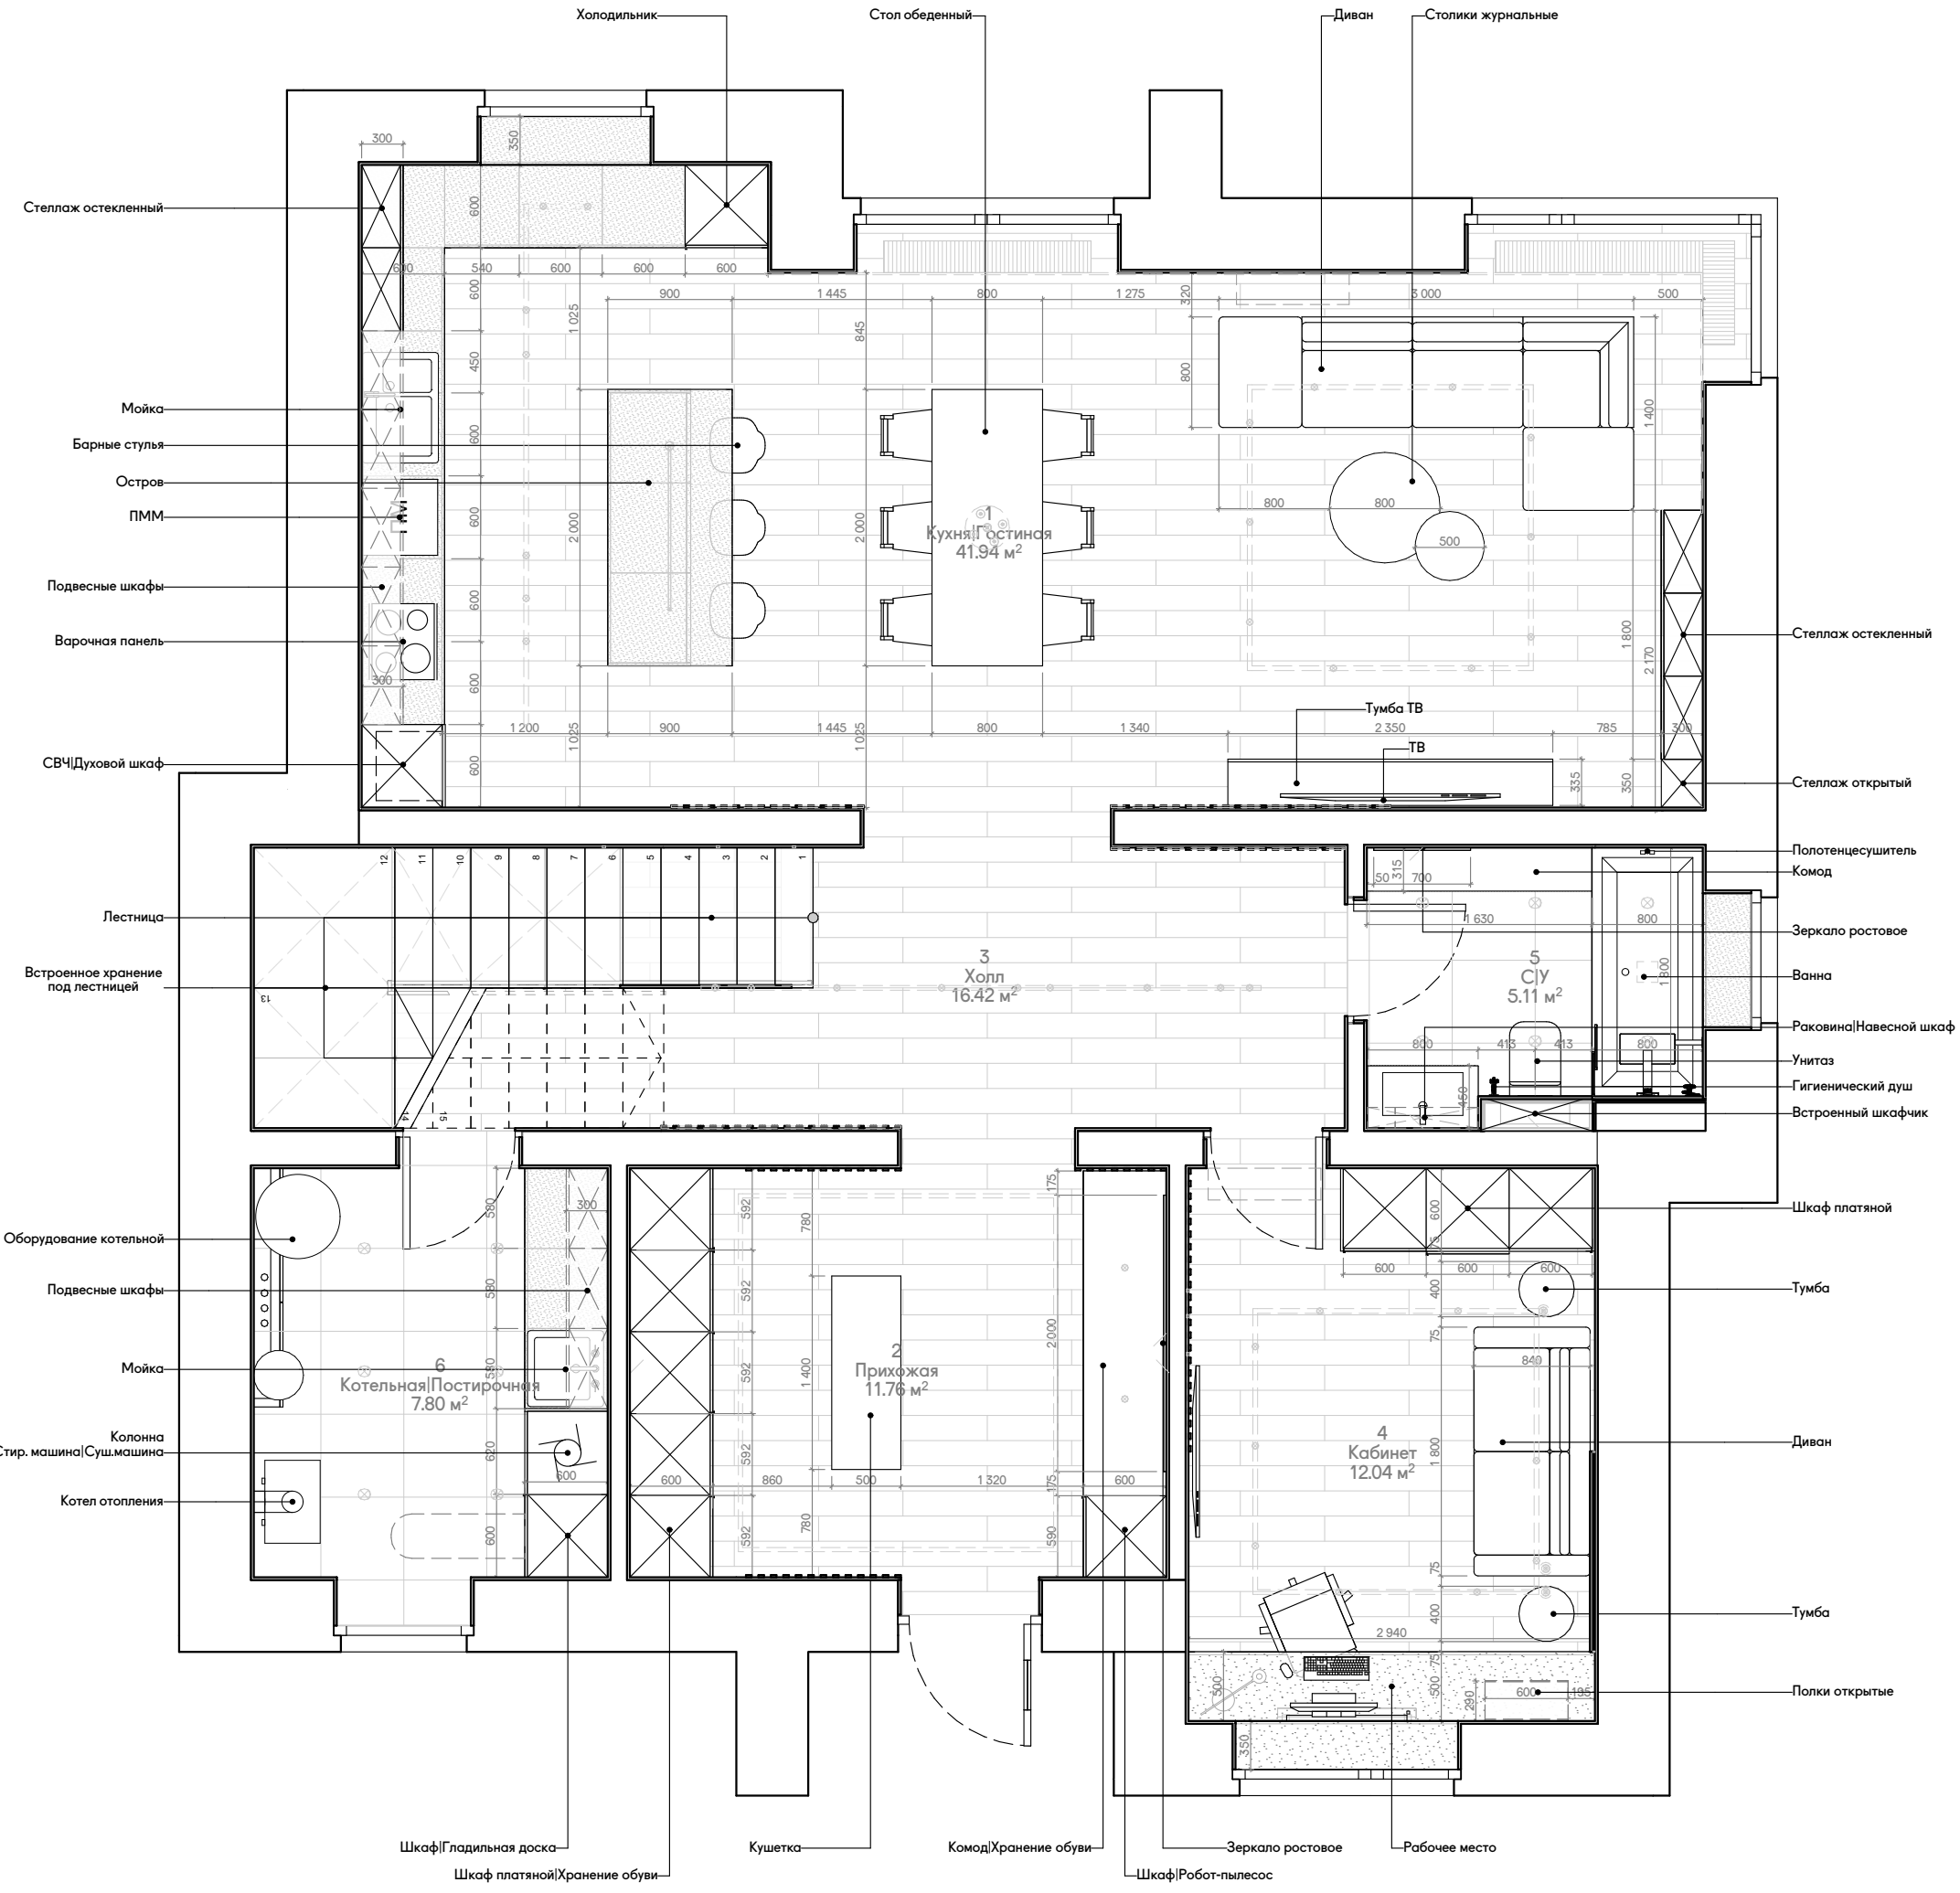

Изм.	Кол.уч	Лист	Док.	Подпись	Дата	ОРИОН-180	Стадия	Лист	Листов
Рук.Маст.		Каличкин А.Д.					Р	85	141
ГАП		Пономарев А.А.							
Архитектор		Муратов Р.Р.				Общая планировка			

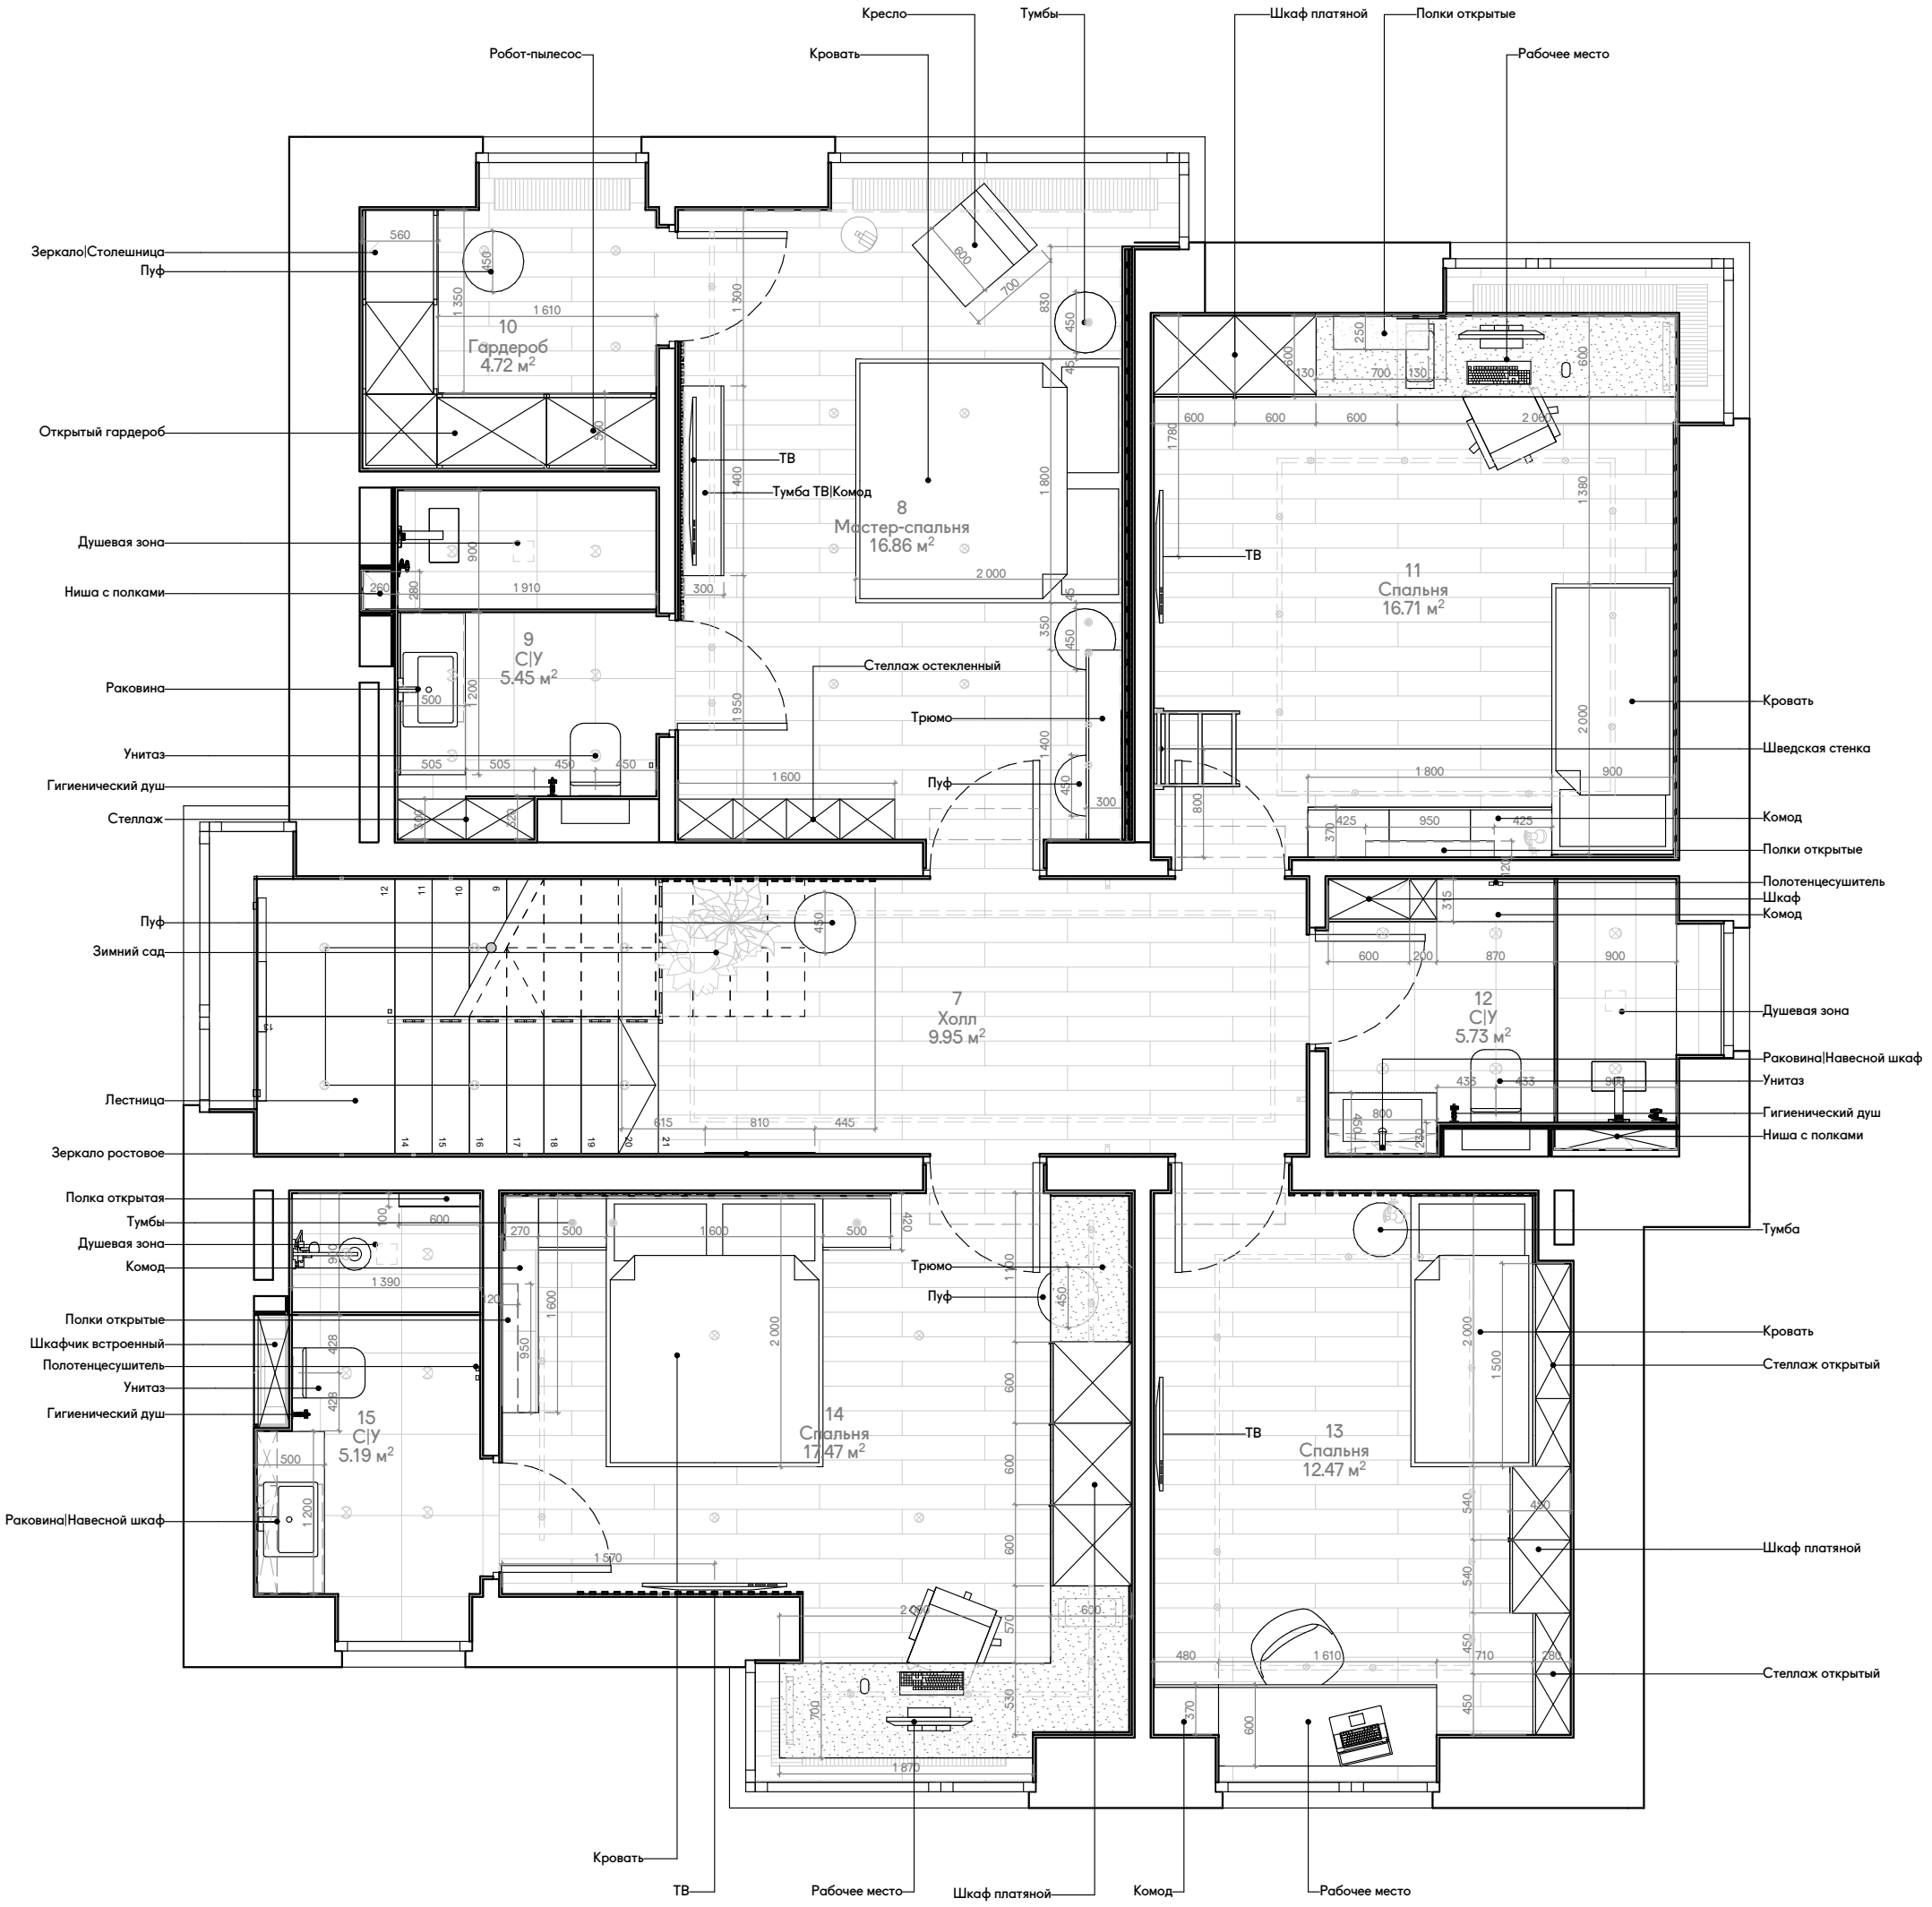

Изм.	Кол.уч	Лист	Док.	Подпись	Дата	ОРИОН-180	Стадия	Лист	Листов
Рук.Маст.		Каличкин А.Д.					Р	86	141
ГАП		Пономарев А.А.							
Архитектор		Муратов Р.Р.				Общая планировка 2			

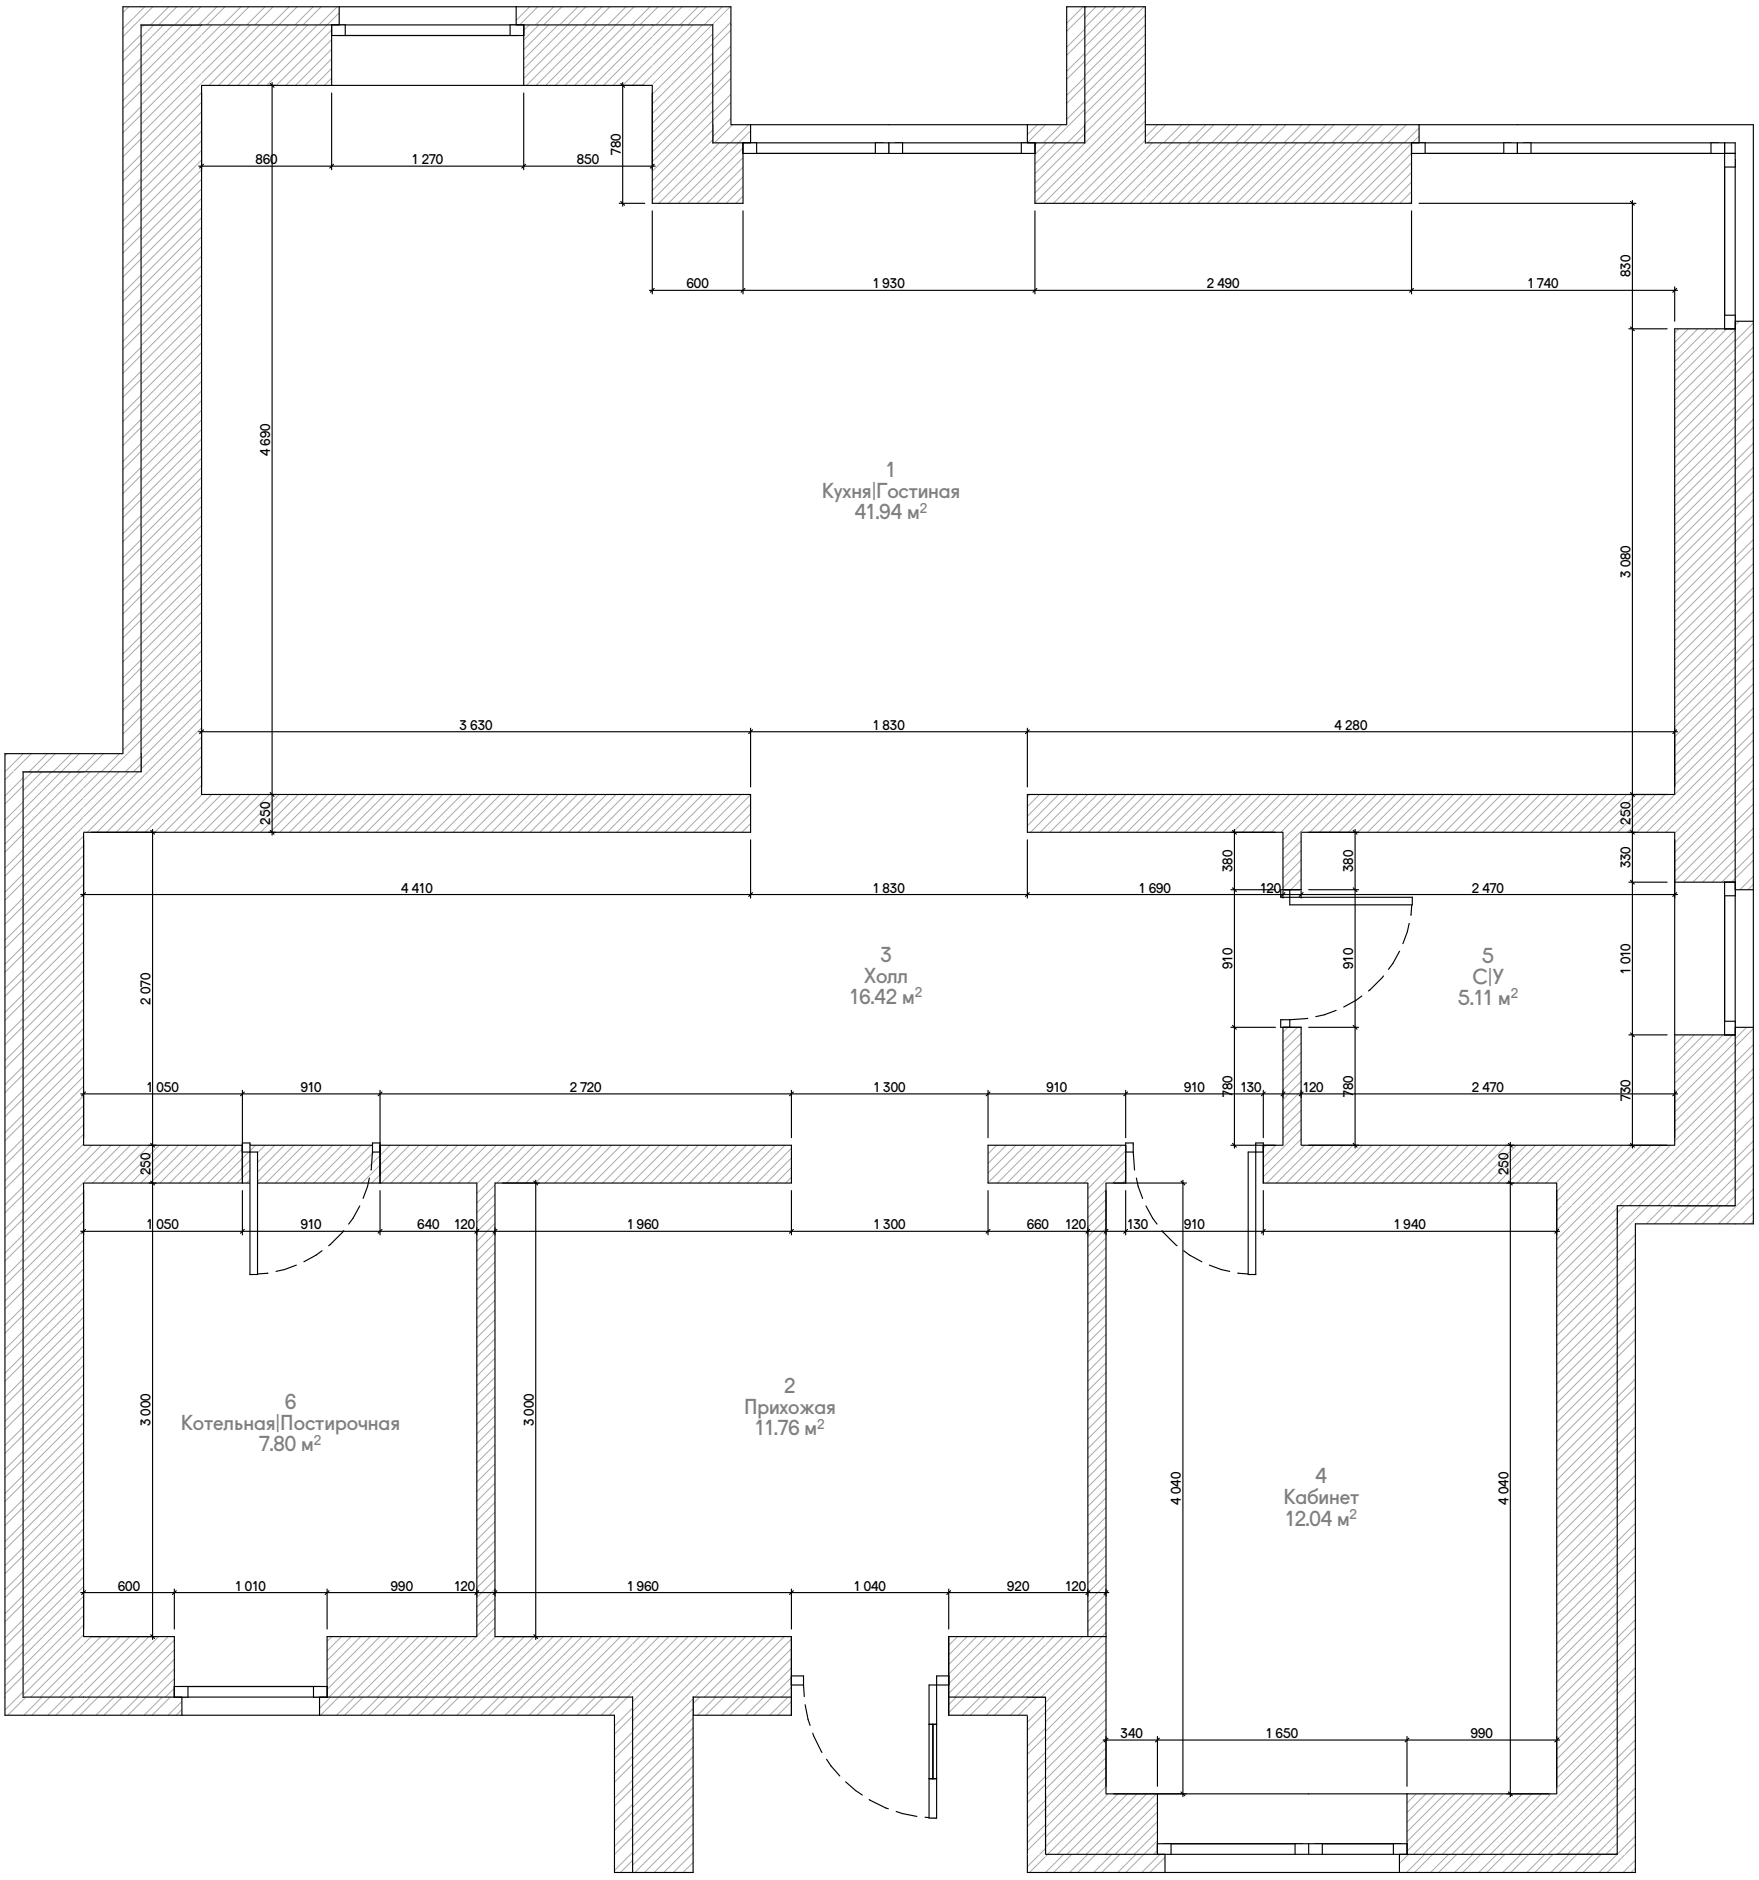

*Размеры указаны на основании рабочей документации, перед началом работ выполнить обмеры фактической геометрии

Изм.	Кол.уч	Лист	Док.	Подпись	Дата	ОРИОН-180	Стадия	Лист	Листов
Рук.Маст.		Каличкин А.Д.					Р	87	141
ГАП		Пономарев А.А.							
Архитектор		Муратов Р.Р.				Обмерный план			

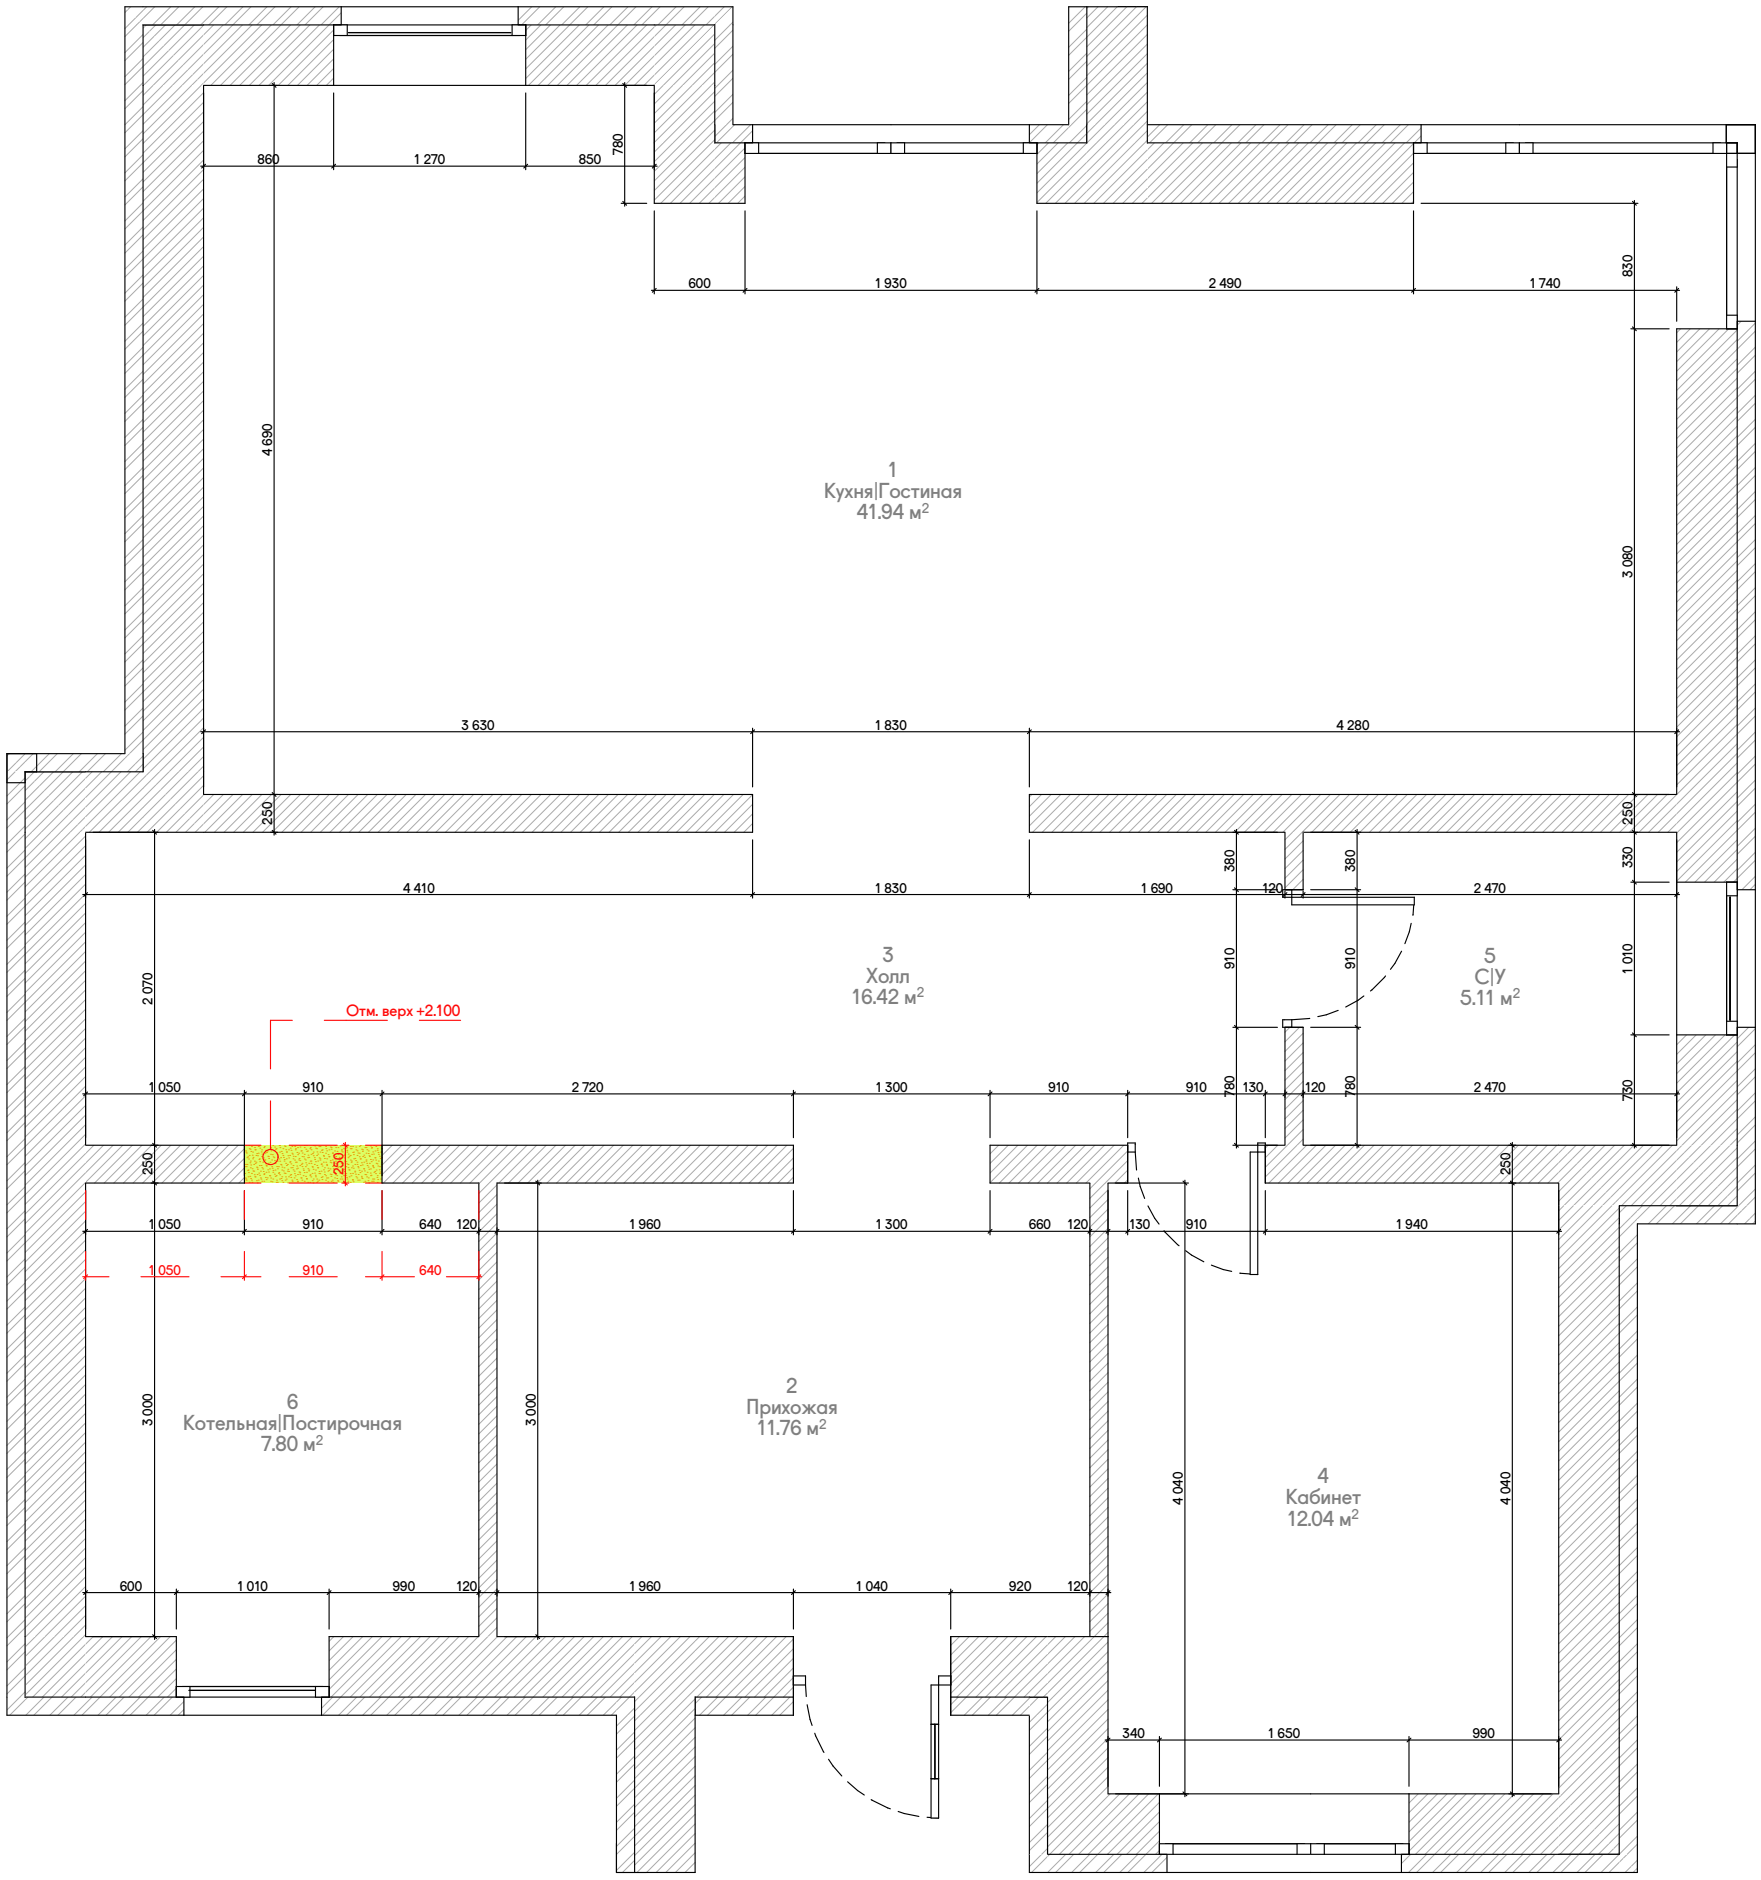

Изм.	Кол.уч	Лист	Док.	Подпись	Дата	ОРИОН-180	Стадия	Лист	Листов
Рук.Маст.		Каличкин А.Д.					Р	89	141
ГАП		Пономарев А.А.							
Архитектор		Муратов Р.Р.				План демонтажа			

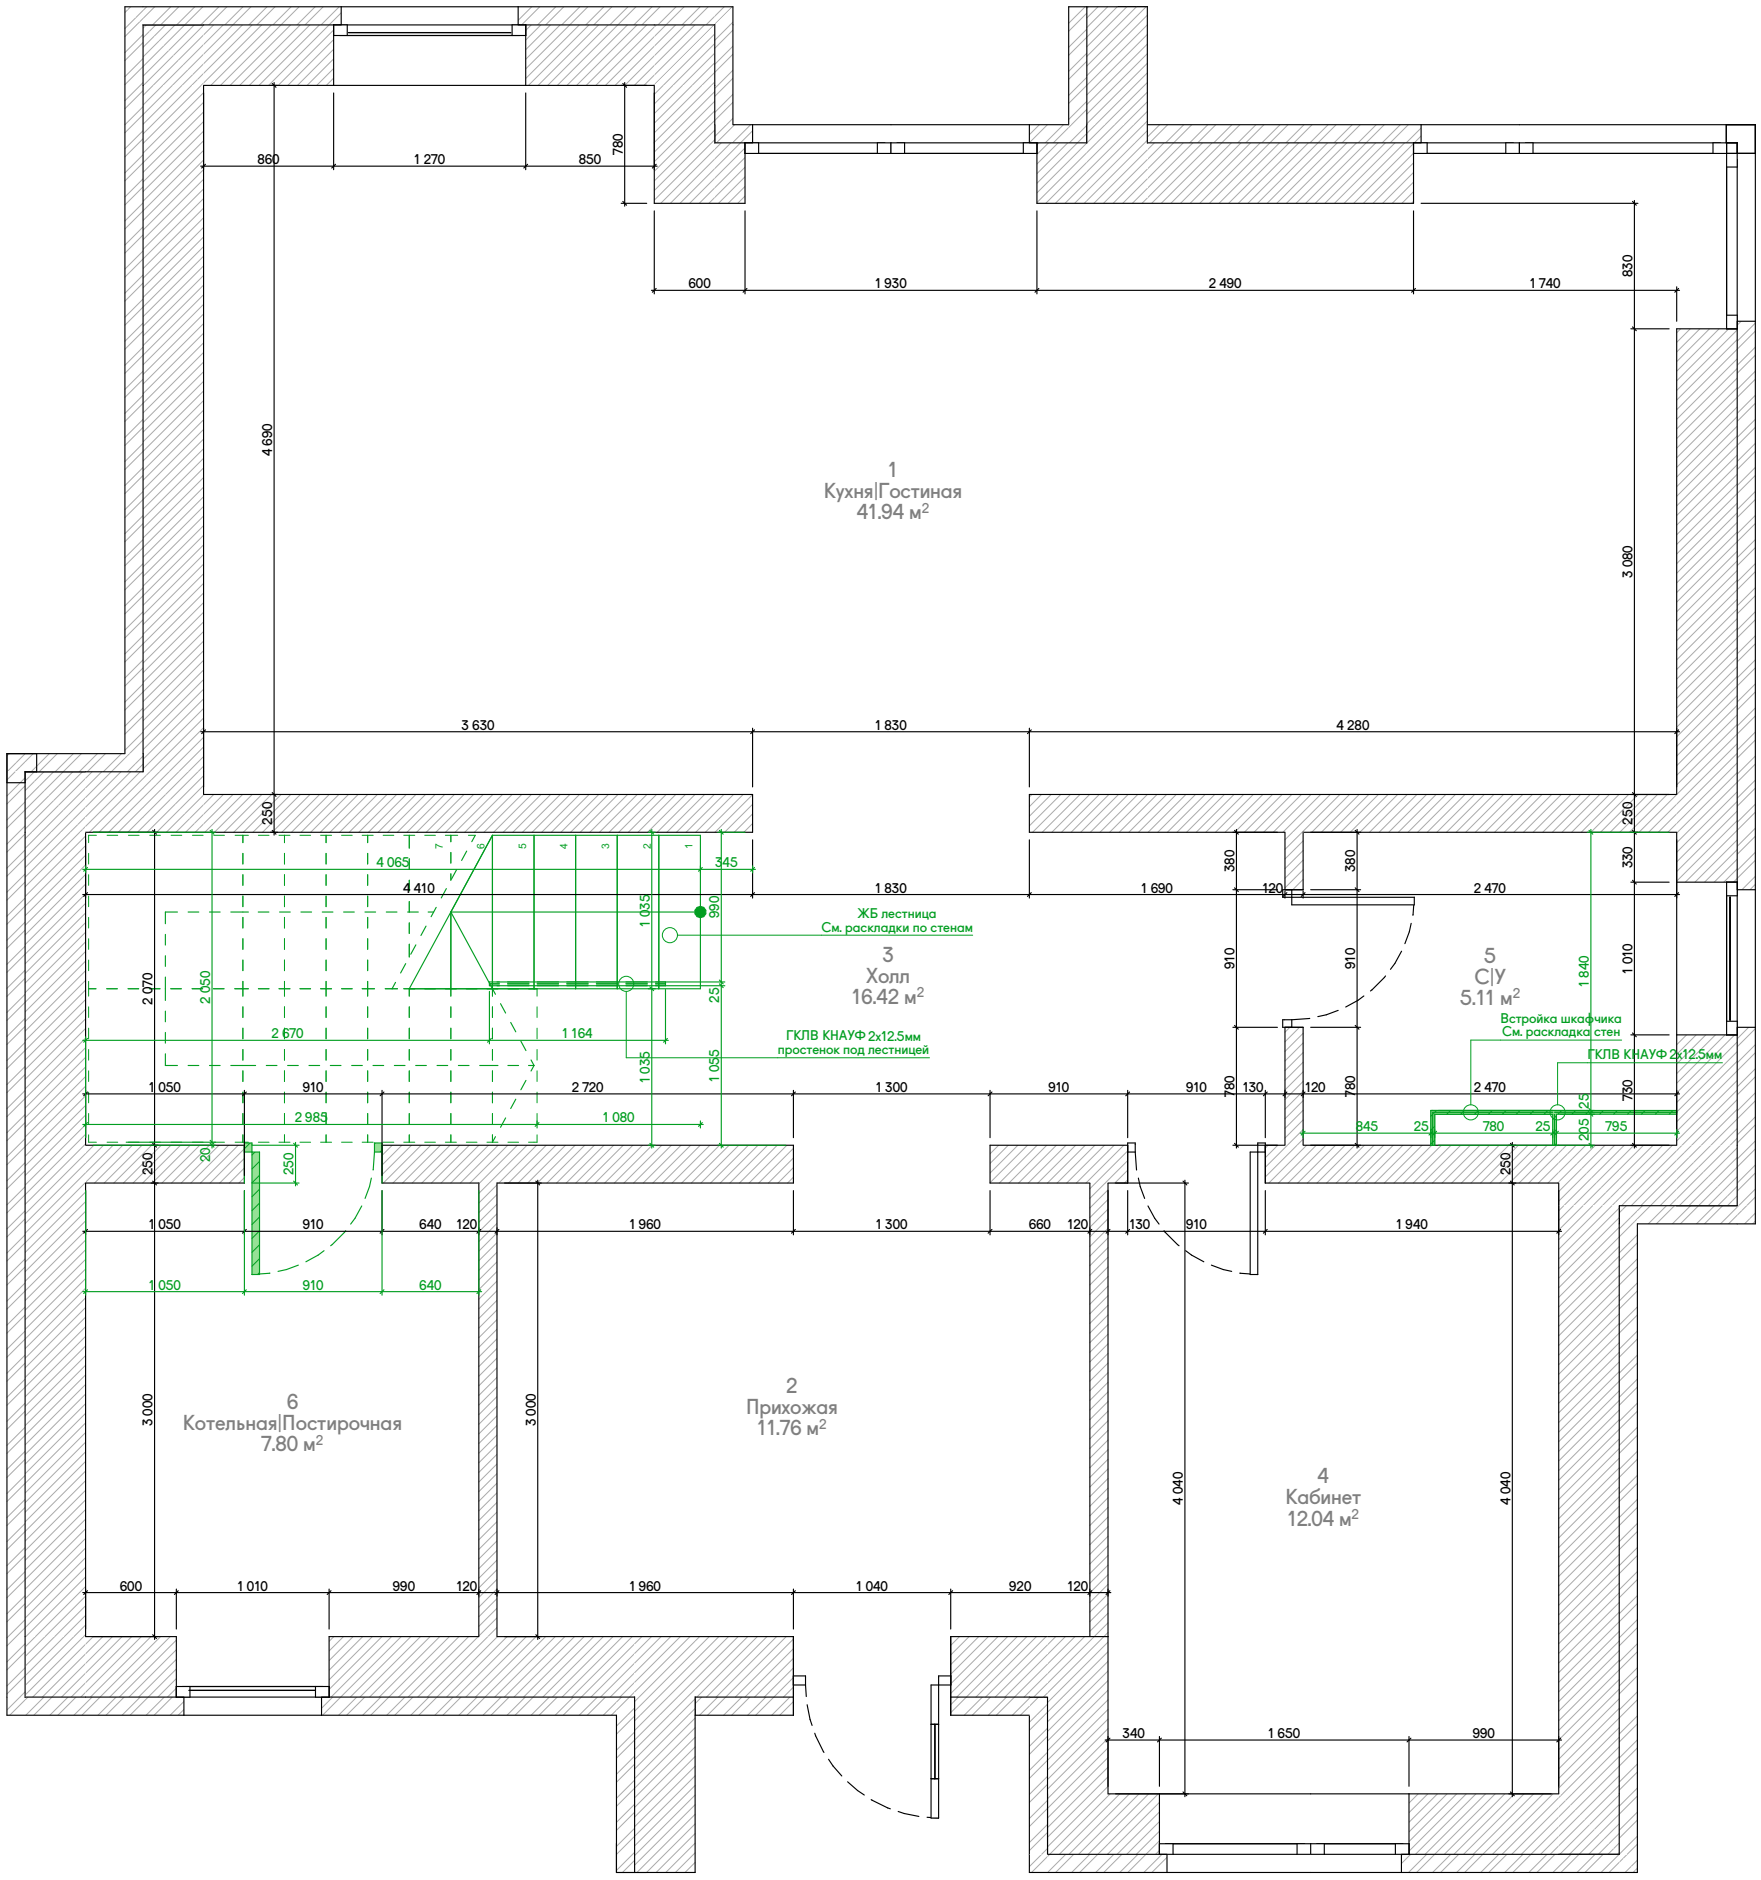

Изм.	Кол.уч	Лист	Док.	Подпись	Дата	ОРИОН-180	Стадия	Лист	Листов
Рук.Маст.		Каличкин А.Д.					Р	90	141
ГАП		Пономарев А.А.							
Архитектор		Муратов Р.Р.				План монтажа			

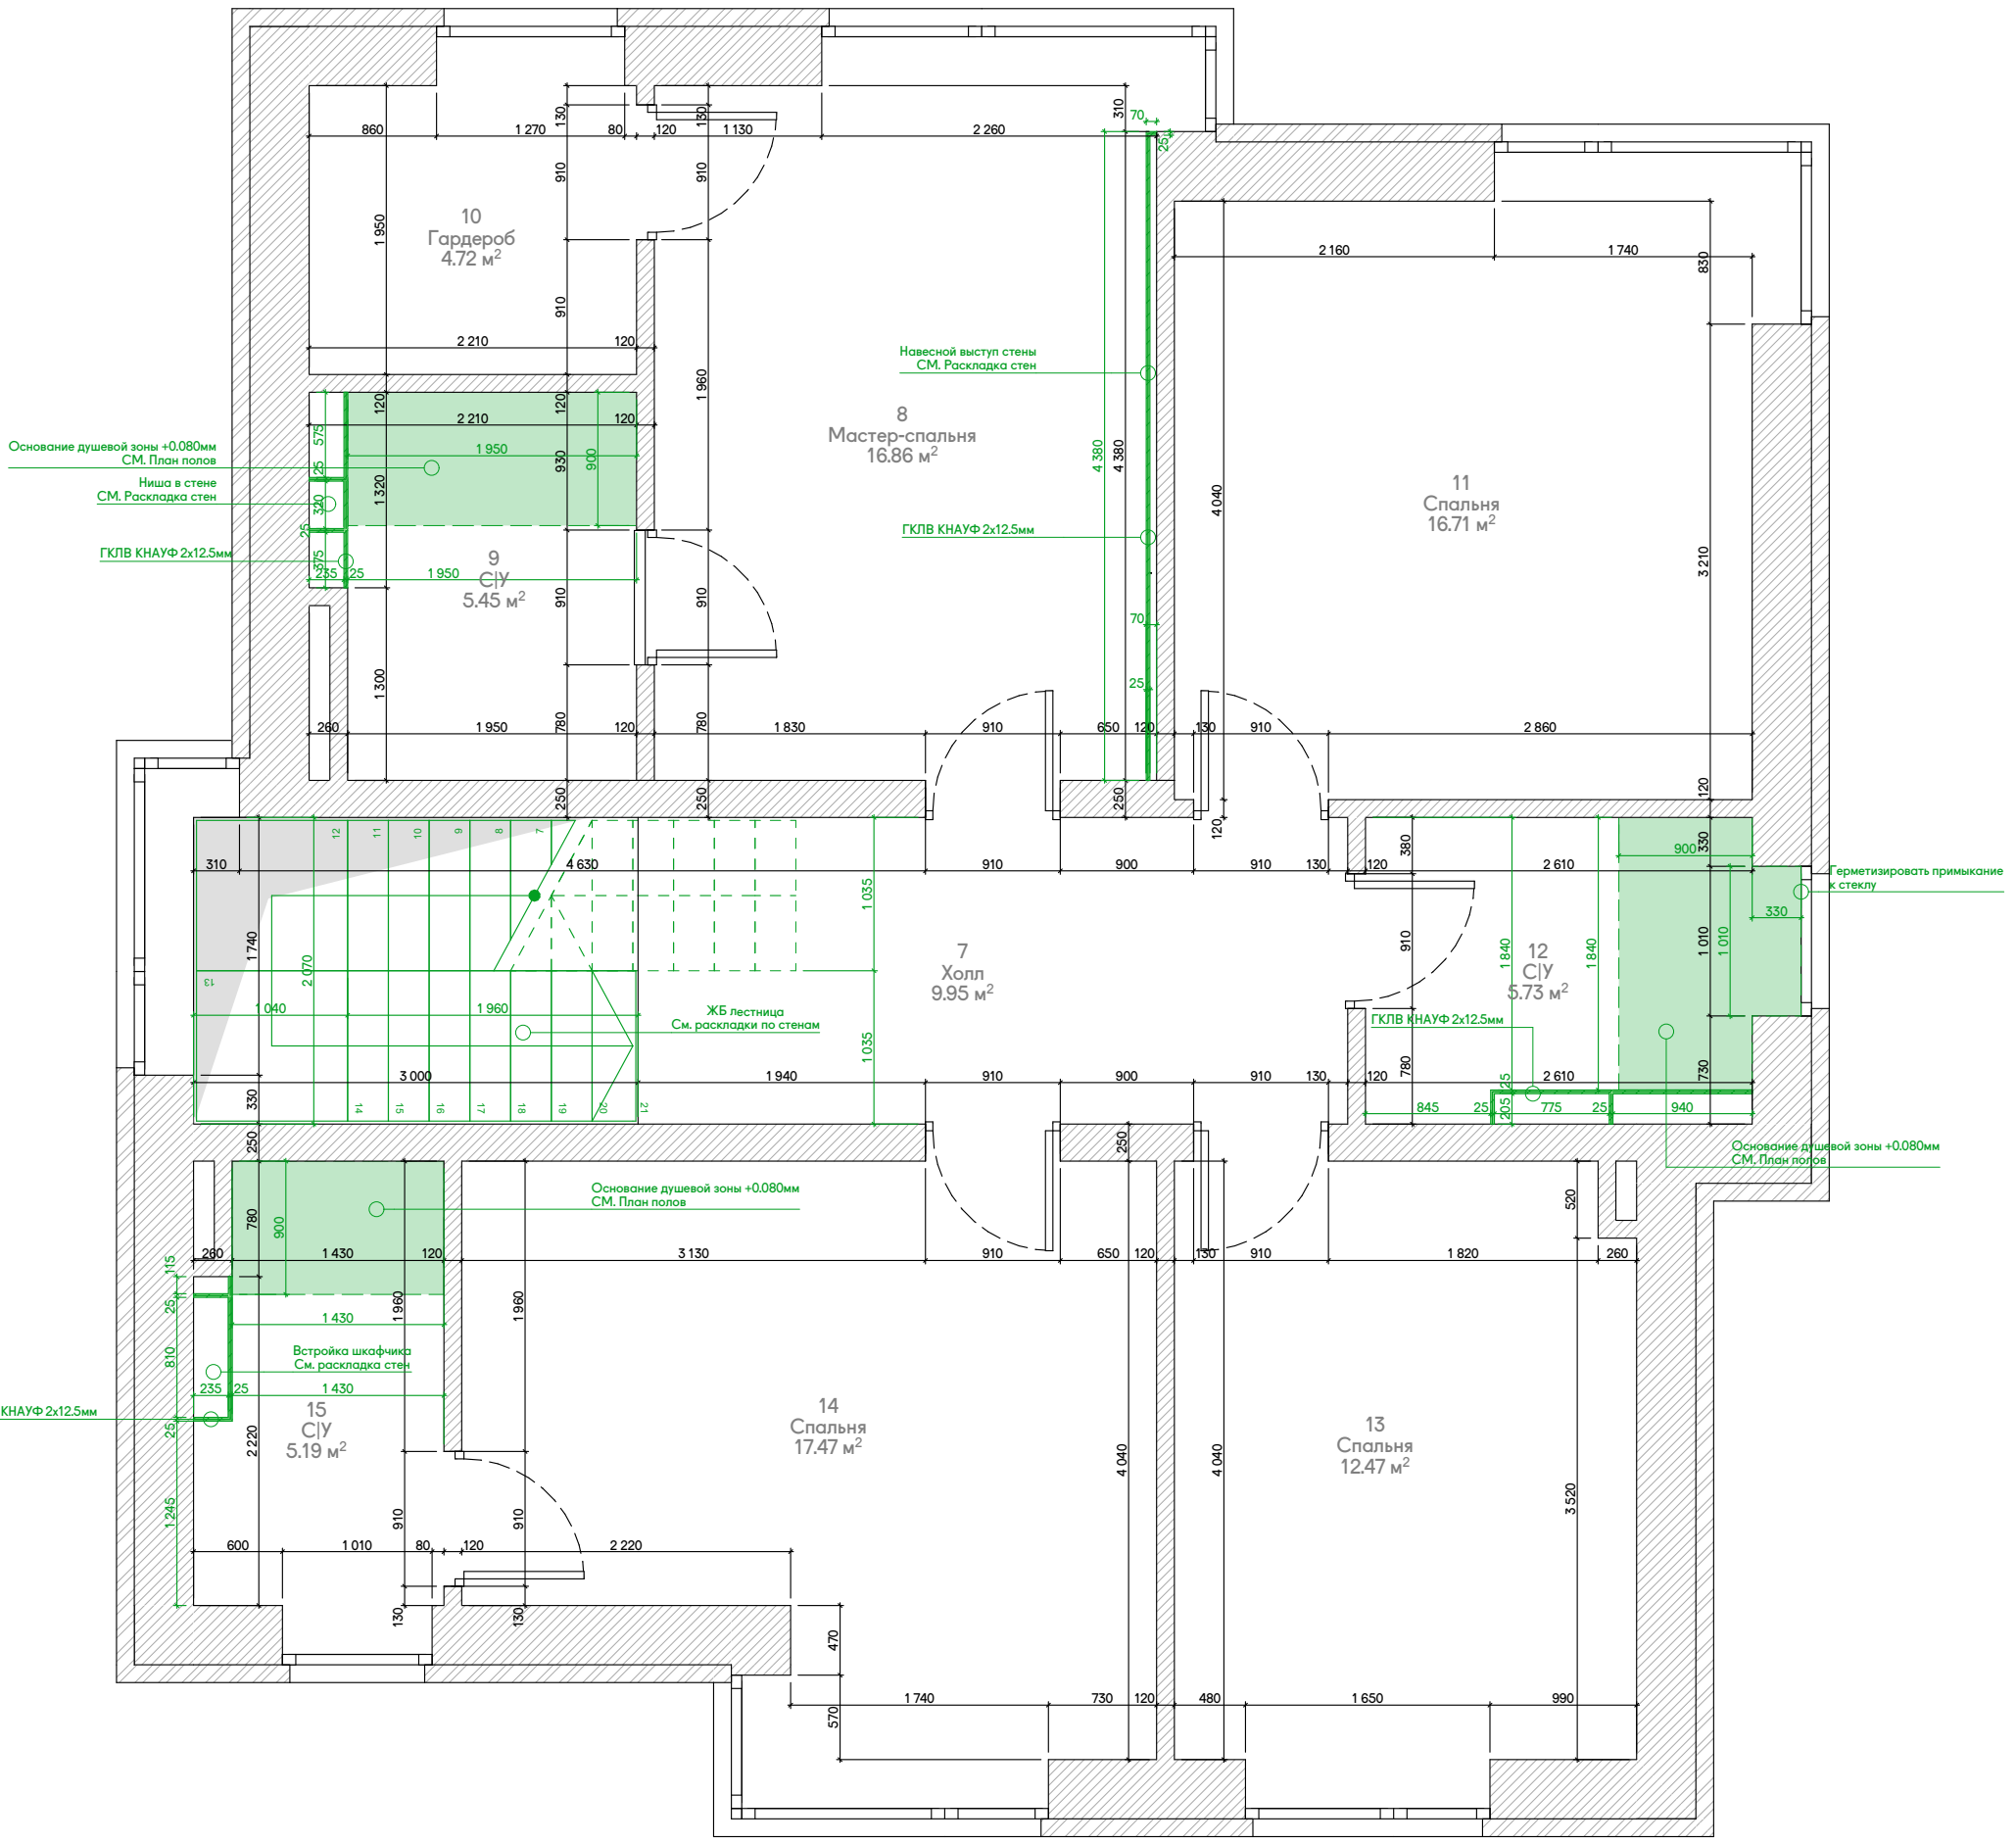

Монтаж стен	
Наименование	Площадь [м2]
ГКЛВ Кнауф 12.5	60.02

Изм.	Кол.уч	Лист	Док.	Подпись	Дата	ОРИОН-180	Стадия	Лист	Листов
Рук.Маст.		Каличкин А.Д.					Р	91	141
ГАП		Пономарев А.А.							
Архитектор		Муратов Р.Р.				План монтажа 2			

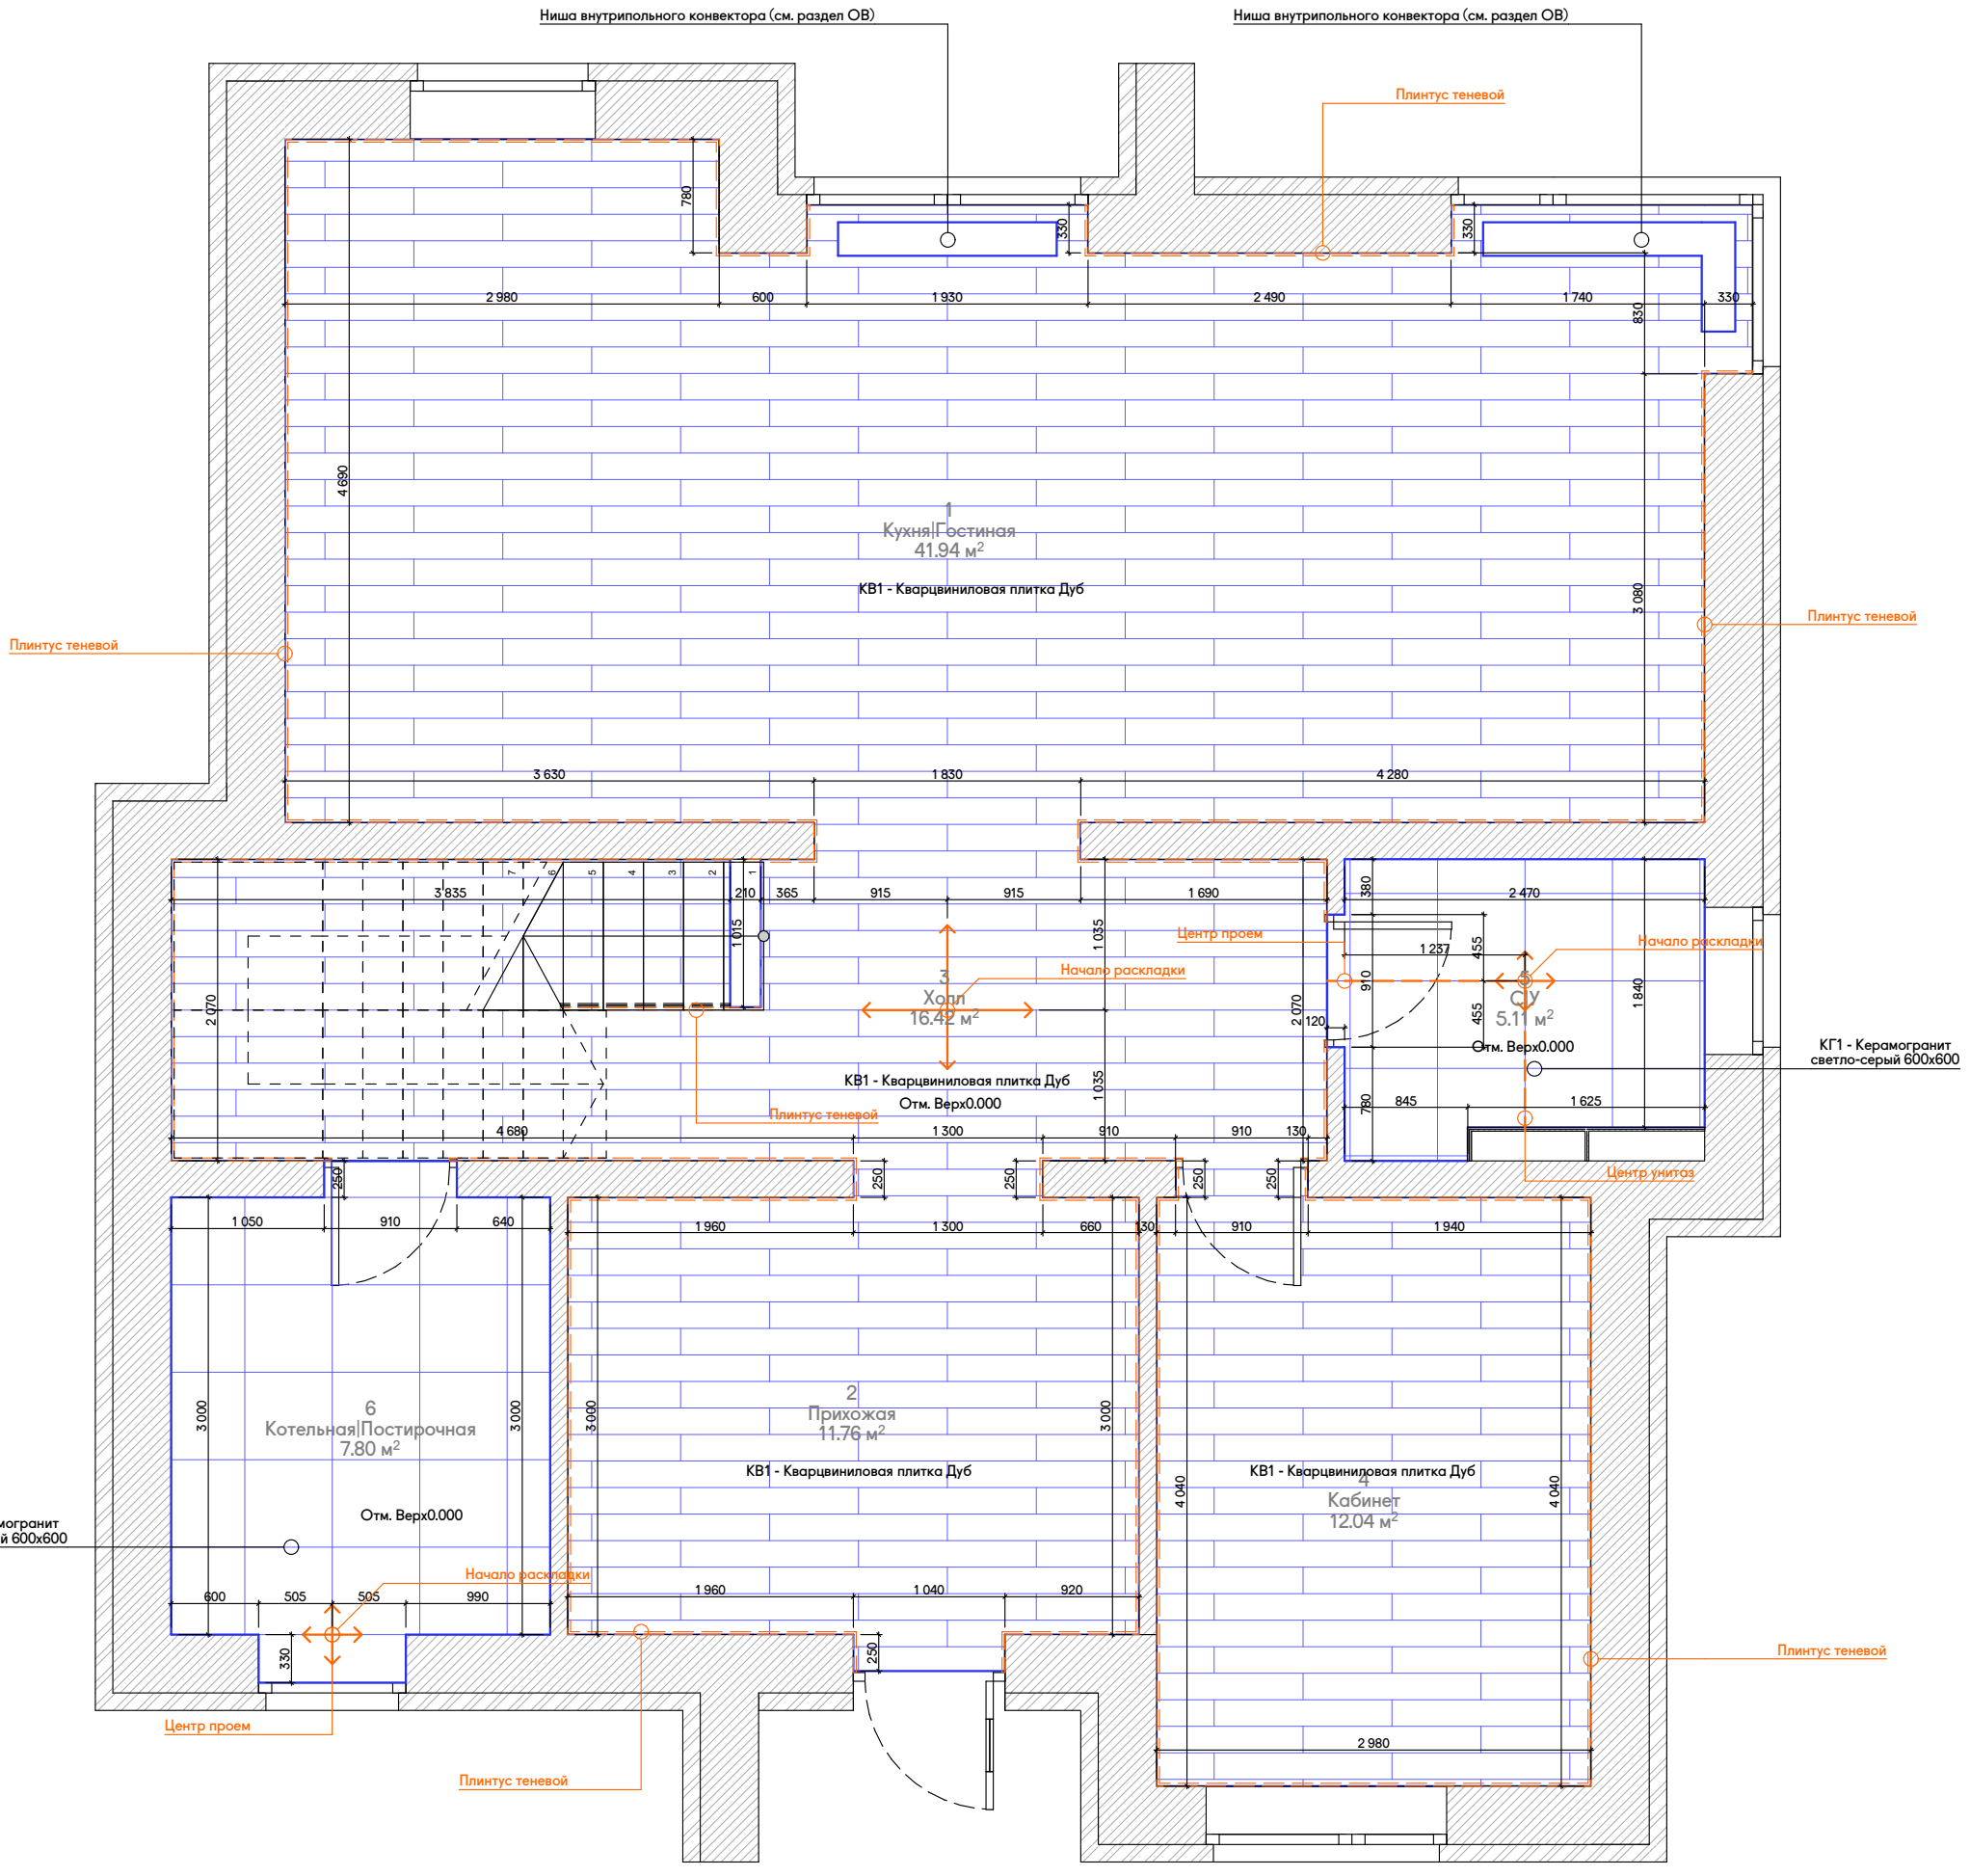

Изм.	Кол.уч	Лист	Док.	Подпись	Дата	ОРИОН-180	Стадия	Лист	Листов
Рук.Маст.		Каличкин А.Д.					Р	95	141
ГАП		Пономарев А.А.							
Архитектор		Муратов Р.Р.				План покрытий пола			

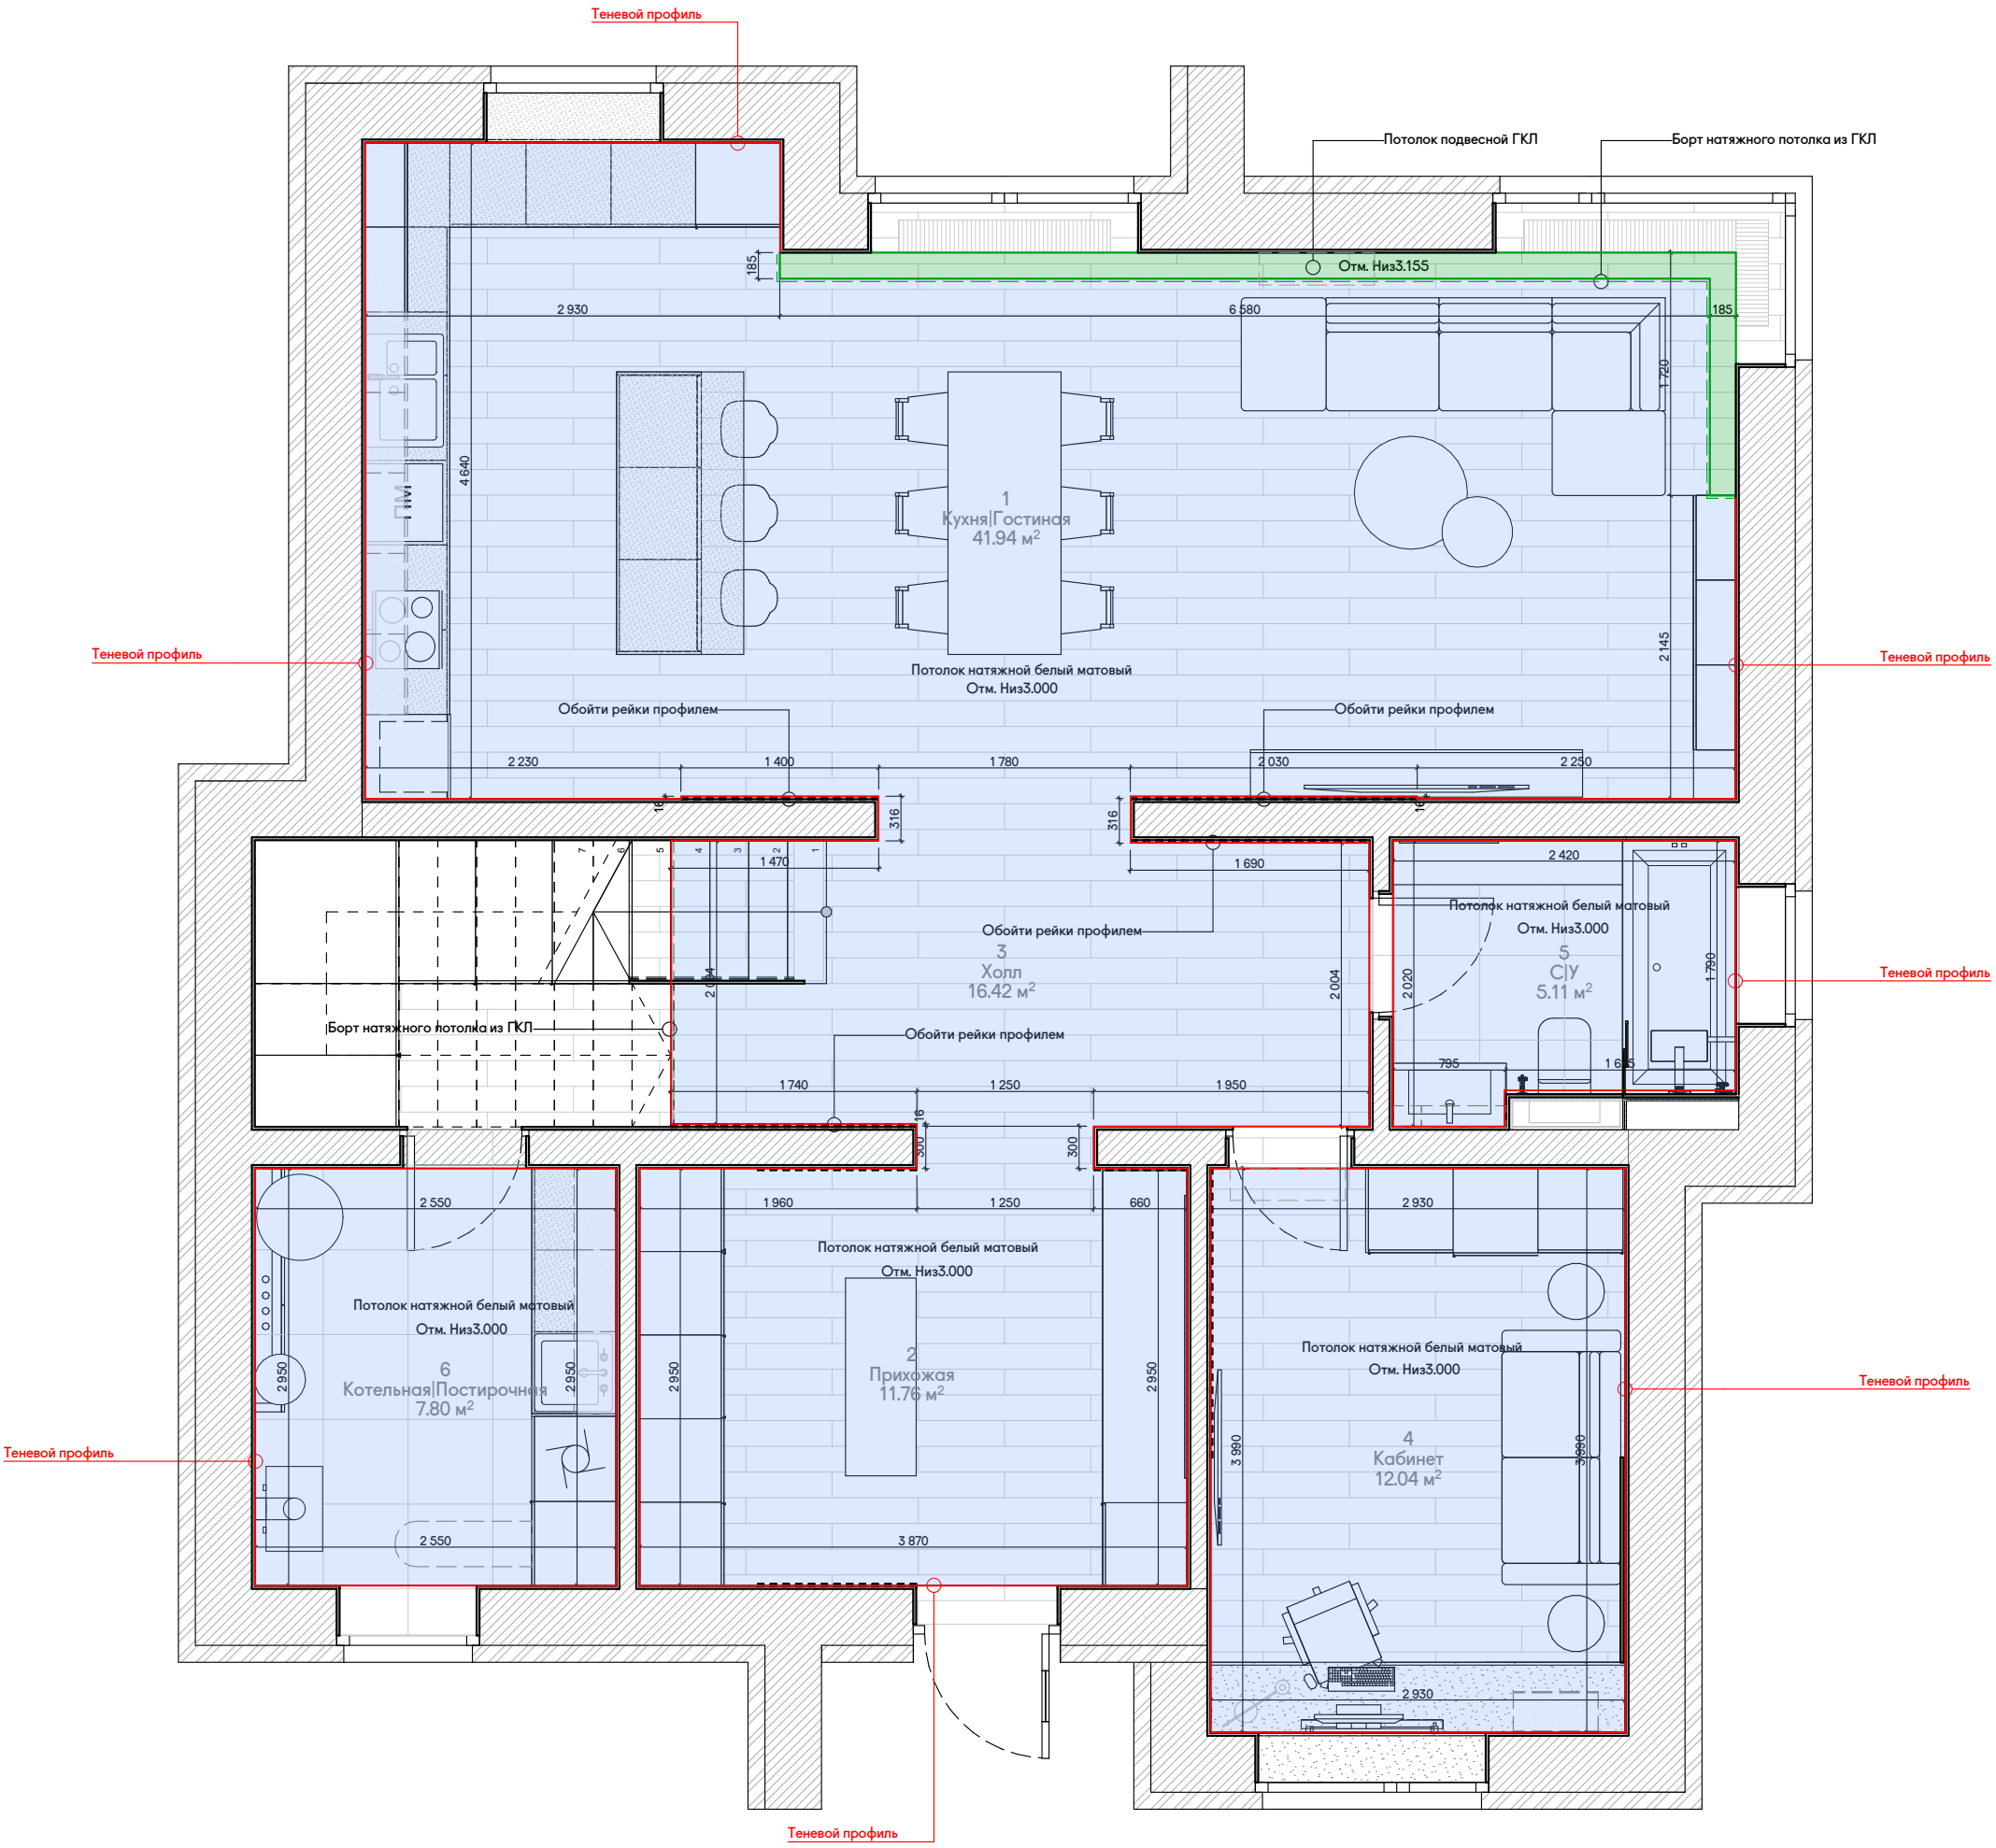

*Размеры даны для справки, утвердить отметки потолков после обмеров фактической геометрии

Изм.	Кол.уч	Лист	Док.	Подпись	Дата	ОРИОН-180	Стадия	Лист	Листов
Рук.Маст.		Каличкин А.Д.					Р	99	141
ГАП		Пономарев А.А.							
Архитектор		Муратов Р.Р.				План потолков			

A510

Подготовка поверхностей|материалы		
Наименование	Примечание	Площадь [м2]
Выравнивание стен под покраску (ГКЛ/Штукатурка)	Выбор выравнивания стен на усмотрение подрядчика	446.96
ГКЛВ Кнауф 12.5	или аналог	64.77
Керамогранит	или аналог	132.02
Панели ЛДСП		22.70

Основные отделочные материалы			
Наименование в проекте	Внешний вид	Наименование подбор	Учитываемая Площадь [м2]
КВ1" - Кварцвиниловая плитка Дуб		ABA плитка Atrium Дуб Артисан класс 33 с фаской толщина 5 мм 182х1220мм	155.22
КГ1" - Керамогранит светло-серый 600х600		Kerama Marazzi Про Дабл DD601520R бежевый светлый обрезной 600х600х9мм	79.37
КГ2"- Керамогранит Бежевый Дерево Узор 300х600		Kerama Marazzi Про Дабл OS\C317\11236R Декор чипсет бежевый матовый обрезной 30х60х0,9	8.91
КГ3" - Керамогранит Бежевый Дерево 300х600		Kerama Marazzi Про Дабл 11236R бежевый матовый обрезной 300х600х9мм	11.24
КГ4" - Керамогранит белый 300х900		Kerama Marazzi KM3090B0140R Тубкаль белый глянцевый обрезной 300х8,5х9мм	34.04
КГ5" - Керамогранит Черный 300х900	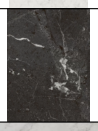	Kerama Marazzi KM3090B0150R Тубкаль чёрный глянцевый обрезной 300х895х9мм	10.45
КГ6" - Керамогранит белый 600х600		Kerama Marazzi KM6060G0321R Тубкаль белый матовый обрезной 600х600х9мм	6.33
КР1" - Краска Белая Матовая		Tikkurila Euro Smart 2 Белый или аналог	457.68
КР2" - Краска Антрацит Матовая		Tikkurila Euro Smart 2 Y499 или аналог	7.60
ЛП1" - ЛДСП Панель Дуб светлый		Egger H3165 ST12 Дуб Виченца светлый	13.28
ЛП2" - ЛДСП Панель Дуб светлый (Сонома)		Дуб Сонома 3025 PR	9.68
НП1" - Натяжной потолок Белый Матовый		Белый матовый	173.29
ШТ1" - Штукатурка декоративная Антрацит	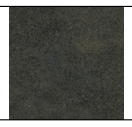	Valpaint Klondike 451A + GOLD G100	8.70

Плинтус напольный подбор			
Наименование в проекте	Внешний вид	Наименование подбор	Длина (мм)
Плинтус теневой напольный	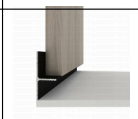	Плинтус с теневым зазором (комплектный с дверями) Tenevoy.ru	134 550.0

Профиль потолочный подбор			
Наименование в проекте	Внешний вид	Наименование подбор	Длина (мм)
Профиль теневой потолочный		EUROKRAAB теневой профиль для натяжных потолков	185 129.9

Изм.	Кол.уч	Лист	Док.	Подпись	Дата	ОРИОН-180	Стадия	Лист	Листов
Рук.Маст.		Каличкин А.Д.					Р	101	141
ГАП		Пономарев А.А.							
Архитектор		Муратов Р.Р.				Ведомость основных отделочных материалов			

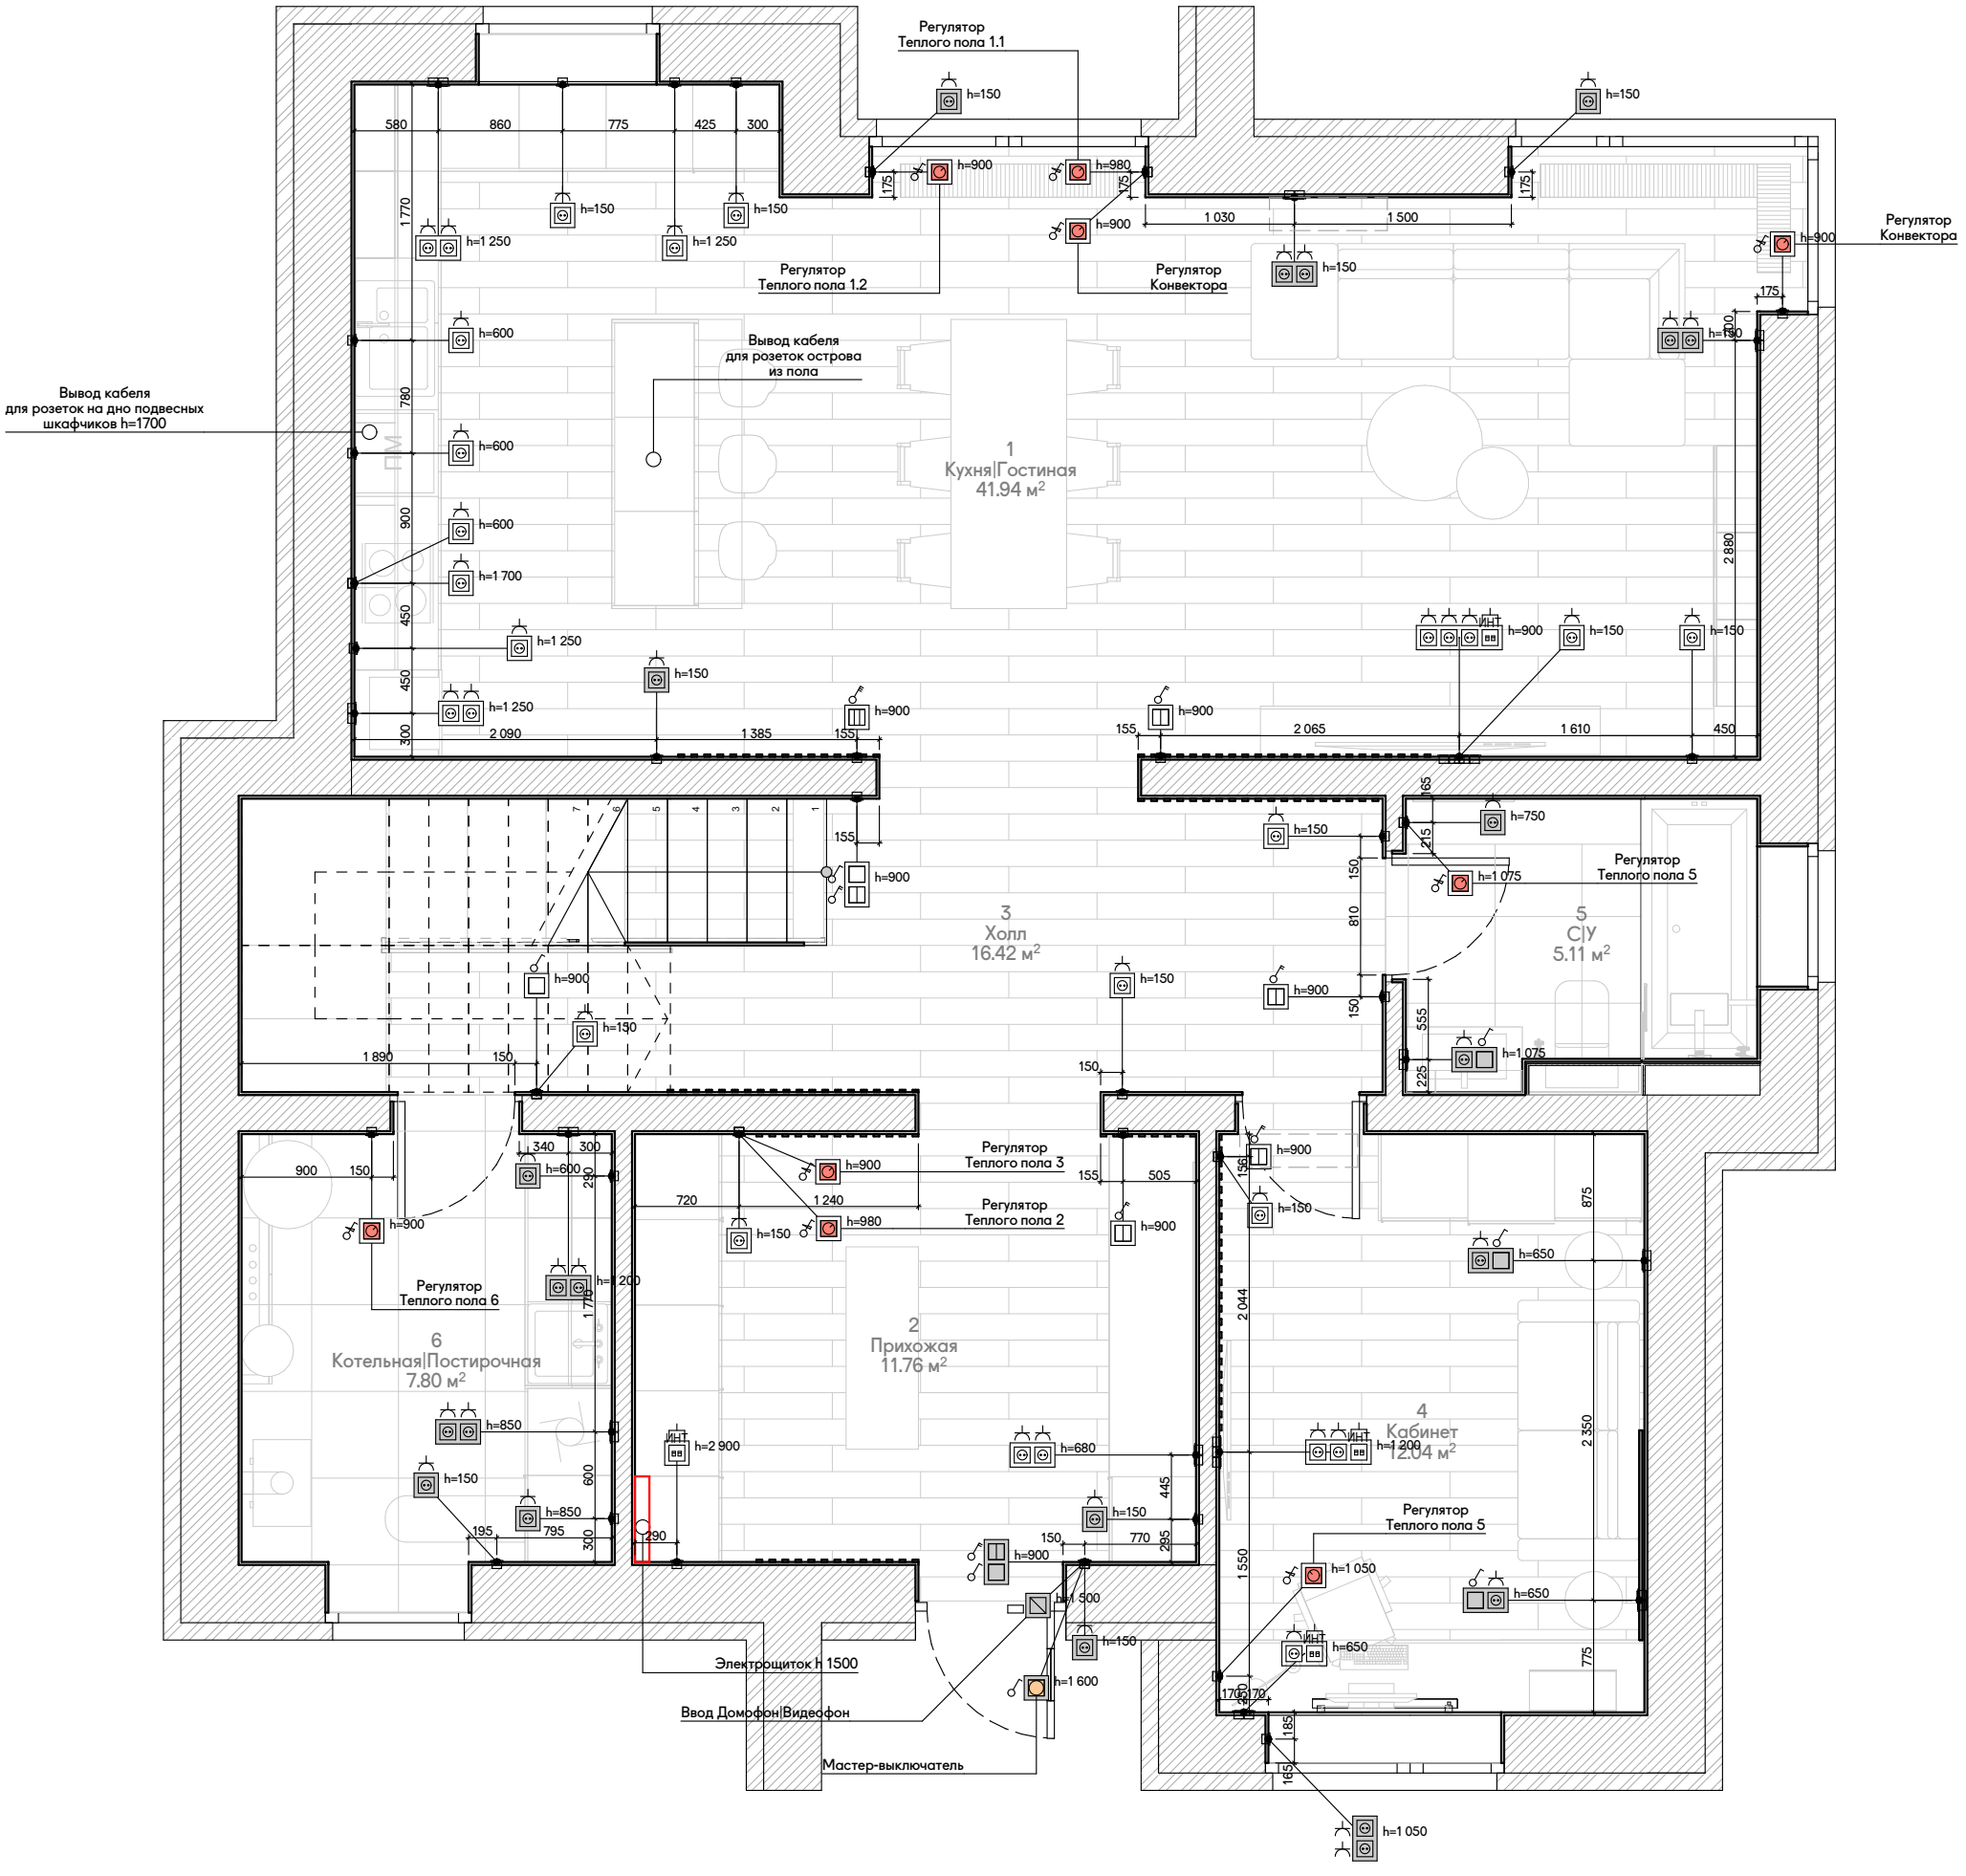

*Схематичное изображение выключателей и рамок на плане показано лицевой стороной по отношению к смотрящему

Изм.	Кол.уч	Лист	Док.	Подпись	Дата	ОРИОН-180	Стадия	Лист	Листов
Рук.Маст.		Каличкин А.Д.					Р	107	141
ГАП		Пономарев А.А.							
Архитектор		Муратов Р.Р.				Нижняя разводка электроприборов			

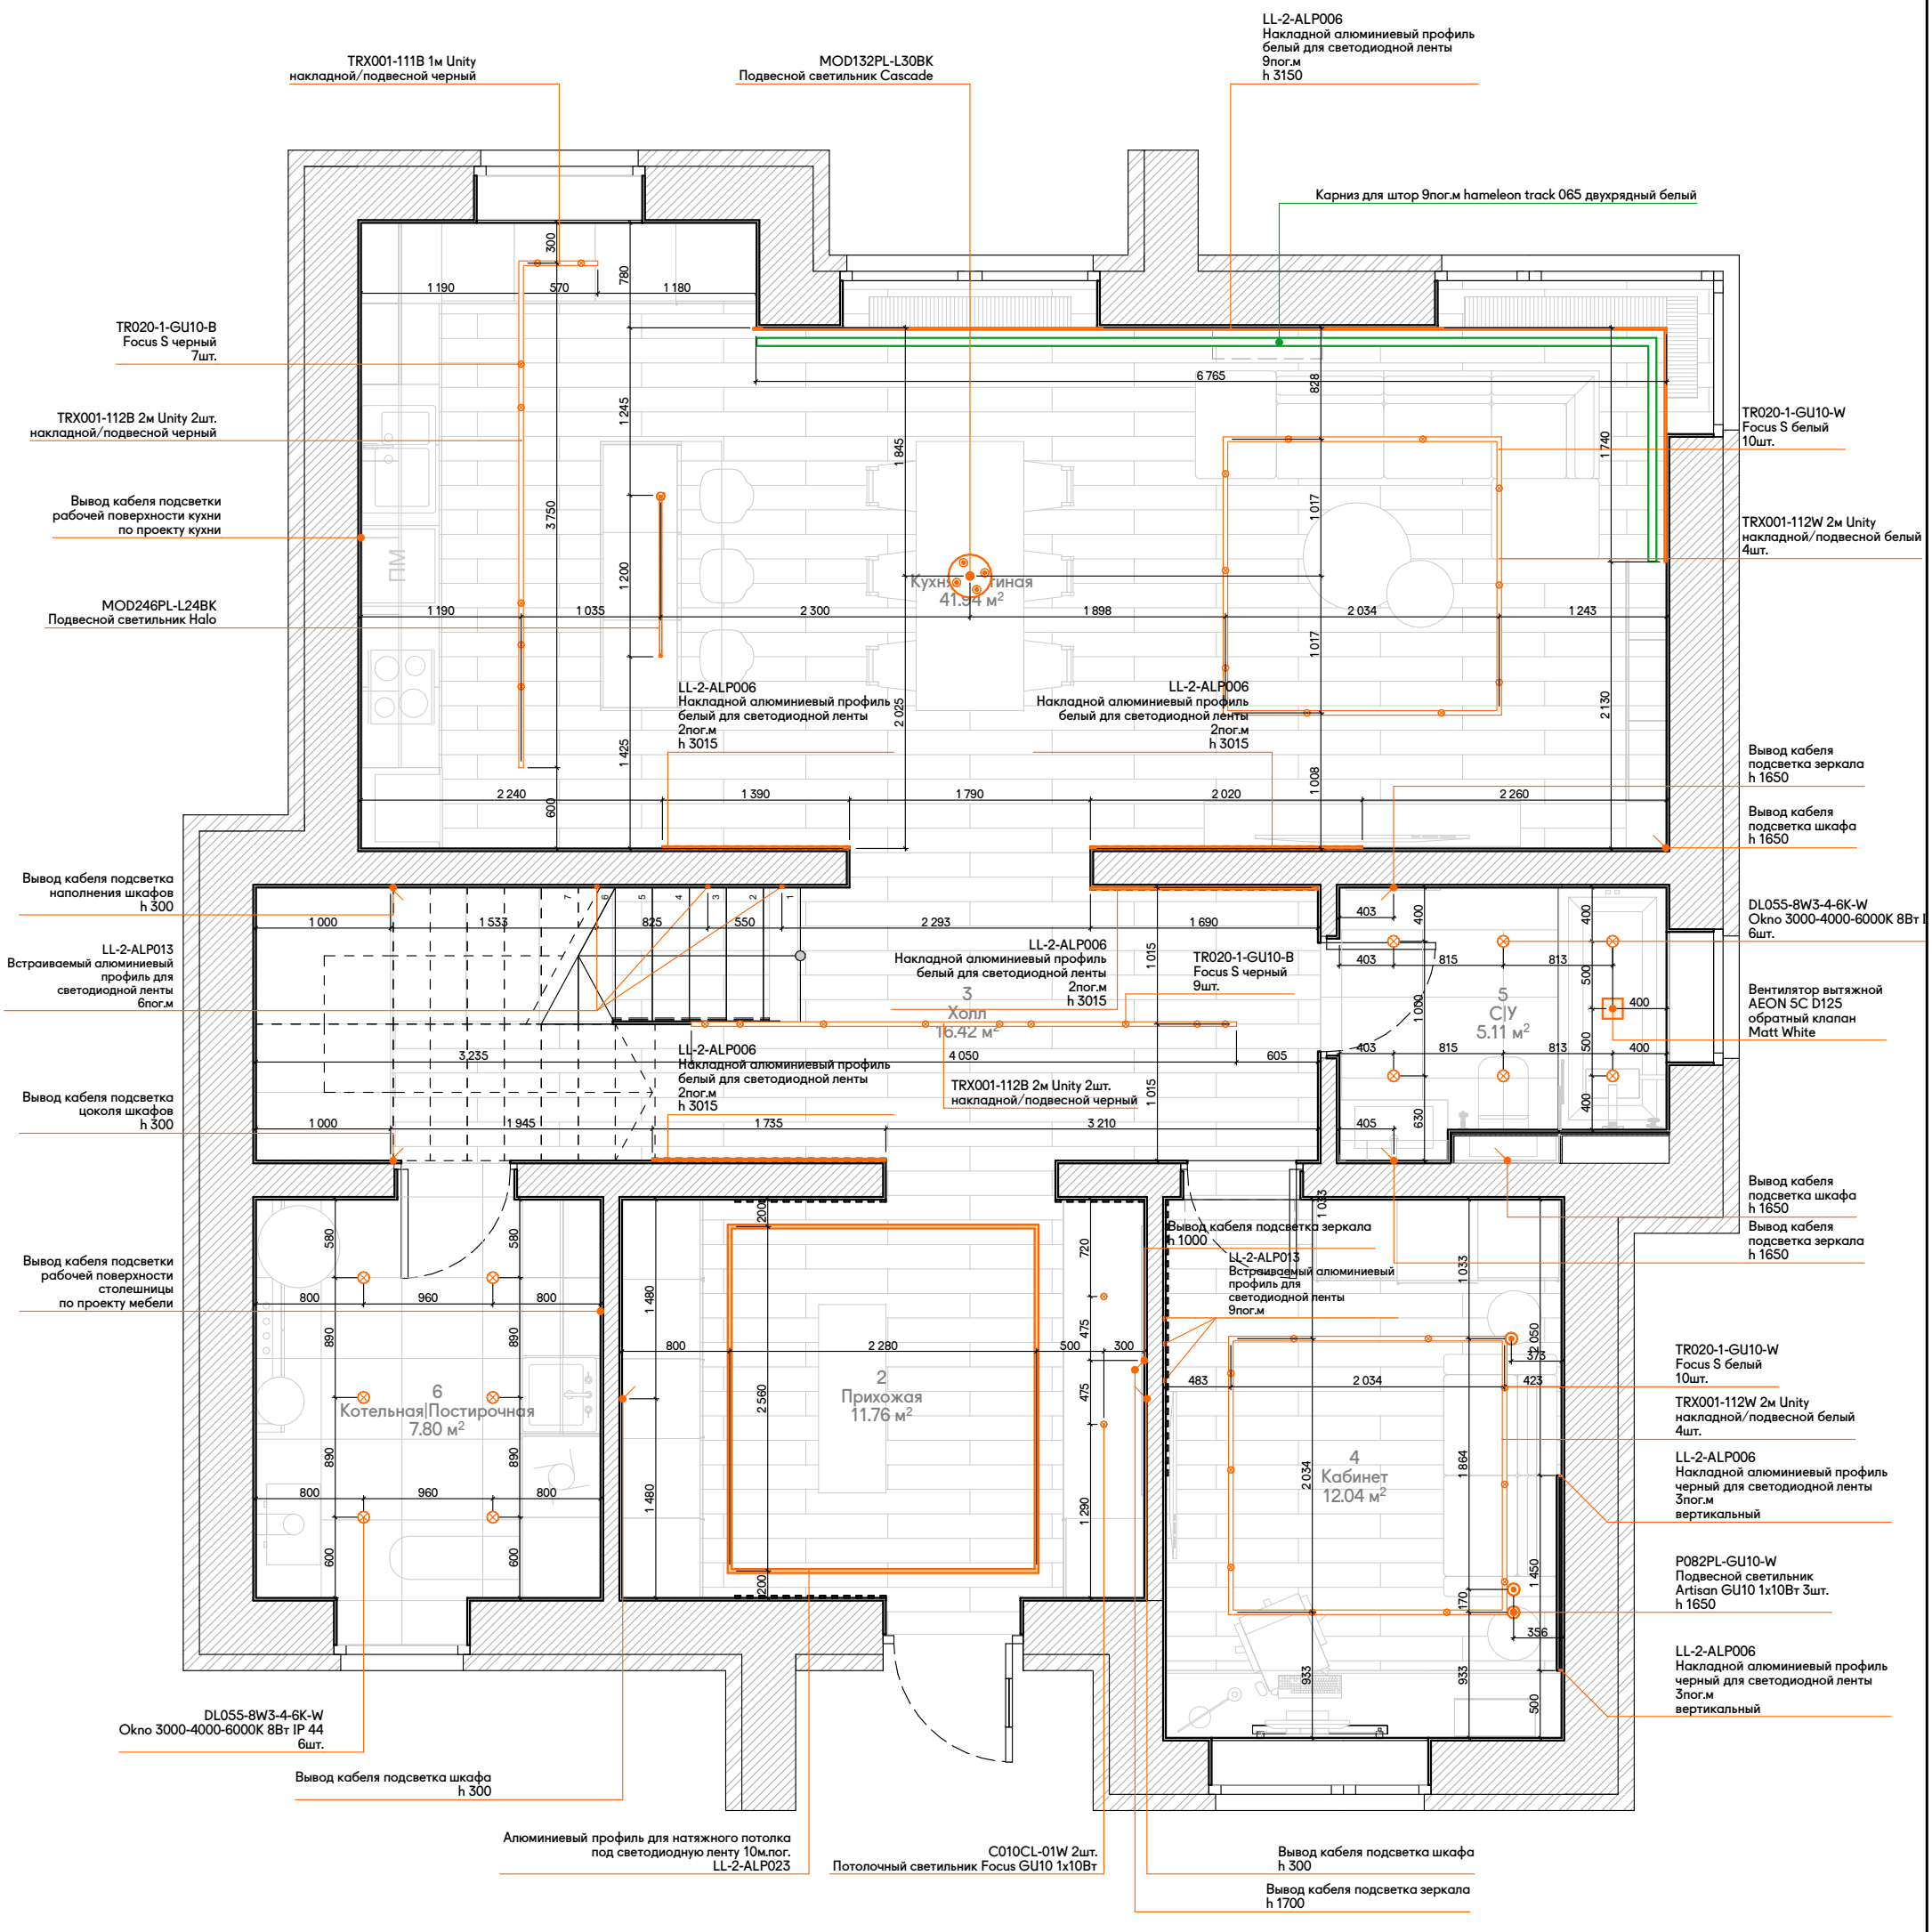

Изм.	Кол.уч	Лист	Док.	Подпись	Дата	ОРИОН-180	Стадия	Лист	Листов
Рук.Маст.		Каличкин А.Д.					Р	109	141
ГАП		Пономарев А.А.							
Архитектор		Муратов Р.Р.				Верхняя разводка электроприборов			

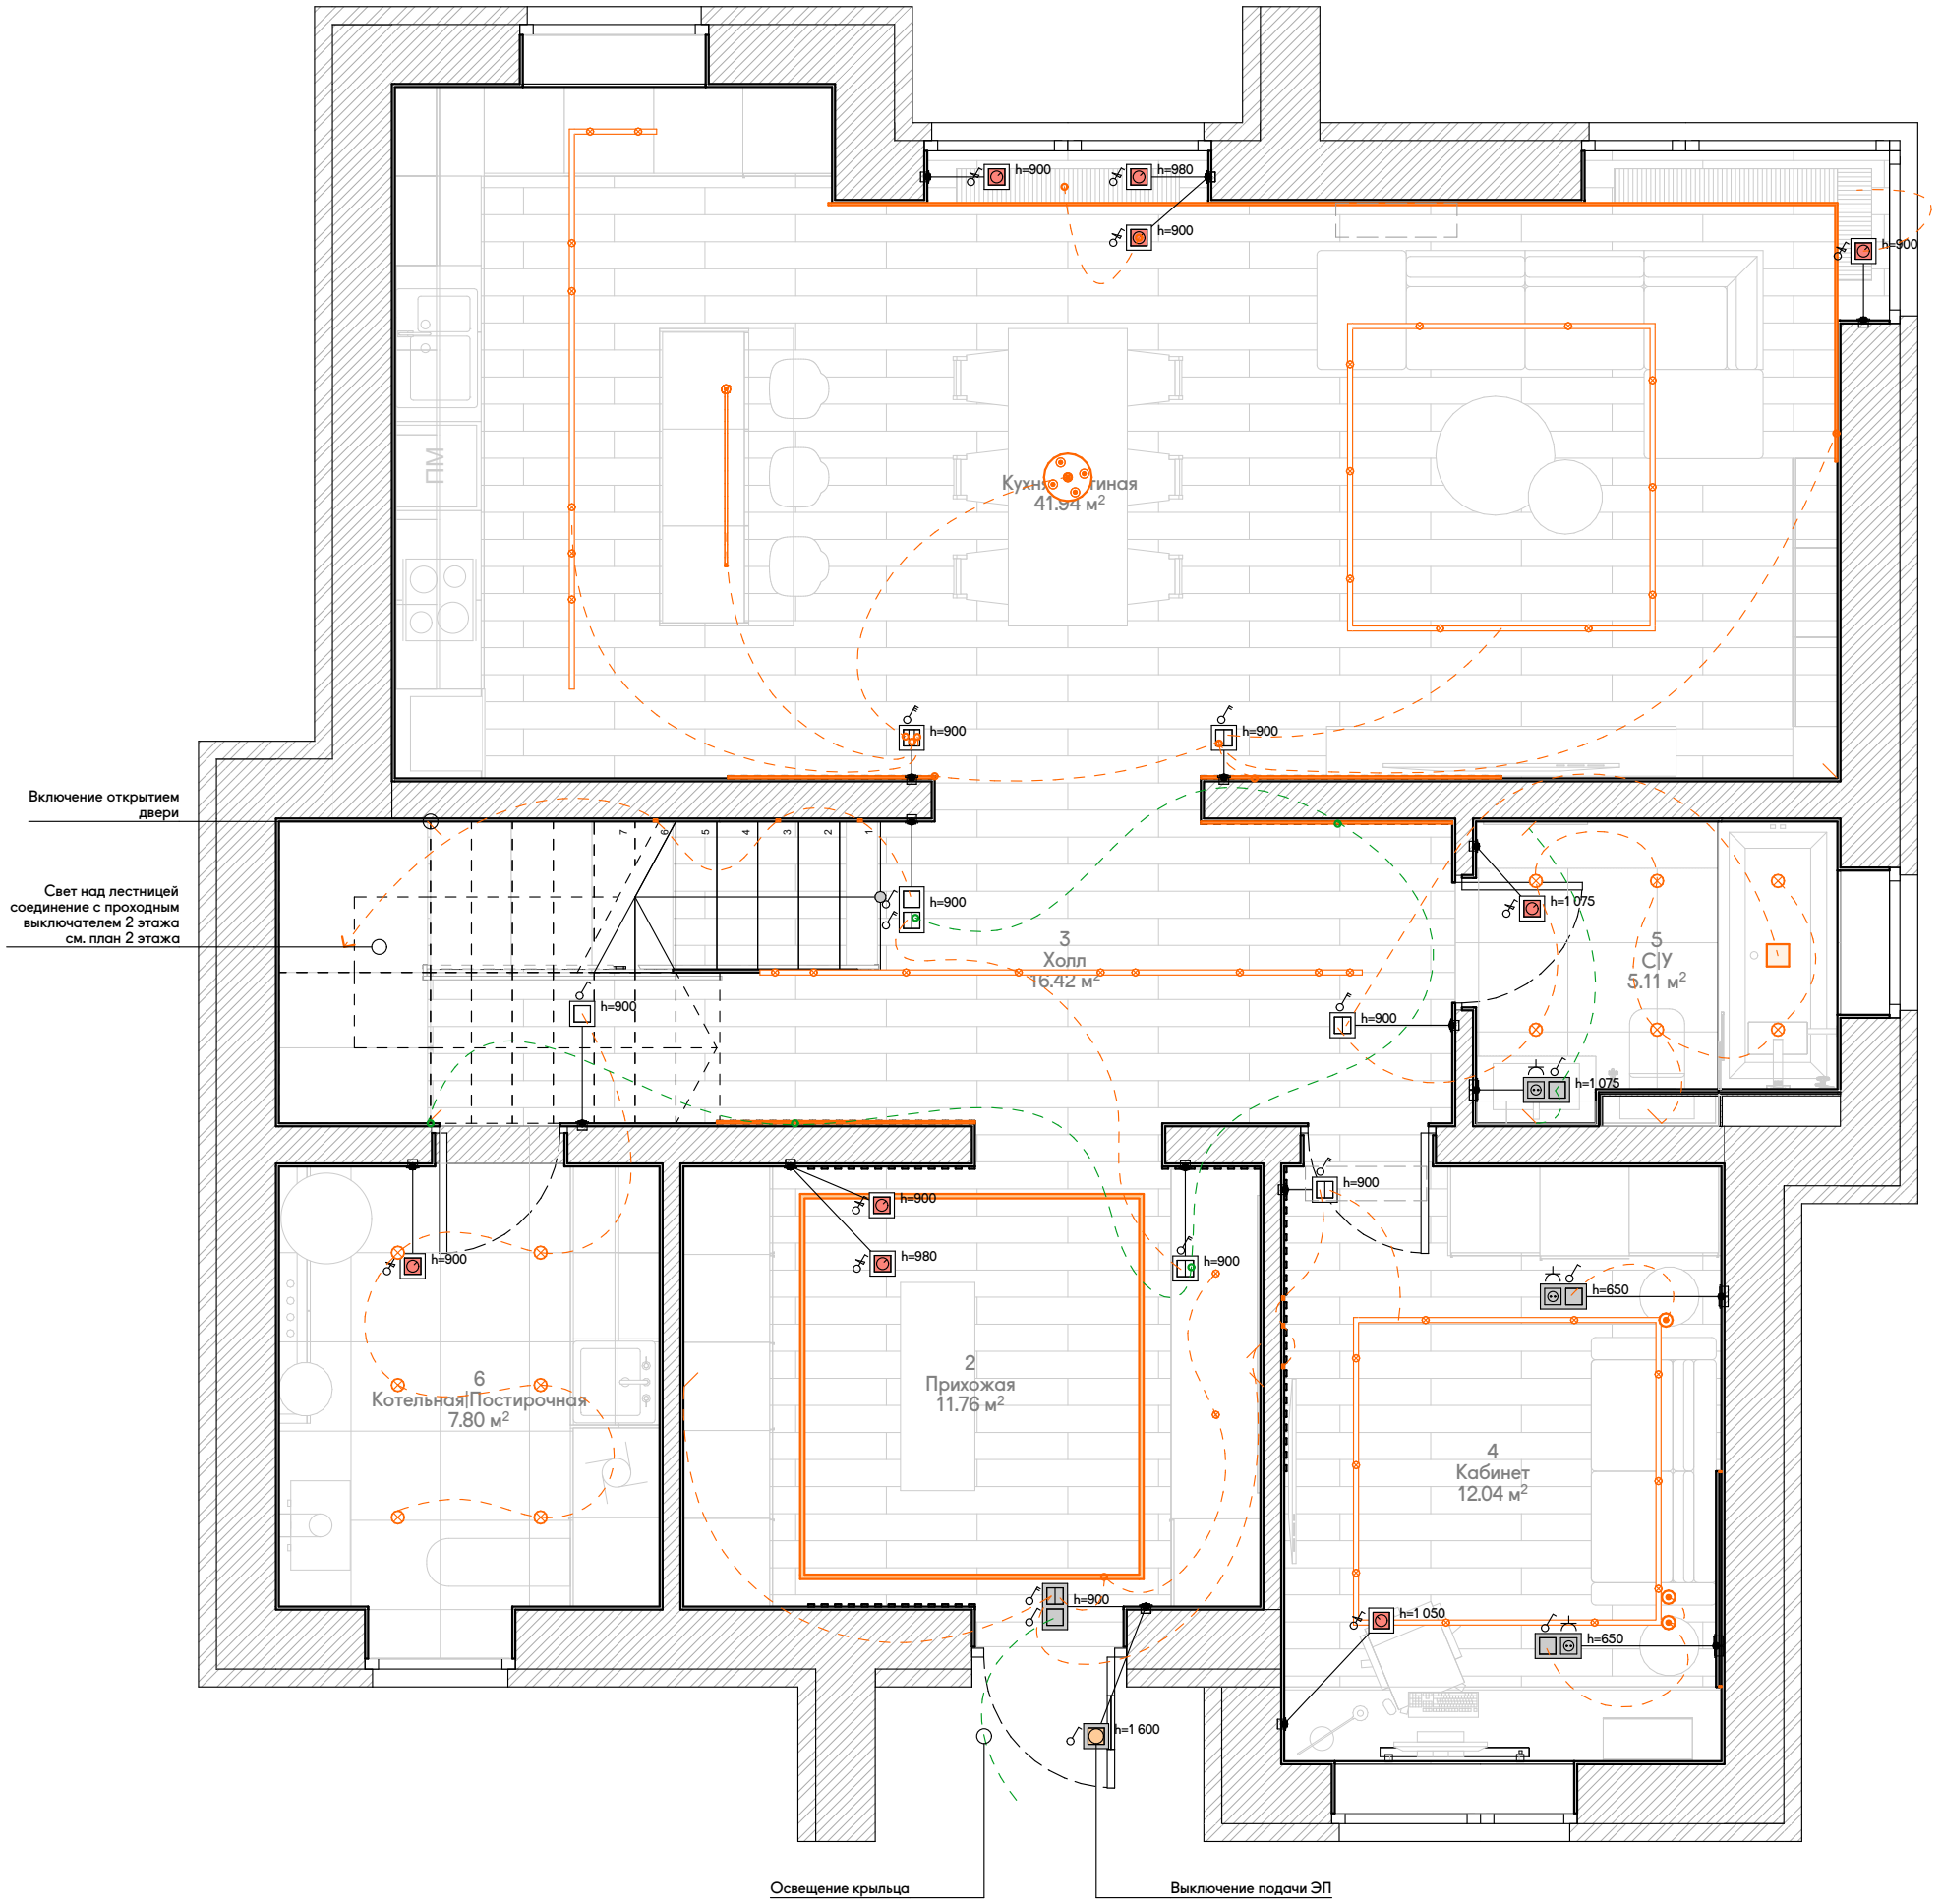

*Схематичное изображение выключателей и рамок на плане показано лицевой стороной по отношению к смотрящему

Изм.	Кол.уч	Лист	Док.	Подпись	Дата	ОРИОН-180	Стадия	Лист	Листов
Рук.Маст.		Каличкин А.Д.					Р	111	141
ГАП		Пономарев А.А.							
Архитектор		Муратов Р.Р.				Схема управления электроприборами			

А510

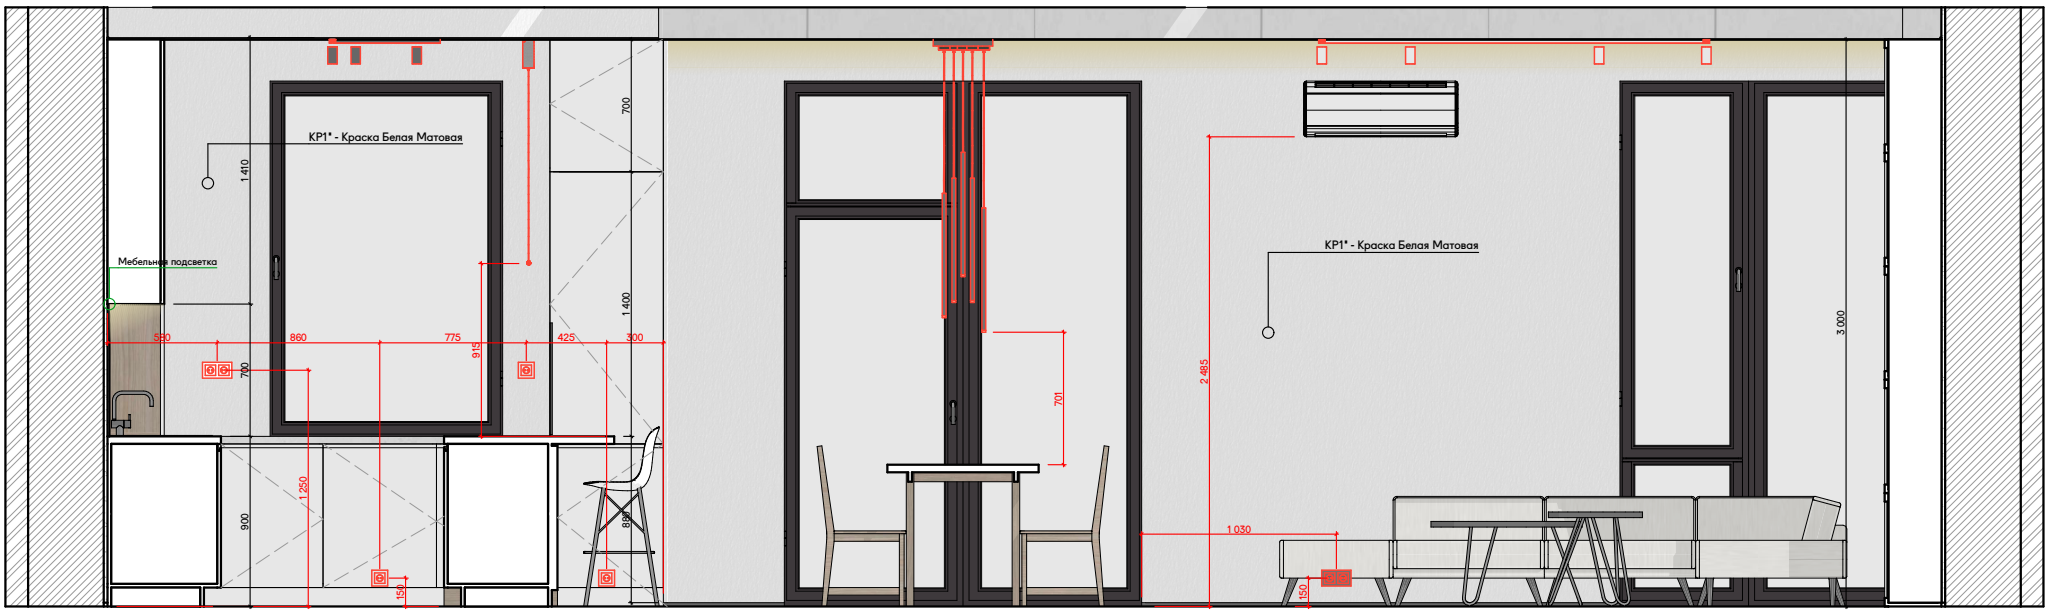

1 Кухня|Гостиная С1 Разрез 1:40

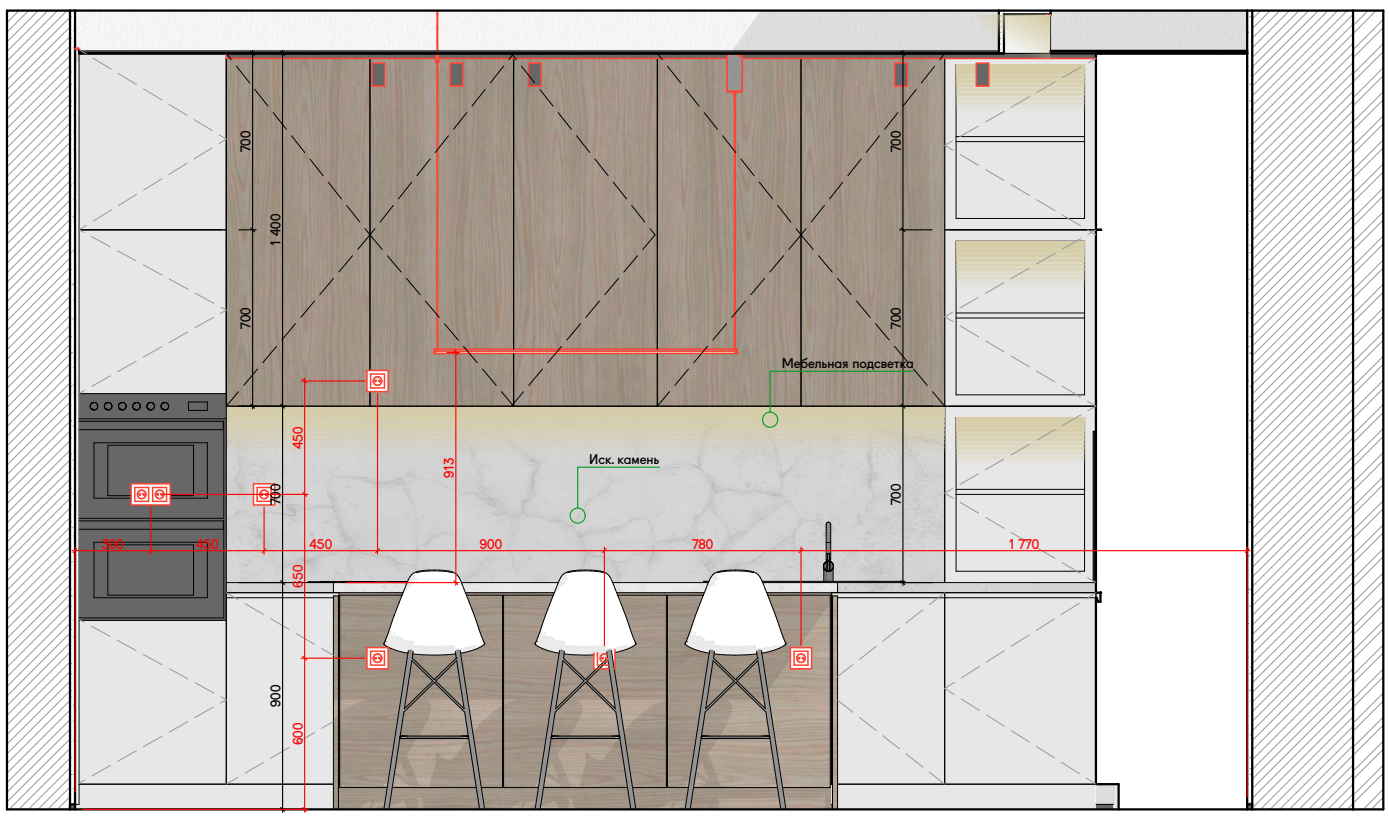

1 Кухня|Гостиная З1 Разрез 1:30

Изм.	Кол.уч	Лист	Док.	Подпись	Дата	ОРИОН-180	Стадия	Лист	Листов
Рук.Маст.		Каличкин А.Д.					Р	117	141
ГАП		Пономарев А.А.							
Архитектор		Муратов Р.Р.				Гостиная С 3			

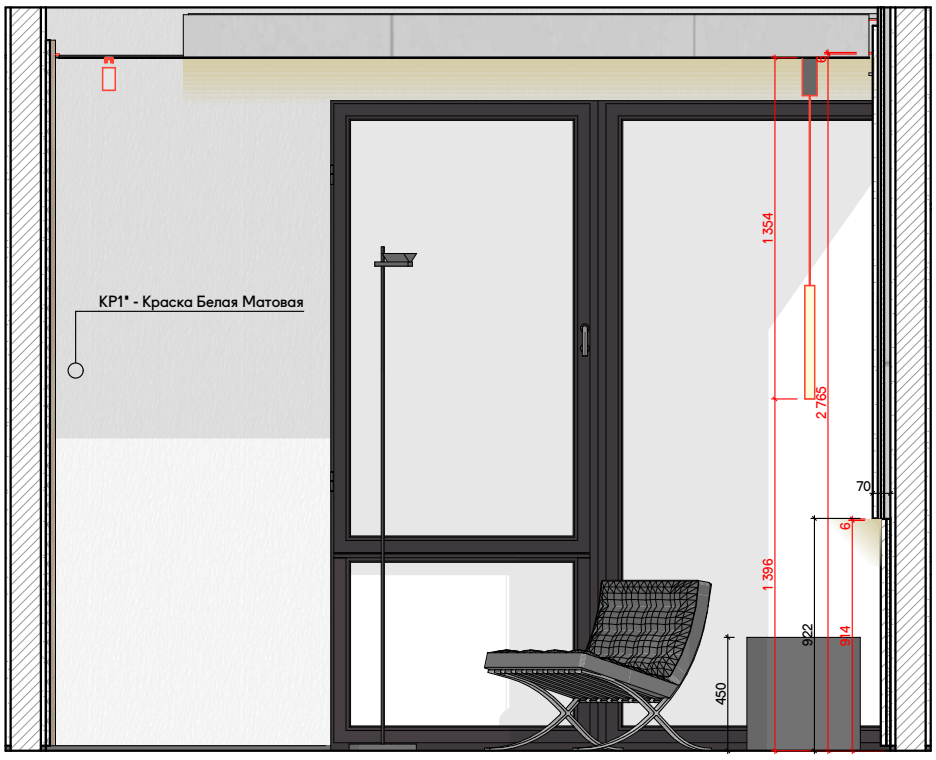

8 Мастер-спальня С Разрез 1:30

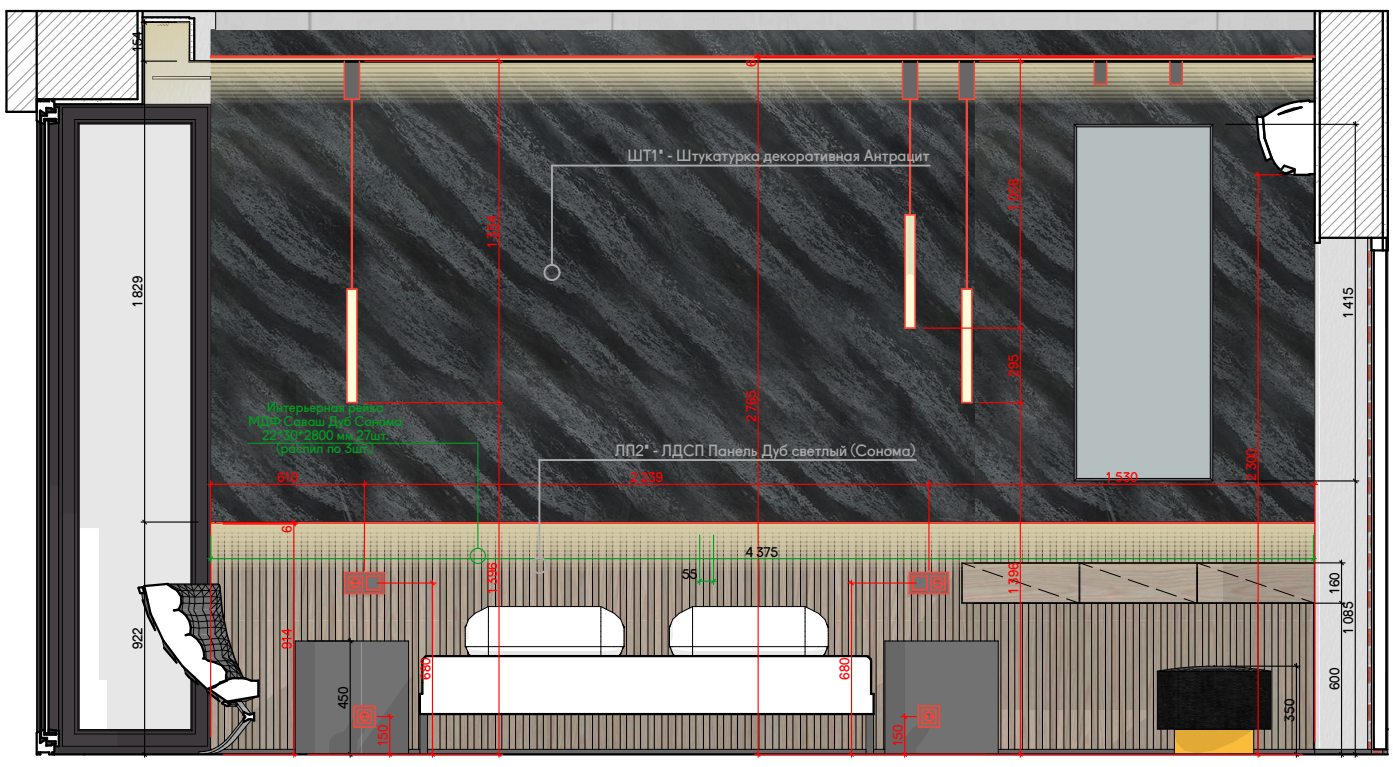

8 Мастер-спальня В Разрез 1:30

Изм.	Кол.уч	Лист	Док.	Подпись	Дата	ОРИОН-180	Стадия	Лист	Листов
Рук.Маст.		Каличкин А.Д.					Р	130	141
ГАП		Пономарев А.А.							
Архитектор		Муратов Р.Р.				Мастер-спальня С 3			